

電気設備工事 1

(一般共通事項)	
1 一般事項	
1) 構成	本特記仕様書は、一般共通事項及び工事種目別概要により構成する。
2) 適用範囲	本特記仕様書は、設計図及び各共通仕様書に記載なき事項を特記するものであり 各工事種目に於て他の工事との関連ある事項は、各々該当工事項目の記載事項を適用する。
3) 適用項目	本特記仕様書は、項目の番号に 〓印の付いた項目は適用しない。 特記事項の内、選択する項目は○印の付いた事項を適用し、・印の付いた事項は適用しない。
2 工事概要	
1) 工事名称	(仮称) 墨田区石原2丁目計画 新築工事
2) 建築主	社名・代表者・合同会社テラバイト両国 代表社員 一般社団法人テラビット両国 職務執行者 出澤貴人
3) 工事場所	住 所 : 東京都中央区京橋2-12-6 A0J税理士法人内 地名地番 : 東京都墨田区石原二丁目13番9 住居表示 : 東京都墨田区石原二丁目19番以下未定 状 況 : ○一般地 ・寒冷地 ・埋立地
4) 地域地区	用途地域・商業地域 防火地域 : ○防火地域 ・準防火地域 ・指定なし
5) 主要用途	寄宿舎
6) 防火対象物区分	5 項 (ロ) (消防法施行令別表第一) 有窓無窓区分: ○有窓階 ・無窓階 (全階) (消防法施行規則第5条の二)
7) 工事種別	○新築 ・増築 ・改築 増改築考慮: ・有 ○無
8) 主要構造	・SRC ○RC ・S ・PC
9) 予定工期	令和 年 月 日 ～ 令和 年 月 日
10) 工事規模	敷地面積: 意匠図による 建築面積: 意匠図による 延床面積: 意匠図による (付属 m ² ○含まず ・含む) 棟・戸数: 1棟 4 2戸 (寄宿舎) 階 数: 地上 7 階、塔屋 0 階
11) 特殊法規指導要綱	
12) 竣工後の管理	○ビル管理会社へ委託 ・自社管理 ・自主管理 有資格者 ・ ・
3 工事種目	
1) 電気設備	○受電設備 (・キュービクル ○低圧架空 2 条引込) ・電話交換機設備・防排煙設備 ・発電機設備 ○インターホン設備 ・非常警報設備 ・蓄電池設備 ・拡声放送設備 ○機械警備設備 ・中央監視設備 ○テレビ共聴設備 ○避雷設備 ○幹線設備 ・呼出表示設備 ○接地設備 ○動力設備 ・電気時計設備 ・有線放送設備 ○電灯コンセント設備 ○自動火災報知設備 (防排煙含む) ○I T V 設備 ○電話配管配線設備 ○電気錠設備 ○インターネット設備
2) 輸送設備 (参 考)	○エレベーター設備 ・エスカレーター設備 ・駐車設備 (エレベーター工事)
4 別途工事	
1) 一般事項	別途工事についての工事工程及び納まりに関しては、別途工事業者と密接に連絡し 調整に当たらなければならない。 負担金等の別途工事項目の官公庁及び関連各供給会社等への諸手続きは、総て請負 者の責任に於て行い、それに必要な諸費用は請負者の負担とする。
2) 別途工事・項目	○電力、電話局線引込みに伴う外線工事及びその負担金 ○ビル陰に依る電波障害対策工事費 (タワークレーン等工事上の問題は除く) ○近隣対策費 (工事上の問題は除く) ○電話機器供給取付工事 ○警備保障工事 ・看板灯、ネオンへの電源供給及び機器供給取付工事 ○住居内居室部分の照明器具供給取付工事 ・

5	工事仕様	
1)	共通仕様書	設計図及び特記仕様書に基づいて施工するほか、電気設備技術基準、内線規程、消防法その他関係諸官公署規定による。 設計図及び特記仕様書に記載なき事項は下記を共通仕様書とし、内容に相違ある場合は、係員の指示に従い施工する。 ○「公共建築工事標準仕様書（電気設備工編）」最新版
2)	共通事項	
1)	設計図書等の優先順位	設計図書とは、現場説明書及び質疑応答書、特記仕様書、設計図及び共通仕様書をいい、その優先順位は下記による。 (1) 事業主設備仕様書 (2) 見積要素綱及び現場説明書(質疑応答書含む) (3) 標準仕様書 (4) 役所協議済図書(確認申請、開発許可、条例、指導要綱、届出、所管庁議事録 (5) デザイン資料(外観・エントランス等) (6) 特記仕様書 (7) 各設計図書 ※(1)については工事期間中に事業者が作成するものであり、請負者は係員と共に作成協力するものである事。 ※上記各図書中(1)及び現場説明書除く)細断疑義あるものは質疑応答書により係員に確認する事。確認が無き場合、本工事費が発生する項目は、それを優先とする
2)	施工基準	工事に関係ある諸法規及び法令、規則、条例並びに関連各供給会社諸規定を遵守し設計図書に基づき、設置された設備がその機能を完全に発揮するように誠実良好且つ安全に施工する。
3)	係員の定義	係員とは、工事請負契約書に記載された工事監理者又は監督員により、電気設備工事に関して工事監理業務の代行を依頼された設備工事監理担当者とする。
4)	施工計画	実際の施工に先立って施工計画書・工程表・施工要領書・製作図・施工図書を作成し又施工図に基づき騒音、振動、耐震強度等を試算すると共に、係員の指定するものは試作を行い承諾を受ける事とし、これに要する費用は総て請負者の負担とする
5)	疑義	設計図書に記載がなくとも、工事上、納まりより当然必要と認められるものに関する費用は総て請負者の負担とする。 設計図書の内容に相違がある場合、表示が不明確な場合等の疑義は、工事契約以前に質疑 応答書をもって確認する。 設計図書と工事現場の状態で一致しない場合、予期する事が出来なかった特別な状態が発生し設計図書に示された条件を満足する事が出来なくなった場合等の疑義は速やかに書面をもって係員に通知し、その指示をうける。
6)	変更	工事施工に於いて、現場の納まり、取り扱いなどの関係上、取付位置、寸法、材料数量、取付工法等に関する軽微な変更に関する請負金額の増減は行わないものとする。上記以外の設計変更は、工事契約約款の定め等によるほか、係員と協議によりその都度定める。
7)	諸手続き	工事着手以後の官公庁及び各関連供給会社等への諸手続きは、総て請負者の責任に於いて行い、それに必要な諸費用は請負者の負担とする。
8)	現場代理人	必要資格を有する者で経歴書及び会社組織表を提出し、係員の承諾を得た者とする。 ・ ・
9)	協力業者	協力業者は工事契約後速やかに選定し、そのリストを提出し係員の承諾を得る。 協力業者の現場担当者は、現場代理人と同様の資格を有する者で、経歴書及び会社組織表を提出し、係員の承諾を得た者とする。
10)	機器・機材	本工事に使用する機器・機材は、発生材再使用及び支給品の指定がある場合を除き新品を使用する。 機器・機材メーカーは、原則として後欄のメーカーリストより選定し、工事契約後速やかにメーカーリストを作成し、係員の承諾を得る。これによれない場合は、同等品製造メーカーより選定し、理由書を添えて係員に提出し承諾を得る。 機器に関しては、仕様及び寸法、能力選定図、配線図、外形図等を記した機器図を作成し係員の承諾を得る。又、美観上特に注意しなければならないものとして係員指定したものについては、見本品を提出し、承諾を得ることとし、これらに要する費用は総て請負者の負担とする。 ・ ・ ・
11)	試験・検査	工程の必要な段階に於て、機器・機材の試験検査を行う。 機器・機材のうち輕易なもの及びJIS・JAS・B.L等の表示マークを付けたもので係員の承諾を得たもの、あるいはメーカーの試験成績書・検査証を提出し、係員に認められたものに関しては、試験検査を省略する。 ・ ・ ・
12)	係員事務所	係員事務所は工事監理事務所内に設ける。 係員事務所の運営に係る諸費用は総て請負者の負担とする。 上記によれない事情のある場合は、係員と協議の上その都度定める。
13)	工事に用電力・水	工事に使用する電力・電話・水・排水・ガス等の諸料金は総て請負者の負担とする。
14)	電気料金等	建物引き渡し迄の電気の使用料（基本料金共）及び消火器は見積金額に含める。 ・ 主任技術者に係る受電までの費用： ・ 施主 ・ 施工者 ・ 主任技術者の申請費・初回金： ・ 施主 ・ 施工者 ・ 受（変）電設備の保守料： ・ 施主 ・ 施工者 ○ 受電設備の基本料金： ・ 施主 ○ 施工者 ○ 受電設備の使用料金： ・ 施主 ○ 施工者

5	埋め戻し ・残土処分	埋め戻し土は山砂とすることを原則とするが、根切り土の内ガラ等を含まない良質なものは係員の承諾を得て使用することが出来る。 残土は構外に搬出し処分することとし、これに要する諸費用は、総て請負者の負担とする。
16	試運転調整	各設備は完成時に試運転を行い、その機能が充分に発揮される様調整を行う。 試運転調整に際し、係員と協議の上、絶縁・接地・電圧・電流・照度・騒音・振動音量等を測定し、測定結果を係員に提出し、承諾を得る。
7	施工の検査	施工の一工程が完了した時、係員が指定した工程に達した時、工事が完成した時には係員による外観、作動、機能、安全等の諸検査に合格しなければならない。又、工事完成時には係員と協議の上日時を定め、関係各官公庁及び供給会社の行う検査に合格しなければならない。 建物引渡し後1年を経た時点で、発注者及び工事監理者と協議の上、経年検査を行う。 上記各検査に伴い改善の必要が生じた場合は、請負金額の増減なく指示に従わねばならない。
18	説明板	係員と協議の上、主要な設備機器類及び一連の装置などの取扱要領及び重要な定期点検項目を記した説明板を作成し、指示する場所に取り付ける。
19	予備品	竣工時に納入する予備品は下記とする。 ○ キュービクル、配電盤、制御盤、監視盤、火報受信機等の表示及び制御回路に用いるランプ、ヒューズ類は現用数の各々10%以上、最低2個。 ○ 照明ランプは、現用数の10%以上。 ・ ・
20	工事保証	建物竣工引渡し後1年以内、B.L認定品にあつては2年以内、その他特別に定めのある場合は、その年数以内に、製品及び工事不良等の理由により生じたとされる損害は、請負者の費用負担にて迅速且つ丁寧に復旧すること。
21	その他	係員が工事完成迄の過程に於て必要と認め指示する事項は、厳に遵守しなければならない。
22	竣工時引渡し図書	本工事の竣工時引渡し書類は以下に定めるものの他、係員が必要に応じて定めるものとし、竣工後速やかに提出するものとする。 ○ 竣工図 (B5版、折込、黒表紙、金文字製本) ○ 竣工図 (原図寸法版、観音製本、黒文字) ○ 竣工図 (A3版、縮小観音製本、黒文字) ○ 官公庁等の許認可書類 ○ 機器完成図 ○ 機器納入業者一覧表 (メーカー、代理店、住所、電話番号、担当者) ○ 機器取扱説明書 ○ 試運転調整記録 ○ 予備品、付属品リスト ○ 非常時連絡先一覧表 ・ ・ ・ (部数は後日指示)

メーカーリスト	本工事の見積と施工にあたっては「指定材料及び施工業者リスト」を尊重すること。	
C D管・F E P管	○古河電工	
ポリブテン管	○三菱樹脂	
タイガースポリマー	○矢崎総業	
電線管及付属品	○丸一鋼管	
電線ケーブル	○日立電線 ○麻倉	
照明ポール	○昭和アルミビューテック ○住軽日経エンジニアリング	
避雷針	○東京避雷針 設計課 村杉氏 03-3372-5261	
インターホン	○アイホン営業本部 市場開発部 市場開発第一課 菊池氏 TEL03-5684-3415	
延焼防止材	○ネグロス電工 ○古河電工 ○日立電線	
ケーブルラック・ダクト	○ネグロス電工	
T V 共聴	○マスプロ電工	
照明器具	○パナソニック ○東芝ライテック ○達磨	
防炎機器	○アイホン営業本部 市場開発部 市場開発第一課 菊池氏 TEL03-5684-3415	
各戸分電盤	○カウムラ ○パナソニック	
壁 類	○カウムラ ○パナソニック	
変 圧 器	○日立製作所 ○東芝 ○大阪変圧器 ○高岳製作所	
ハンドホール	○インテック ○土井 ○関根	
エアコンホルダー	○ネグロス電工	
ケーブル貫通不延焼防止工事	○中央防災技研	
遮断器	○日立製作所 ○東芝	
高压開閉器	○日立製作所 ○東芝	
避雷器	○日立製作所 ○東芝	
コンデンサ	○日立製作所 ○東芝	
キュービクル	・日本電機産業 ・河村 ・パナソニック	
配線用遮断器	○三菱 ○東芝 ○パナソニック	
配線器具	○パナソニック ○niratap/NKシリーズ	
呼出表示装置	・アイホン ・パナソニック	
監視カメラ	・ギガプライス	
インターネット	○N T T 東日本 ・ギガプライス	
電気錠	○MIWA	
無人通報システム・全日警	
発電機	・日立製作所 ・東芝 ・川崎重工 ・新潟鉄工所	
蓄電池	・新神戸電機 ・日本電池	
電話交換機器	・岩崎エンジニアリング ・松下通信機器 ・沖電気工業	
拡声機器	・T O A (03-5621-5761 防災システムグループ 塚田氏)	
C A T V	・ J - C O M	
凡 例	本工事の図面に使用する記号は以下とする。 但し、詳細図等でこれによることが不適当であると判断される場合は、この限りではない。 <table> <tbody> <tr> <td>天井いんべい配線</td><td>開閉器 電流計付開閉器</td></tr> <tr> <td>床いんべい配線</td><td>電磁開閉器 カットアウトスイッチ</td></tr> <tr> <td>地中埋設配線</td><td>電話アウトレット(壁付 床)</td></tr> <tr> <td>空 配 管</td><td>端 子 盤</td></tr> <tr> <td>引下げ 立上り 素通し</td><td>スピーカー ホーン形スピーカー</td></tr> <tr> <td>電灯回路番号(200V、100V、動力回路)</td><td>音量調整器</td></tr> <tr> <td>ジャンクションボックス プルボックス</td><td>増 幅 器</td></tr> <tr> <td>V V F 用ジャンクションボックス</td><td>マイクロホンジャック</td></tr> <tr> <td>ハンドホール マンホール</td><td>インタ ーホーン機 報機</td></tr> <tr> <td>蛍 光 灯</td><td>ベル ブザー チャイム</td></tr> <tr> <td>白熱灯(直付け ダウンライト)</td><td>警報ベル 警報ブザー</td></tr> <tr> <td>ペンダント ブラケット</td><td>押しボタ ン 警報押しボタ ン</td></tr> <tr> <td>放電灯(蛍光灯を含まず)</td><td>警報受信盤</td></tr> <tr> <td>誘 導 灯</td><td>U H F 、V H F アンテナ</td></tr> <tr> <td>非常照明灯</td><td>B S アンテナ</td></tr> <tr> <td>屋 外 灯</td><td>混合器 分波器</td></tr> <tr> <td>コンセント(壁付 床)</td><td>分岐器 分配器</td></tr> <tr> <td>単極スイッチ パイロットランプ</td><td>T V アウトレット(75Ω)</td></tr> <tr> <td>2極スイッチ 3路スイッチ 4路スイッチ</td><td>スポット型 感知器</td></tr> <tr> <td>換 気 扇</td><td>煙感知器</td></tr> <tr> <td>電動機 電加熱</td><td>P 型 発信機 警報ベル 標識灯</td></tr> <tr> <td>フロートスイッチ フロートレススイッチ電極</td><td>火災報知機受信盤</td></tr> <tr> <td>電灯分電盤</td><td>火災報知機副表示機</td></tr> <tr> <td>動力分電盤 動力制御盤</td><td></td></tr> <tr> <td>直流分電盤</td><td></td></tr> <tr> <td>引込開閉器盤</td><td></td></tr> </tbody> </table>	天井いんべい配線	開閉器 電流計付開閉器	床いんべい配線	電磁開閉器 カットアウトスイッチ	地中埋設配線	電話アウトレット(壁付 床)	空 配 管	端 子 盤	引下げ 立上り 素通し	スピーカー ホーン形スピーカー	電灯回路番号(200V、100V、動力回路)	音量調整器	ジャンクションボックス プルボックス	増 幅 器	V V F 用ジャンクションボックス	マイクロホンジャック	ハンドホール マンホール	インタ ーホーン機 報機	蛍 光 灯	ベル ブザー チャイム	白熱灯(直付け ダウンライト)	警報ベル 警報ブザー	ペンダント ブラケット	押しボタ ン 警報押しボタ ン	放電灯(蛍光灯を含まず)	警報受信盤	誘 導 灯	U H F 、V H F アンテナ	非常照明灯	B S アンテナ	屋 外 灯	混合器 分波器	コンセント(壁付 床)	分岐器 分配器	単極スイッチ パイロットランプ	T V アウトレット(75Ω)	2極スイッチ 3路スイッチ 4路スイッチ	スポット型 感知器	換 気 扇	煙感知器	電動機 電加熱	P 型 発信機 警報ベル 標識灯	フロートスイッチ フロートレススイッチ電極	火災報知機受信盤	電灯分電盤	火災報知機副表示機	動力分電盤 動力制御盤		直流分電盤		引込開閉器盤	
天井いんべい配線	開閉器 電流計付開閉器	
床いんべい配線	電磁開閉器 カットアウトスイッチ	
地中埋設配線	電話アウトレット(壁付 床)	
空 配 管	端 子 盤	
引下げ 立上り 素通し	スピーカー ホーン形スピーカー	
電灯回路番号(200V、100V、動力回路)	音量調整器	
ジャンクションボックス プルボックス	増 幅 器	
V V F 用ジャンクションボックス	マイクロホンジャック	
ハンドホール マンホール	インタ ーホーン機 報機	
蛍 光 灯	ベル ブザー チャイム	
白熱灯(直付け ダウンライト)	警報ベル 警報ブザー	
ペンダント ブラケット	押しボタ ン 警報押しボタ ン	
放電灯(蛍光灯を含まず)	警報受信盤	
誘 導 灯	U H F 、V H F アンテナ	
非常照明灯	B S アンテナ	
屋 外 灯	混合器 分波器	
コンセント(壁付 床)	分岐器 分配器	
単極スイッチ パイロットランプ	T V アウトレット(75Ω)	
2極スイッチ 3路スイッチ 4路スイッチ	スポット型 感知器	
換 気 扇	煙感知器	
電動機 電加熱	P 型 発信機 警報ベル 標識灯	
フロートスイッチ フロートレススイッチ電極	火災報知機受信盤	
電灯分電盤	火災報知機副表示機	
動力分電盤 動力制御盤	
直流分電盤	
引込開閉器盤	







Date	Revision	Ok.	Date	Revision	Ok.	Checked	Date	Drawn	Date	Project title	Scale	Unit
										(仮称)墨田区石原2丁目計画		MM
										Sheet content	Sheet No.	
										特記仕様書 (1)		E - 01

(設備工事概要)		
1. 契約種別	A. 一般用 ・業務用電力・高圧電力・従量電灯○低圧電力・深夜電力 B. 共同住宅用 ・共用部 ・業務用電力 ・低圧電力 ○従量電灯 (・A ・B ○C) ・住戸部 ・低圧電力 ○従量電灯 (・A ○B ・C) ・深夜電力	
2. 計量	A. 一般用 B. 共同住宅用 ○共用部 電灯、動力一括計量 ○住戸部 各戸計量	
3. 計算条件 (共同住宅用)	住戸用幹線容量 (1住戸の最大負荷容量) ○1K (入居時 30A) 最大4KVA ・1DK (入居時 40A) 最大6KVA ・2LDK (入居時 40 A) 最大8KVA 住戸用幹線の総合需要率 住戸数n → ∞ 4.6 % ・住戸冷暖房 (冷房) (暖房)	
4. 引込	引込方式 ・1回線○2回線 () ○低圧架空2条引込 引込電圧 ・特高 ・高圧 ○低圧 3φ3W 6600V 50Hz φ W V Hz キャビネット ・有 ○無 ・構内に東電柱建柱 引込開閉器 ○有 ・無	
5. 借受変電	集合住宅用変圧器 (色指定サービス)	
6. 自家受変電	形式 ・屋内 ○屋外 ○キュービクル ・開放形 ケ所 受電盤 主遮断器 高圧真空遮断器 遮断容量 200A 配電盤 面 変圧器 ○油入 ・不燃油 ・油入窒素封入 ・乾式 種 三相 1台 単相 1台 合計 130 KVA コンデンサー 三相 1台 合計 35.3Kvar 保護方式 受電 ・変圧器 ○コンデンサー 力率調整 ○有 ・無 リアクトル ○有 ・無 資格者主任技術者 ・不要 ・要 3種 ○キュービクルは、屋外型仕様とし、消防告示7号キュービクル式非常電源専用受電設備 認定基準等に適合したものとする。(耐重塩害仕様) エンジン形式 ○ディーゼル ・ガスタービン 出力 PS 冷却方式 ○水冷 ・空冷 ○ラジエター 起動方式 ○自動 ・手動 ・バッテリー ・圧縮空気 起動時間 ○40秒 (一般) ・10秒 燃料 ディーゼル軽油 発電機 3φ 3W 200V 138KVA 110.4KW 極数 4極 力率改善 80% (遅れ) 形状 ・開放型 ○キュービクル ○屋外 ・屋内) ○超低騒音 75dB ・寒冷地仕様 用途 ・ELV (一般・非常) ○消火栓 ・スプリンクラー ○泡消火 ○非常用コンセント ・非常照明	
7. 発電機		
8. 蓄電池	形式種類 ・キュービクル ・開放形 蓄電池種類 (・鉛 ・アルカリ) 登降機 入力 AC φ W V 出力 DC V / cell Ah / HR 用途 ・非常照明 ・誘導灯 ・排煙ダンパー ・操作用	
9. 中央監視	方式 ・CRT ・グラフィックパネル ・液晶表示 受変電 ・操作 ・表示 ・記録 ・計量 ・計測 動力 ・操作 ・表示 ・記録 ・計量 ・計測 照明 ・操作 ・表示 ・記録 ・計量 ・計測 発電機 ・操作 ・表示 蓄電池 ・表示 停電補償 時間 CVCF ・有 ・無	

10. 幹線	一般用 (共用) ・集合受託用変圧器からの供給 ○動力 3φ 3W 200V ○配管 ○ケーブル ・バスダクト ・金属ダクト ○メッセンジャー ○電灯 1φ 3W 100/200V ○配管 ○ケーブル ・バスダクト ・金属ダクト ○メッセンジャー ○非常用 ○非常コンセント 1系統 ・屋内消火栓 ・泡消火 B. 共同住宅用 引込開閉器盤 ○自立 ・壁掛 ・開放 ・閉鎖 系 統 数 ○住戸用 4系統 配線方式 共用動力 3φ 3W 200V ○配管・分岐ケーブル (○CV・VV○CVT) 共用電灯 1φ 3W 200/100V ○配管・分岐ケーブル (○CV・VV○CVT) 住戸用電灯 1φ 3W 200/100V ・配管○分岐ケーブル (・CV・VV○CVT) 非常用電灯 1φ 3W 200/100V ○配管・分岐ケーブル (○FPT) 非常用動力 3φ 3W 200V ・配管・分岐ケーブル (・CV○FPT)	
11. 動力	電 圧 3φ 3W 200V ○配管 ○ケーブル 分電盤・制御盤 ○壁掛 ・埋込 ○自立 ・ユニット 制御方式 ○遠方 ○自動 ○連動 ○手動 表 示 ・電源 ○運転 ・停止 ○満減水 ○故障 監視警報盤 ○満減水 ○故障 設置場所 管理員室	
12. 電灯	電 圧 1φ 3W 200/100V ○配管○ケーブル・バスダクト○ケーブルラック 分 電 盤 ○壁掛 ・埋込 ・自立 点 滅 器 300V 1P 15A コンセント125V 2P 15A ○壁・床 (・スタ ンド型 ・床収納型 納入数 ケ) プレート類 ・ステンレス ・新金属 ・プラスチック ・フルカラー ○miratap/NKシリーズ グレー・ブラックとする	
13. 照明器具	L E D ○一般型 非 常 灯 ○LED ○電源 (○内蔵 ・別置) 誘 導 灯 ○LED ・電源 (○内蔵 ・別置) 設計照度 700 ~ 1500 lx () 300 ~ 700 lx () 150 ~ 300 lx () 70 ~ 150 lx ()	
14. 電話配管配線	局線引込 ○架空 ・埋設 引込可能局線数 10P 屋内配管 ○配管 ○ケーブルラック ・フロアダクト 端 子 箱 ○MDF 10P+10P用 保安器スペース○有・無 10P ○IDF 7面 ○壁掛 (天井内に設置) アクトレット ○壁 ・床 ○各戸 各居室に設置 設置場所 洋室 1箇所	
15. 電話交換機	方 式 ・自営 ・直営 機 種 回 線 数 局線 本 内線 本 中 継 台 ・有紐 ・無紐 ・デスク型 ・卓上型 電 話 型 台 電話交換手 ・不要 ・要	
16. インターホン (オートロック)	用 途 ・夜間 ○訪問 ・保守 ・内部通信 方 式 ・親子 ・相互 ・複合 ○集合住宅 系 統 集合玄関機 → 室内親機 → 玄関子機 機 種 ○ハンズフリー型 ・拡声型 局 電 源 ○AC 100V ・DC V ・GC V 総務省令第40号対応 ○非接触キー装置・電気錠装置は、本工事とする。 用 途 ・呼出し ○非常 ・BGM ア ン プ 卓上型 ・デスク型 ・ロッカー型 ○壁掛型 出力120W 出力回路 回路 大出力回路 回路 付 属 品 ・マイク・プレーヤー・レコーダー ・ラジオ ・CMマシン ・BGM装置 ○非常電源装置 スピーカ ○天井埋込型 3W ・壁掛型 W ・トランペット型 W	
17. 拡声放送		
18. 電気時計	親時計 ・水晶 ・電波 ・音叉 出力 回路 ・壁掛 ・自立 子時計 ・有極 ・無極	

19. テレビ共聴	受信電波 ○地上波○BS○CS110度 ・CS (スカイパーフェクTV) アンテナ ○BS/CS110度900φ ・CS (スカイパーフェクTV) 900φ ○地上波デジタルUHFアンテナ20素子 分配方式 ○幹線分枝 ブースター・幹線増幅器○BS/CS110度/CATV ・CS (スカイパーフェクTV) アクトレット ○地上波デジタル/BS/CS110度共用1端子10MHz~3224MHz型 アクトレット ・CS (スカイパーフェクTV) 用1端子型 ○各戸 各居室に設置 設置場所 洋室1箇所 ※ブースターは別図参照	
20. 呼出表示設備 (浴室用)	用 途 ・防犯警報 ・表示 ・安全確保 表示盤 ・10窓 設置場所 管理室 機 器 ・ベル ・サイレン ・ブザー ・ランプ ・チャイム ・電子音 方 式 電 源 ・AC100 V ・DC V ・G C V	
21. 自動火災報知 (防火扉自閉 設備含む)	受信機 ○P型 設置場所 管理員室 感知器 ○スポット ○煙 発信機 ○P型 ○総合型式 他設備との関連 アリ ・ 総務省令第40号対応火災報知設備 ○インターホン設備 パッケージ型消火設備 ・ 非常放送設備 ○電気錠設備 ○オートドア	
22. ガス漏れ警報	ガ ス ○都市ガス ・LPG 他設備との関連 ○インターホン設備	
23. 防排煙	制御盤 1回線 設置場所 管理室 感知器 ○埋第3種 ・火報兼用 レリーズ ○シャッター ・重畳 ・防火戸 ・ダンパー ・排煙口 他設備との関連 アリ ○自動火災報知設備	
24. 非常警報	操作装置 回線 設置場所 方 式 他設備との関連	
25. 機械警備	制御盤 ○本工区内 (メーカーは現場にて決定) ○設置場所 管理員室 センサー類の供給取付及び配線工事 ○本工区内 配 管 ○本工区内 配 線 ○本工区内 接 地 電 源 ○AC 100V ・GC V 他設備との関連 ○警報盤、火報、インターホン、ELVインターホン、宅配ボックス	
26. 避雷針設備	方 式 ○突針 (基数 1) ○棒上導体 (種類 2.0/13オニヨリ) 引下導線 ・鉄骨アース ・鬼燈線 ○鉄筋アース 接地極 ・接地銅板 900×900×1.5t 2箇所 補助極 ・接地銅棒 10φ×500 1 4箇所 試験端子箱 ・露出 ○埋込 ○SUS ・塩ビ ・黄銅	
27. 接 地	用 途 ○集合住宅用変圧器 ○動力 ○電灯 ○電話 ○弱電 種 類 ○A種 ○B種 ○D種 ○C種 接地線 ○接地用IV線 接地極 ○接地銅板 (900×900×1.5t) 補助極 ○接地銅棒 (10φ×500) 1	
28. I T V	○ 監視カメラ設備 ○ 壁室にカメラドライブユニット、デジタルレコーダー、液晶モニターを設置する。 ○ ITV機器は別途工事、配管は本工事とする ○ 施主による指定業者工事	
29. インターネット 設備	○ MIWAとする。	
30. 電気錠システム 設備		

30. 共通事項	1. 床及び防火区画貫通部分は、国土交通大臣認定工法による防火区画貫通処理を行う。 2. 総ての空配管には、呼び線を挿入する。	
器具標準取付高さ	ス イ ッ チ 床 上 ボックス中心 ・1300 ○1250 ・ mm コンセント " " ・ 300 ○ 250 ・ mm 電話アクトレット " " ・ 300 ○ 250 ・ mm TVアクトレット " " ・ 300 ○ 250 ・ mm インターホン インターホン親機はスイッチ下端に高さを揃える事 上記設備をドア脇に設ける場合、ドア枠からボックス中心までの離れは150mmとする。 動 力 盤 床 上 盤上端 1800mm 電 灯 盤 " " 1800mm TV共聴盤 " " 1800mm 端 子 盤 " 盤下端 300mm	
1. エレベーター	・乗用 ・住宅用 ・人荷用 ・荷物用 ・非常用 1台 ・ロープ式 ・油圧式 積載量 600kg (定員 9名) スピード 45m / min 停止箇所 1階 ~ 5階 5ヶ所	
その他	(1) 建築設備の構造 建築設備の構造は、建築設備耐震設計・施工指針2011年版による (2) 弱電設備 (電話配管配線設備、テレビ共聴視設備、インターホン設備、ITV設備等) 電灯コンセント設備等で防火区画貫通部及び床貫通部は国土交通大臣認定の区画貫通処理 を行う事 (E-3図：建築基準法施行令129条の2の5 配電管設備の構造図参照) (3) 警報設備、LAN設備、監視カメラは再度、担当者と協議の上施工の事 (4) 電柱移設費は本工事とする。	

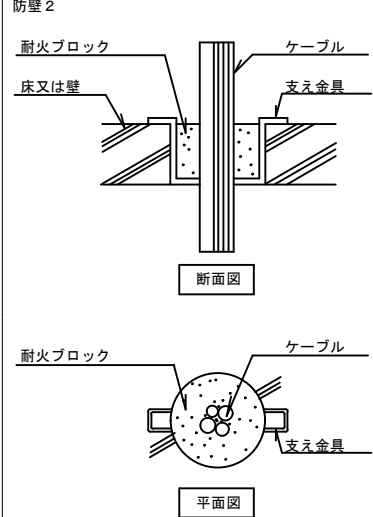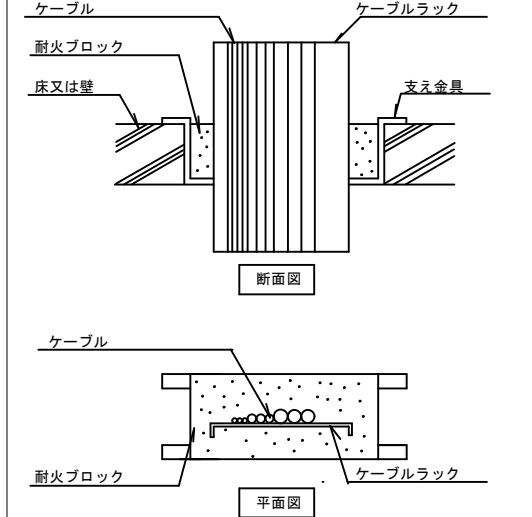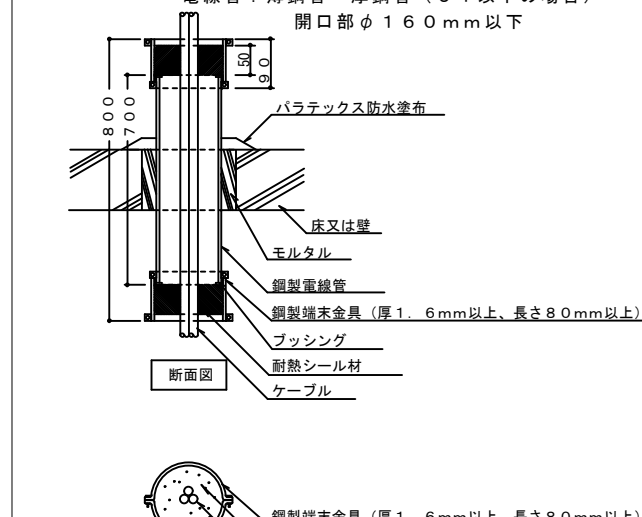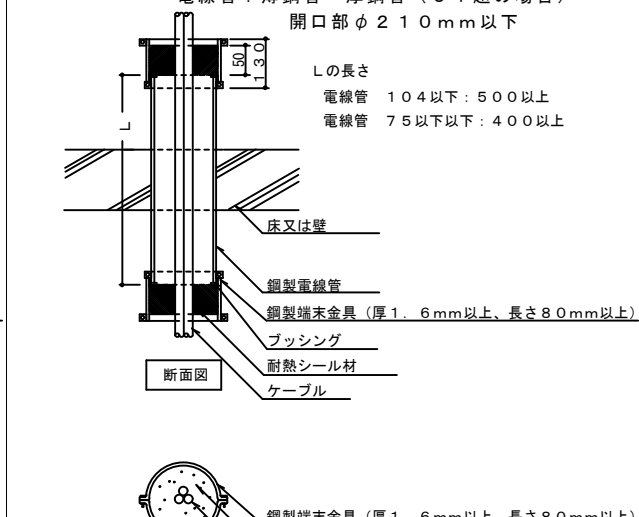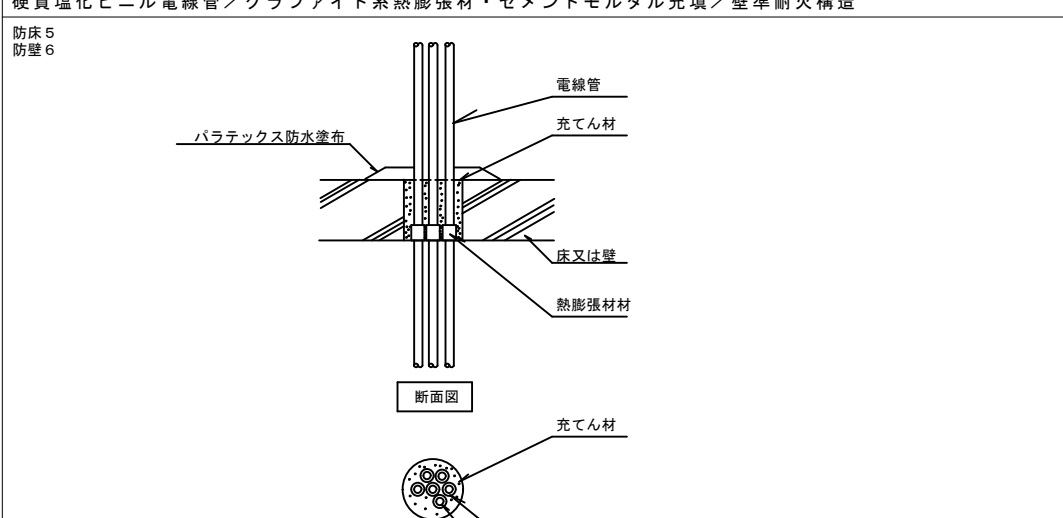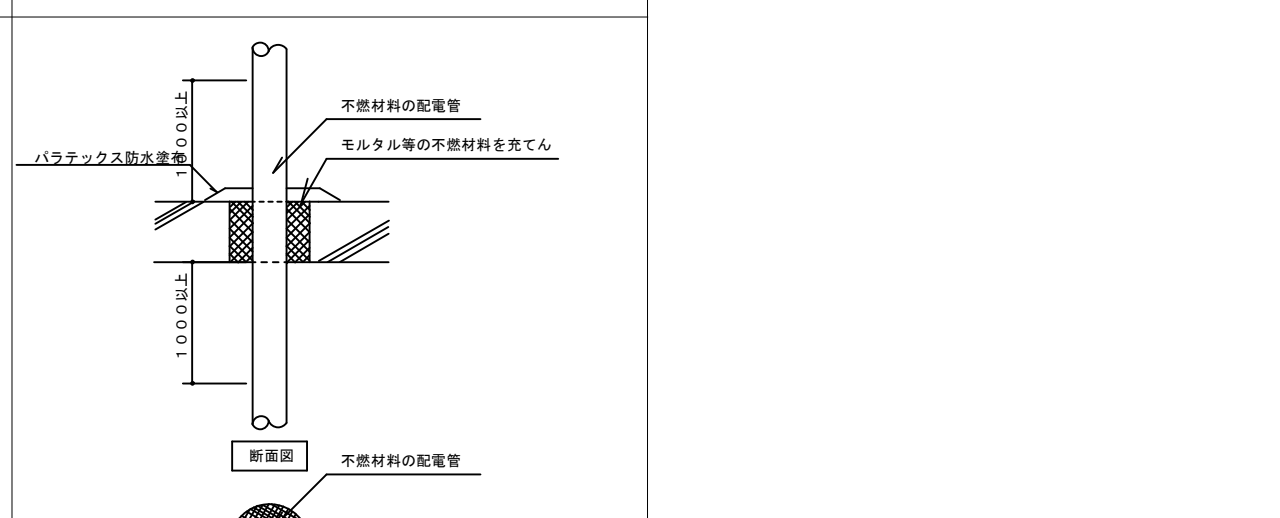ケーブルの床耐火構造貫通 ケーブルの壁準耐火構造貫通 防床1 防壁1 防壁2  （耐火ブロックの充てん） 耐火ブロックを適宜組み合わせて、隙間の無いように押圧してなじませながら、ケーブル周囲及び開口部に充てんする	ケーブル・ケーブルラックの床耐火構造貫通 ケーブル・ケーブルラックの壁準耐火構造貫通 防床2 防壁3  （耐火ブロックの充てん） ケーブルどうしの谷間など小さな隙間に小さい耐火ブロックを押圧してなじませながら充てんする。 次に、耐火ブロックを適宜組み合わせて、隙間の無いように押圧してなじませながら、ケーブル周囲及び開口部に充てんする	鋼製電線管／モルタル・水酸化カルシウム充てん／被膜電線／床 鋼製電線管／モルタル・水酸化カルシウム充てん／被膜電線／壁 防床3 防壁4 壁・床100mm以上の鉄筋コンクリート 電線管：薄鋼管・厚鋼管（51以下の場合） 開口部φ160mm以下  （断熱シール材の充てん） 電線管の両端外側のケーブル上に耐熱シール材を長さ50mm以上に充てんする。 耐熱シール材充てん部及びそれに連なる電線管端部を鋼製端末金具で覆う。 鋼製端末金具の締め具を締め付けて、鋼製端末金具を電線管端部に固定し又、耐熱シール材を締め付ける。	鋼製電線管／水酸化カルシウム充てん／被膜電線／床 鋼製電線管／水酸化カルシウム充てん／被膜電線／壁 防床4 防壁5 壁・床100mm以上の鉄筋コンクリート 電線管：薄鋼管・厚鋼管（51超の場合） 開口部φ210mm以下 Lの長さ 電線管 104以下：500以上 電線管 75以下以下：400以上  （断熱シール材の充てん） 電線管の両端外側のケーブル上に耐熱シール材を長さ50mm以上に充てんする。 耐熱シール材充てん部及びそれに連なる電線管端部を鋼製端末金具で覆う。 鋼製端末金具の締め具を締め付けて、鋼製端末金具を電線管端部に固定し又、耐熱シール材を締め付ける。
合成樹脂製可とう電線管／グラファイト系熱膨張材・セメントモルタル充填／床耐火構造 硬質塩化ビニル電線管／グラファイト系熱膨張材・セメントモルタル充填／床耐火構造 合成樹脂製可とう電線管／グラファイト系熱膨張材・セメントモルタル充填／壁準耐火構造 硬質塩化ビニル電線管／グラファイト系熱膨張材・セメントモルタル充填／壁準耐火構造 防床5 防壁6  （熱膨張材の取り付け） グラファイト系熱膨張材を書く配管に取り付け、所定の位置までスライドさせる。 開口部全体に隙間がないように、セメントモルタルで充てんし埋め戻す。充てん材硬化後隙間の無いことを確認する。	配電管が防火区画等を貫通する部分の構造  貫通部周囲の充てん材は、必要に才おじて脱着防止措置を施す。 配電管の貫通する部分及び防火区画等を貫通する部分からそれぞれ両側に1m以内の距離にある部分を不燃材料で造る。		

設備の構造については
建築基準法施行令第129条の2の4に準拠する

防床1	床貫通・ケーブル配線	PS060	FL-0050	防壁1	壁貫通・ケーブル配線（壁厚100mm以下）	PS060	WL-0293
防床2	床貫通・ケーブルラック	PS060	FL-0232	防壁2	壁貫通・ケーブル配線（壁厚100mm以超）	PS060	WL-0293
防床3	床貫通・薄鋼管・厚鋼管（51以下）	PS060	FL-9091	防壁3	壁貫通・ケーブルラック	PS060	WL-0231
防床4	床貫通・薄鋼管・厚鋼管（51超）	PS060	FL-9093	防壁4	壁貫通・薄鋼管・厚鋼管（51以下）	PS060	WL-9092
防床5	床貫通・合成樹脂管（CD／PF36以下）	PS060	FL-0298	防壁5	壁貫通・薄鋼管・厚鋼管（51超）	PS060	WL-9094
				防壁6	壁貫通・合成樹脂管（CD／PF36以下）	PS060	WL-0305

確認E-01



Date	Revision	Ck.	Date	Revision	Ck.	Checked	Date	Drawn	Date	Project title	Scale	Unit
										(仮称) 墨田区石原2丁目計画 新築工事		MM
										Sheet content		Sheet No.
										建築基準法施行令第129条の2の4 配電管設備の構造図		E-03

注. (1)  防火区画貫通処理（国土交通大臣認定工法）
但し、梁貫通部は、スリーブ貫通処理のこと


注. (2) 防火区画及び床貫通部は、貫通後耐火処理（大臣認定工法）の事。

注：（３） MB内の電力量計とガスの混在について
電力量計（**W**）に（**爆**）の表記のあるタイプについては全溶接した1.6 t以上の鉄箱に電力量計を収容して
防爆仕様とすること。
鉄箱のケーブル取出し口は、前後に5 cmの鋼管を取り付け口は、パテ詰めすること

注. (4) 幹線はピット内はケーブルラックW=600、セパレーター付きとし警報用の信号ケーブルと分けること

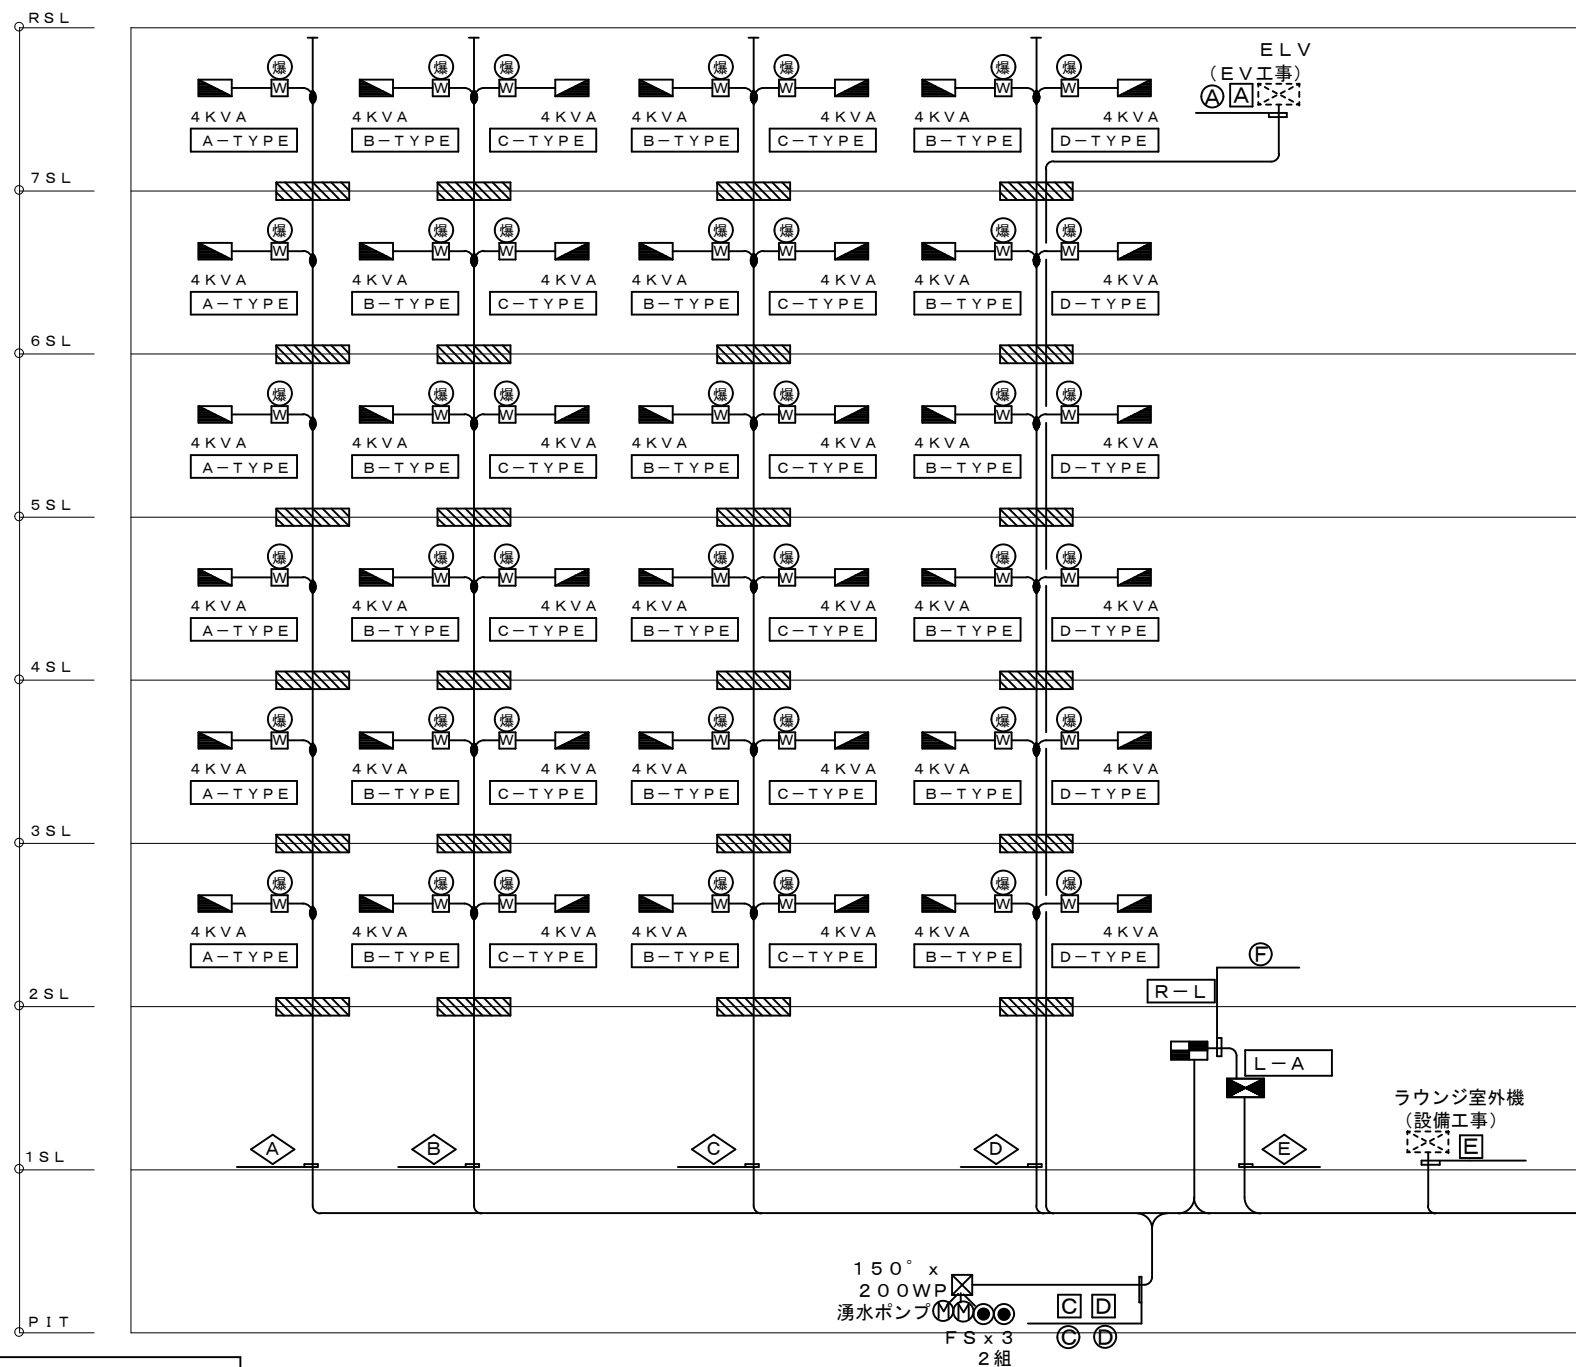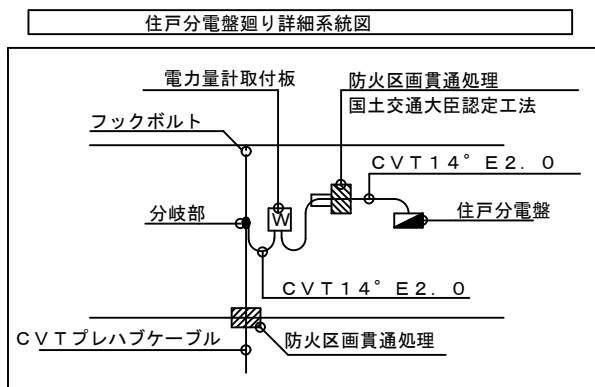

記 号	行 先	配 線 サ イ ス [*]	配管サイズ [*] (露出又は隠蔽)	配管サイズ [*] (地下シフト内)	配管サイズ [*] (地中埋設)
	J 01~LP-M	CVT 60° E 8°	(75)	メッセンジャー	FEP (80)
	J 02~LP-M	CVT 100° E 14°	(75)	メッセンジャー	FEP (80)
	J 03~LP-M	CVT 100° E 14°	(75)	メッセンジャー	FEP (80)
	J 04~LP-M	CVT 100° E 14°	(75)	メッセンジャー	FEP (80)
	L-A~LP-M	CVT 38° E 2. 0	(51)	メッセンジャー	FEP (50)
	ELV制御盤~LP-M	CVT 8° E 2. 0	PF (28)	メッセンジャー	FEP (30)
	増圧ポンプ~LP-M	CV 5. 5° -3C E 2. 0	PF (22)	メッセンジャー	FEP (30)
	湧水ポンプ~LP-M	CV 3. 5° -3C E 2. 0	PF (22)	メッセンジャー	FEP (30)
	湧水ポンプ~LP-M	CV 3. 5° -3C E 2. 0	PF (22)	メッセンジャー	FEP (30)
	ラウンジ室外機~LP-M	CV 5. 5° -3C E 2. 0	PF (22)	メッセンジャー	FEP (30)
	ラウンジ室外機~LP-M	CV 5. 5° -3C E 2. 0	PF (22)	メッセンジャー	FEP (30)
	ELV~R-L	CVV2° -3P	PF (22)	メッセンジャー	
	増圧ポンプ~R-L	CVV2° -3P	PF (22)	メッセンジャー	FEP (30)
	湧水ポンプ~R-L	CVV2° -3P x 2	PF (22)	メッセンジャー	
	湧水ポンプ~R-L	CVV2° -3P x 2	PF (22)	メッセンジャー	
	LP-M~R-L	CVV2° -10P	(51)	メッセンジャー	
	L-A~R-L	CVV2° -3P	PF (22)	メッセンジャー	

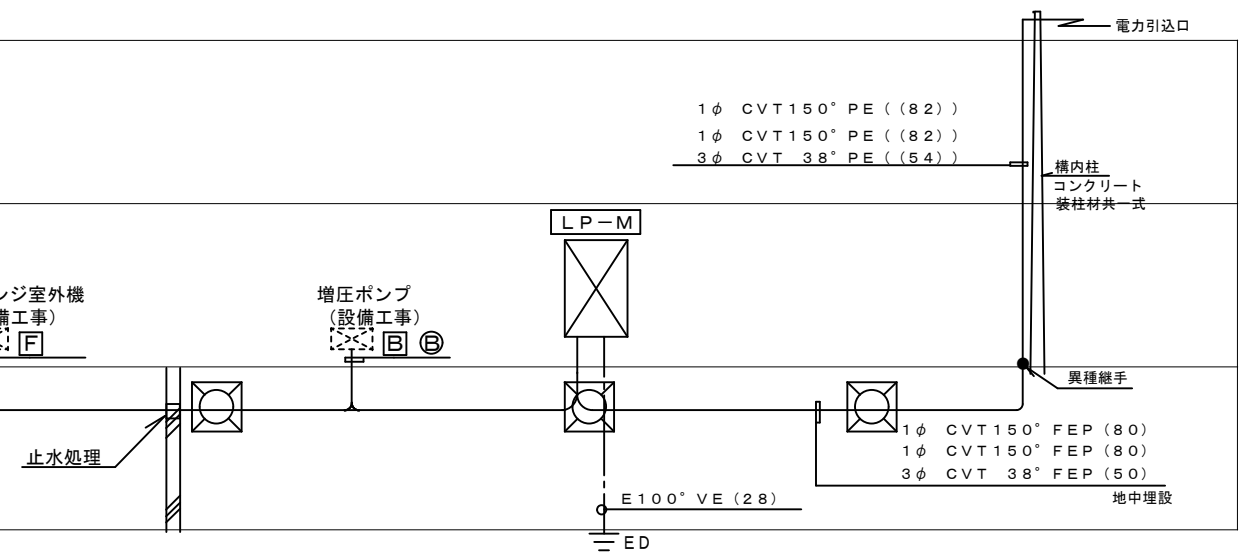


幹線設備 系統図

<table><tr><td>Date</td><td>Revision</td><td>Ck.</td></tr><tr><td></td><td></td><td></td></tr><tr><td></td><td></td><td></td></tr><tr><td></td><td></td><td></td></tr><tr><td></td><td></td><td></td></tr><tr><td></td><td></td><td></td></tr><tr><td></td><td></td><td></td></tr></table>						Date	Revision	Ck.																			<table><tr><td>Date</td><td>Revision</td><td>Ck.</td></tr><tr><td></td><td></td><td></td></tr><tr><td></td><td></td><td></td></tr><tr><td></td><td></td><td></td></tr><tr><td></td><td></td><td></td></tr><tr><td></td><td></td><td></td></tr><tr><td></td><td></td><td></td></tr></table>						Date	Revision	Ck.																			<table><tr><td>Checked</td><td>Date</td></tr><tr><td></td><td></td></tr><tr><td></td><td></td></tr><tr><td></td><td></td></tr><tr><td></td><td></td></tr><tr><td></td><td></td></tr><tr><td></td><td></td></tr></table>		Checked	Date													<table><tr><td>Drawn</td><td>Date</td></tr><tr><td></td><td></td></tr><tr><td></td><td></td></tr><tr><td></td><td></td></tr><tr><td></td><td></td></tr><tr><td></td><td></td></tr><tr><td></td><td></td></tr></table>		Drawn	Date													株式会社 小野田建築設計事務所 ARCHITECTURE & ENGINEERING Dept. 一級建築士登録第255585号 小野田 貴夫				<table><tr><td colspan="2">Project title</td></tr><tr><td colspan="2">(仮称)墨田区石原2丁目計画 新築工事</td></tr><tr><td colspan="2">Sheet content</td></tr><tr><td colspan="2">幹線動力設備 系統図</td></tr></table>				Project title		(仮称)墨田区石原2丁目計画 新築工事		Sheet content		幹線動力設備 系統図		<table><tr><td>Scale</td><td>Unit</td></tr><tr><td></td><td>MM</td></tr><tr><td colspan="2">Sheet No.</td></tr><tr><td colspan="2">E - 04</td></tr></table>		Scale	Unit		MM	Sheet No.		E - 04	
Date	Revision	Ck.	
Date	Revision	Ck.	
Checked	Date	
Drawn	Date	
Project title	
(仮称)墨田区石原2丁目計画 新築工事	
Sheet content	
幹線動力設備 系統図	
Scale	Unit	
	MM	
Sheet No.	
E - 04	


注記 1 特記なき配管配線は下記に依る事

- 電話
- 電話
- 電話
- 電話
- 電話
- 電話
- PVC0. 65-1P x 1CD (16)
- PVC0. 65-1P x 1CD (16)
- PVC0. 65-1P x 2CD (16)
- PVC0. 65-1P x 2CD (16)
- CD (16)
- " (16)

- 2 配管施工後、呼線挿入の事
- 3 電話用モジュージャック 6極2芯用 x 2 埋込型
- 4 引込に当たりNTTと事前に協議を行う事。
- 5 MDF以降住戸内アウトレットまでの配管配線及び整端は、電気工事とする。 又、NTTと事前に協議を行う事。
- 6 MDF内ジャンパー線の結線を施す事。

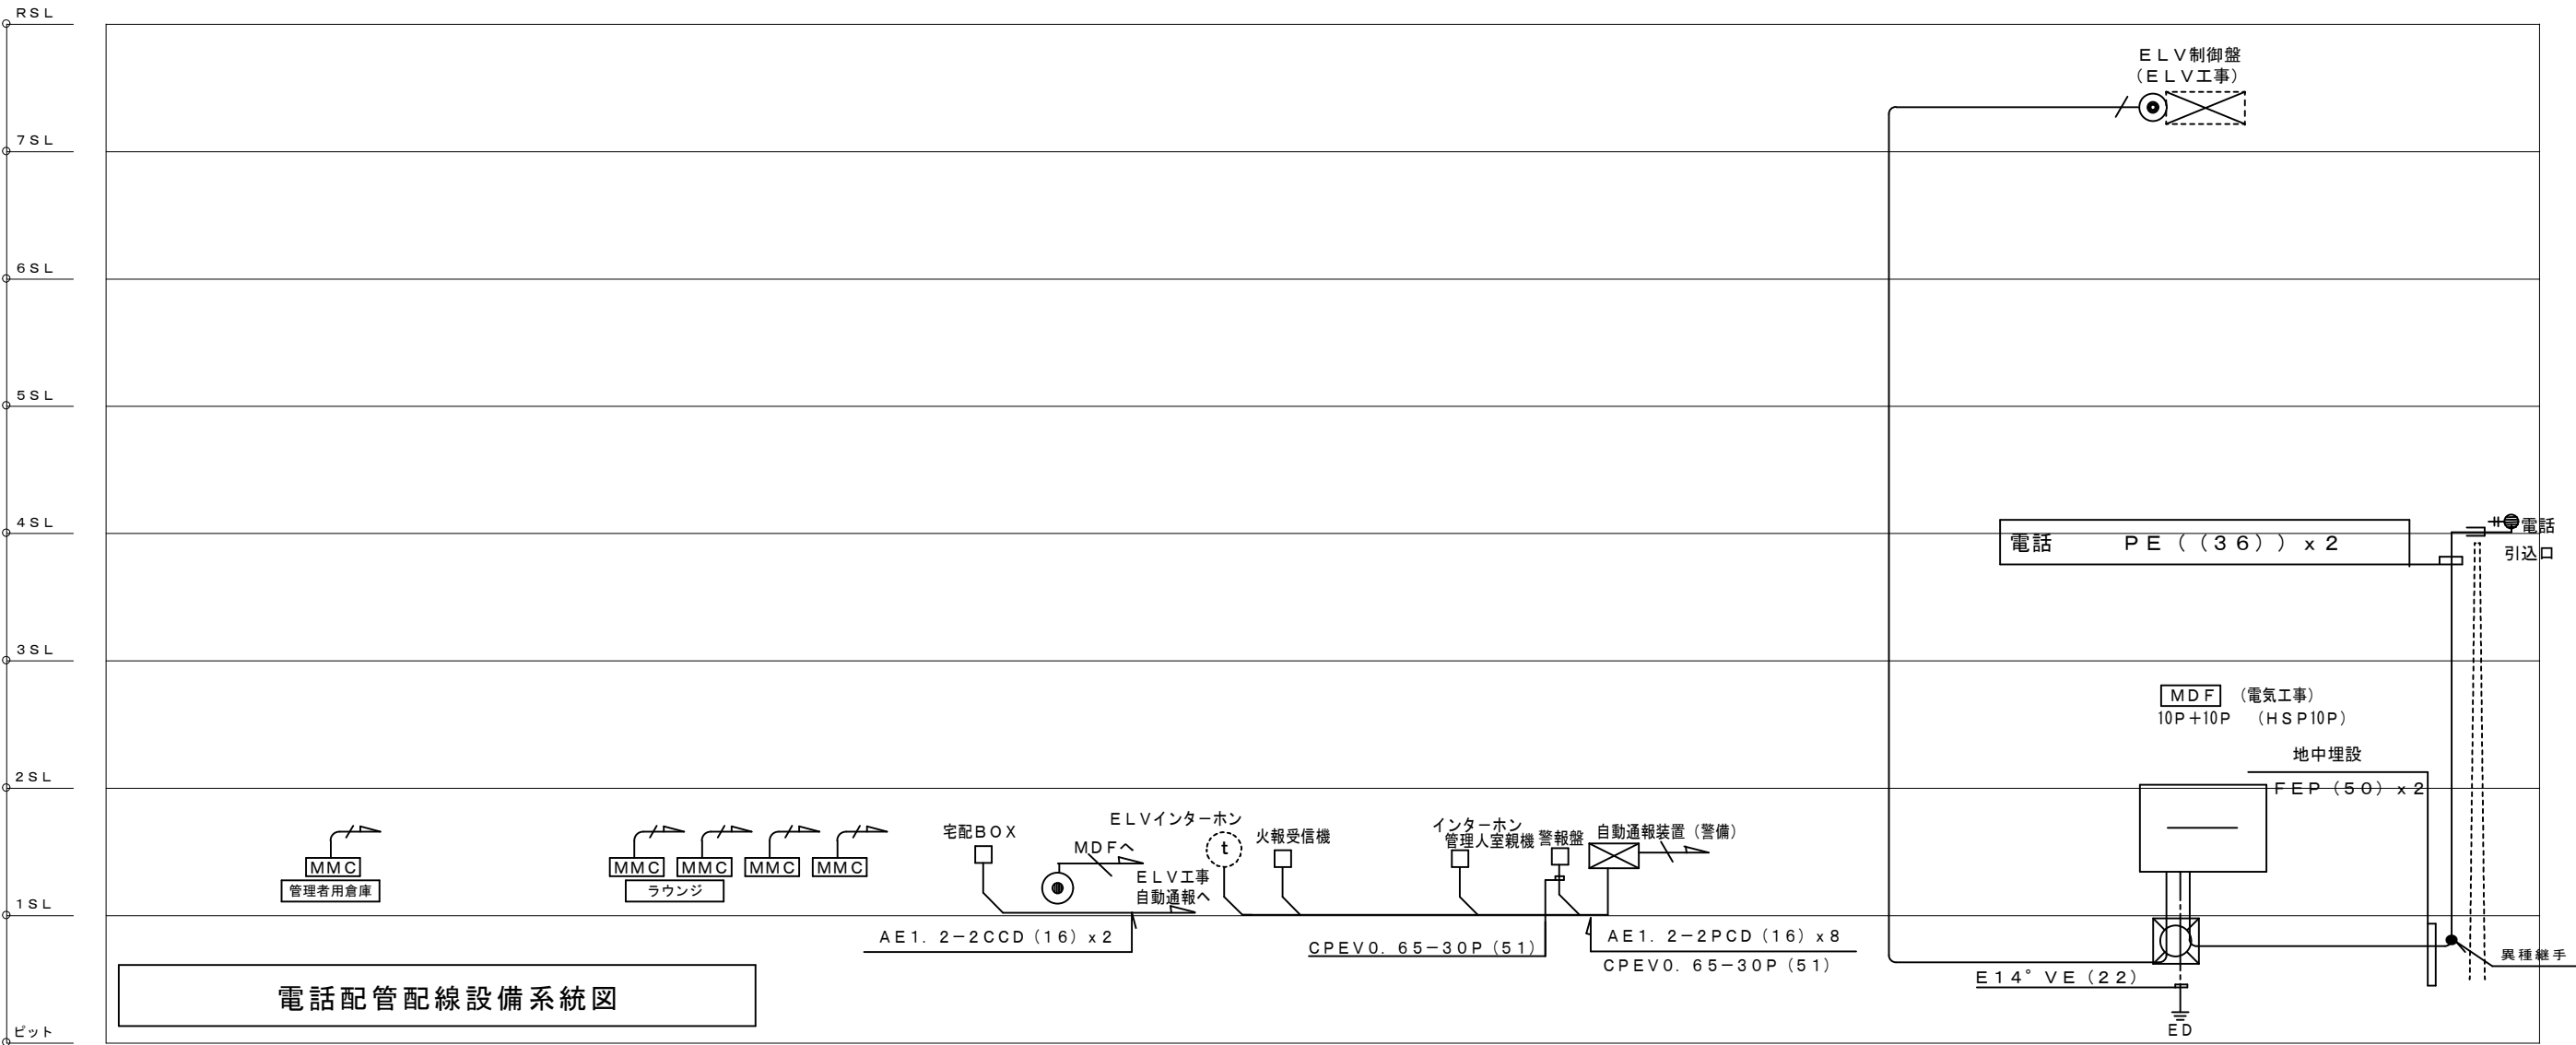

Date	Revision	Ck.	Date	Revision	Ck.	Checked	Date	Drawn	Date	Project title	Scale	Unit
										(仮称) 墨田区石原2丁目計画 新築工事		MM
										Sheet content		Sheet No.
										電話配管配線設備 系統図		E - 0 6

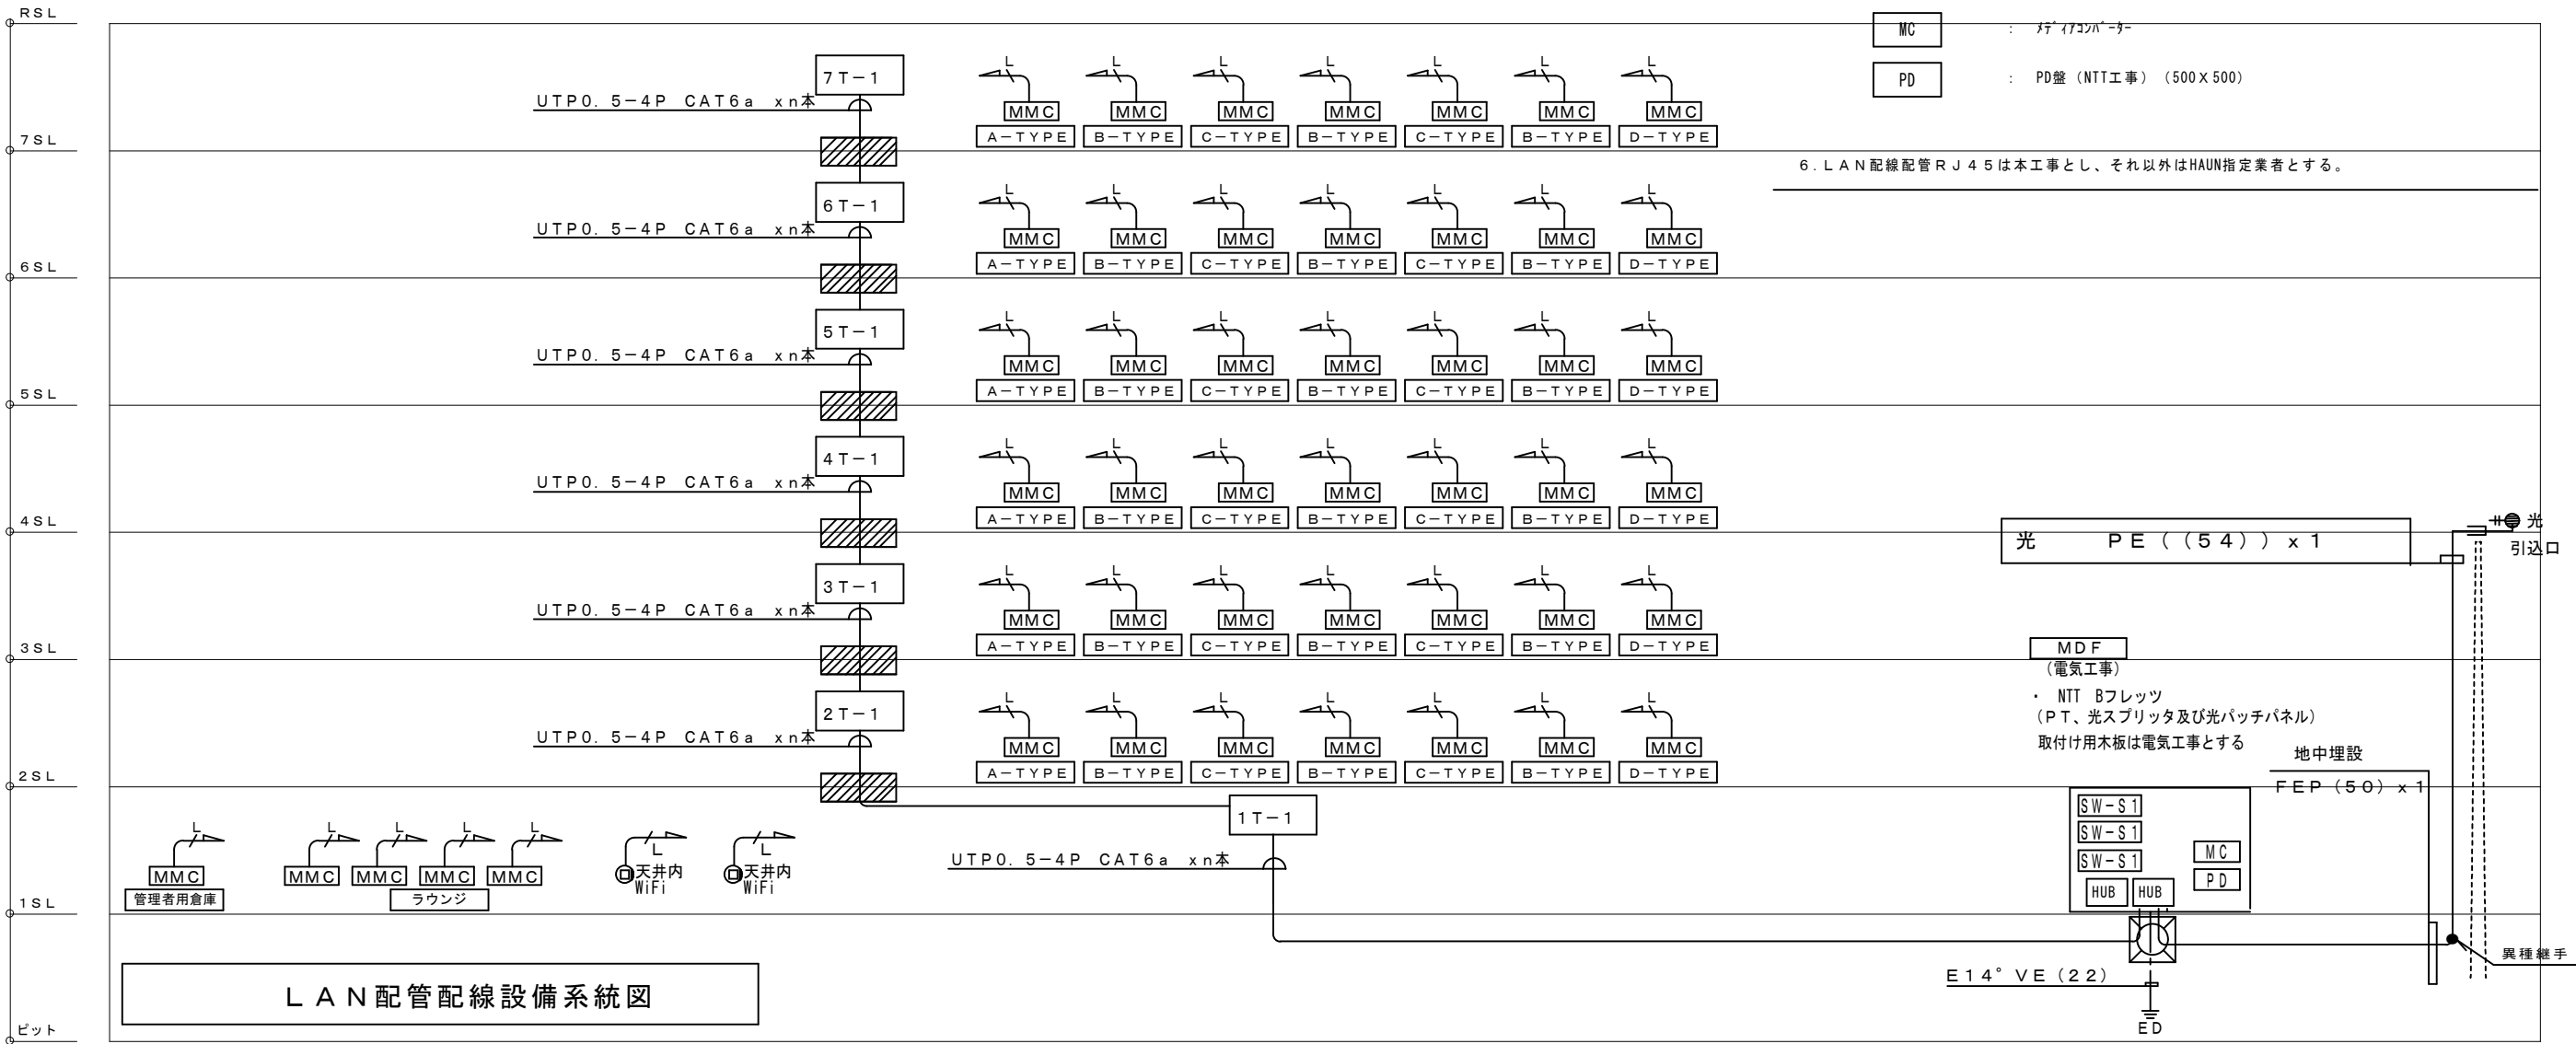

- 注記
- 防火区画貫通部は、国土交通大臣認定工法(1時間耐火)にて防火区画貫通処理を行うこと。
 - 防火区画を貫通する配線は、金属管にて保護をする。
 - 壁を立上げ・引下げする配線は、PF管にて保護をする。
 - 特記なき配管配線は下記とする。
- Cat6a UTP0.5-4P (PF22)
- 導入線1.2mm (PF22)
- (E25) 導入線1.2mm (E25)
5. 凡例
- MMC : LAN7ポート (モジュラージャック8極8芯) (コンセント一体ポート)
- HUB : 住宅情報機器群
- SW-S1 : スイッチングハブ (24ポート)
- MC : デバイスコンバーター
- PD : PD盤 (NTT工事) (500x500)
6. LAN配線配管RJ45は本工事とし、それ以外はHAUN指定業者とする。

Date	Revision	Ck.	Date	Revision	Ck.	Checked	Date	Drawn	Date	Project title	Scale	Unit
										(仮称) 墨田区石原2丁目計画 新築工事		MM
										Sheet content		Sheet No.
										L A N設備 系統図		E - 0 7

株式会社 小野田建築設計事務所

ARCHITECTURE & ENGINEERING Dept.
一級建築士登録第255585号 小野田 貴夫

注記 1. テレビ機器は下記による。

UV/BSCS110

 2 分配器 (双方向)

3 分配器 (双方向)

 4 分配器 (双方向)

 6分配器（双方向）

1 分岐器 (双方向)

◎ 端末ユニット（2端子・F型接栓付き
・ハイパスフィルタ内蔵及び切替SW付）

TVブースター用コンセント
露出形2P15A×2 ET付

2. 特記なき配線は下記とする。

_____ S-5C-FBCD (16)

—C— CD (22)


~~7C~~ S-7C-FBCD (22)

3. EPS内、MDF付近に全体の系統図をプラスチックケースに収めて設置する事



4. 増幅器、分配器、分岐器の同軸ケーブルは行き先表示の名札を取り付けること。

5. 区画貫通部は大臣認定工法によること

6. TV機器は10MHz～3224MHzとする。

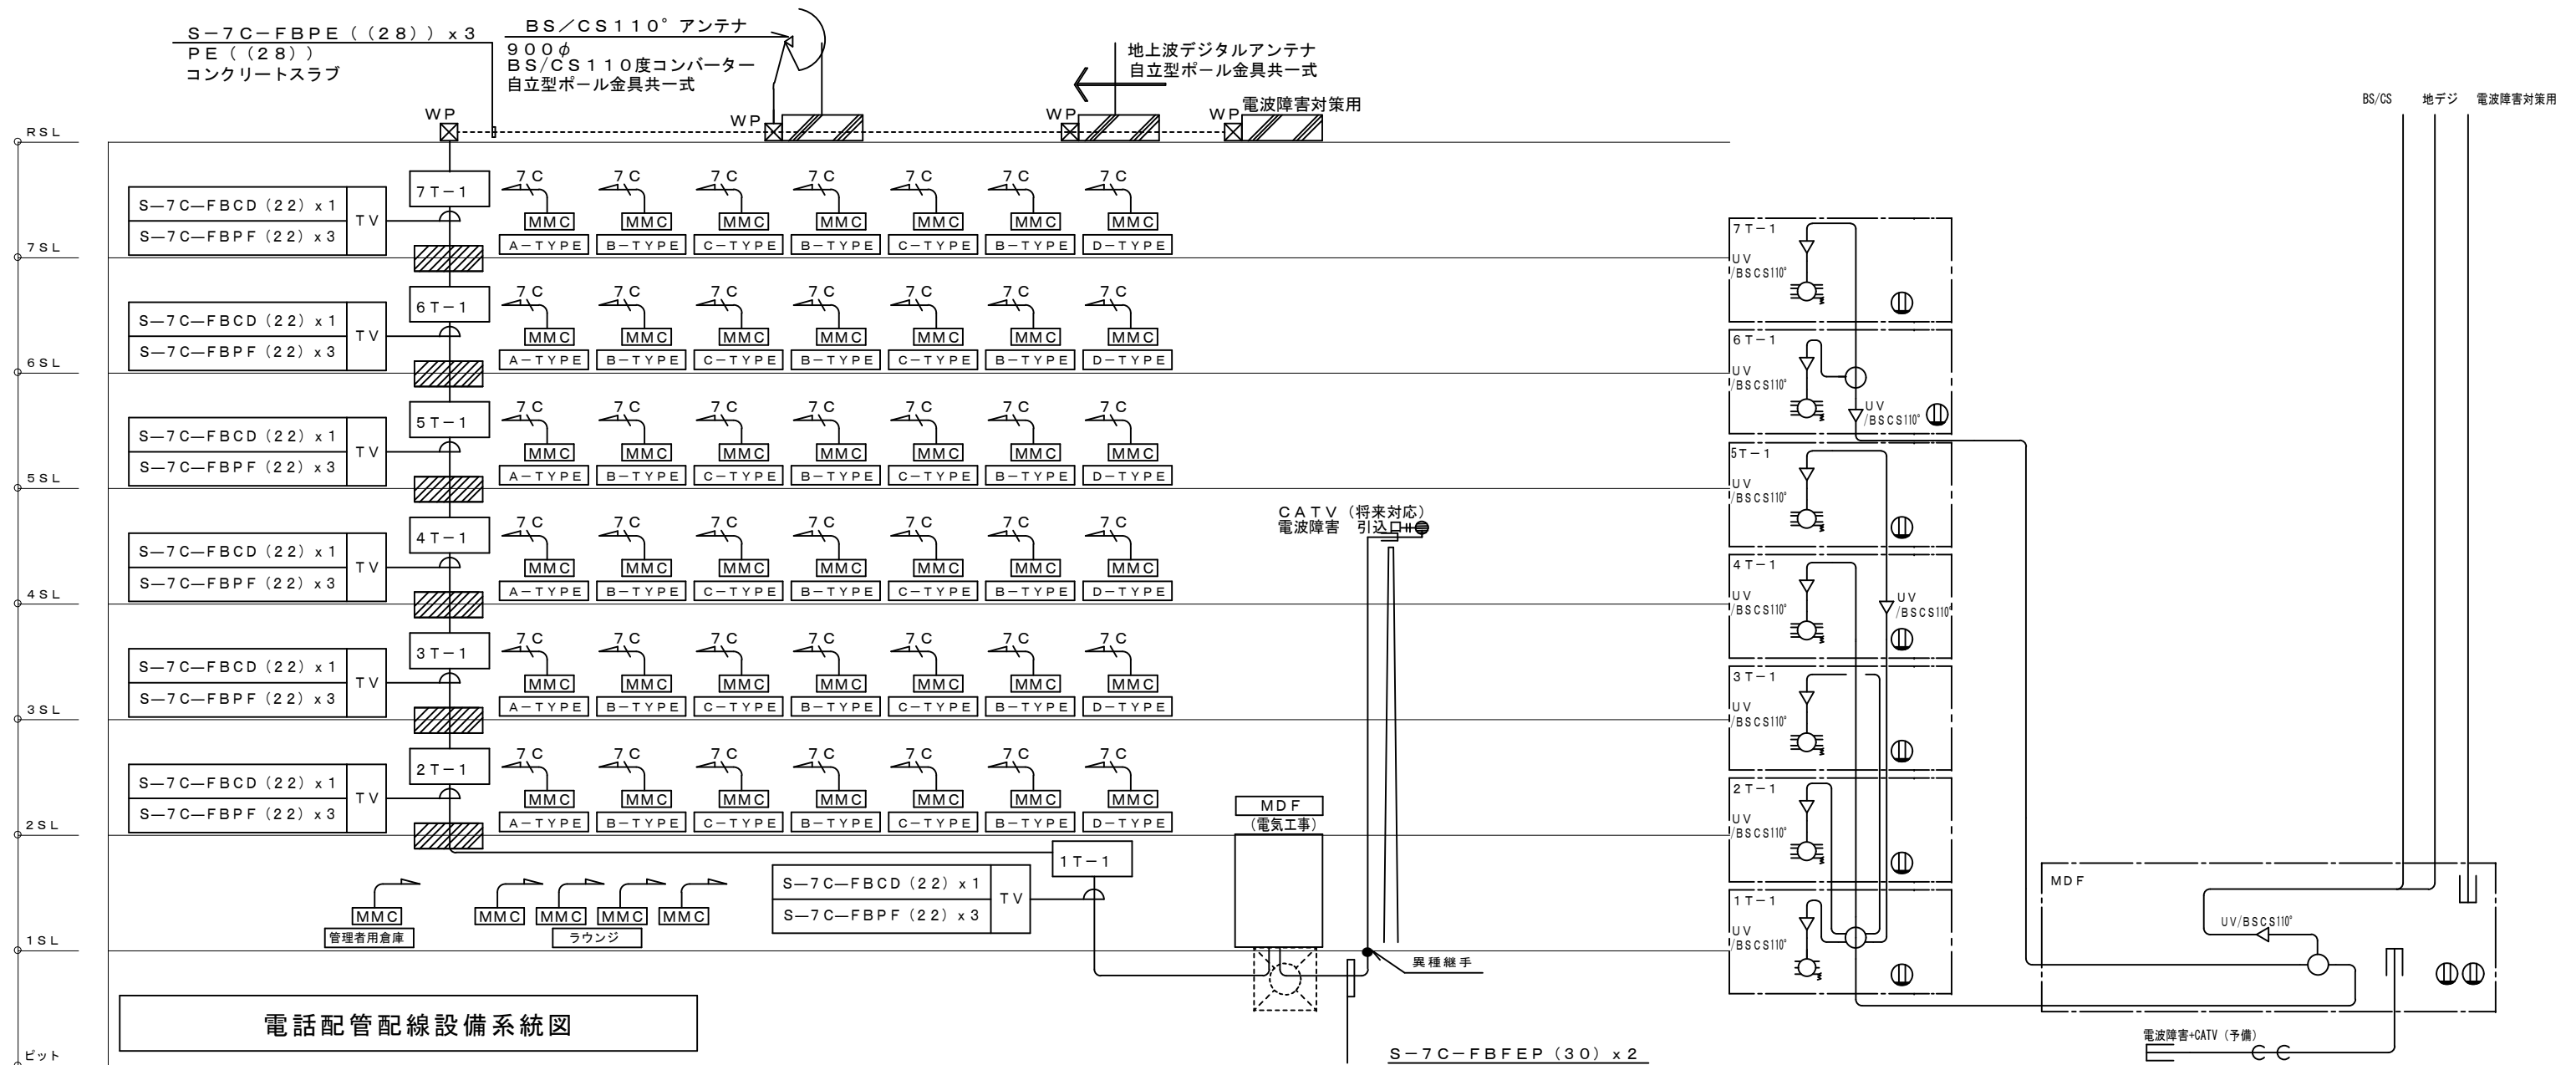


Date Revision Ck.			Date Revision Ck.			Checked Date		Drawn Date		株式会社 小野田建築設計事務所 ARCHITECTURE & ENGINEERING Dept. 一級建築士登録第255585号 小野田 貴夫		Project title		Scale Unit	
												(仮称) 墨田区石原2丁目計画 新築工事		MM	
												Sheet content		Sheet No.	
												テレビ共同視聴設備 系統図		E - 08	

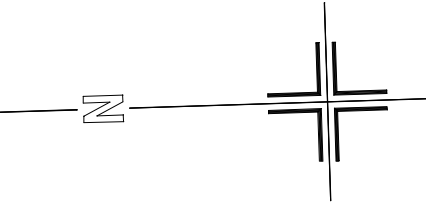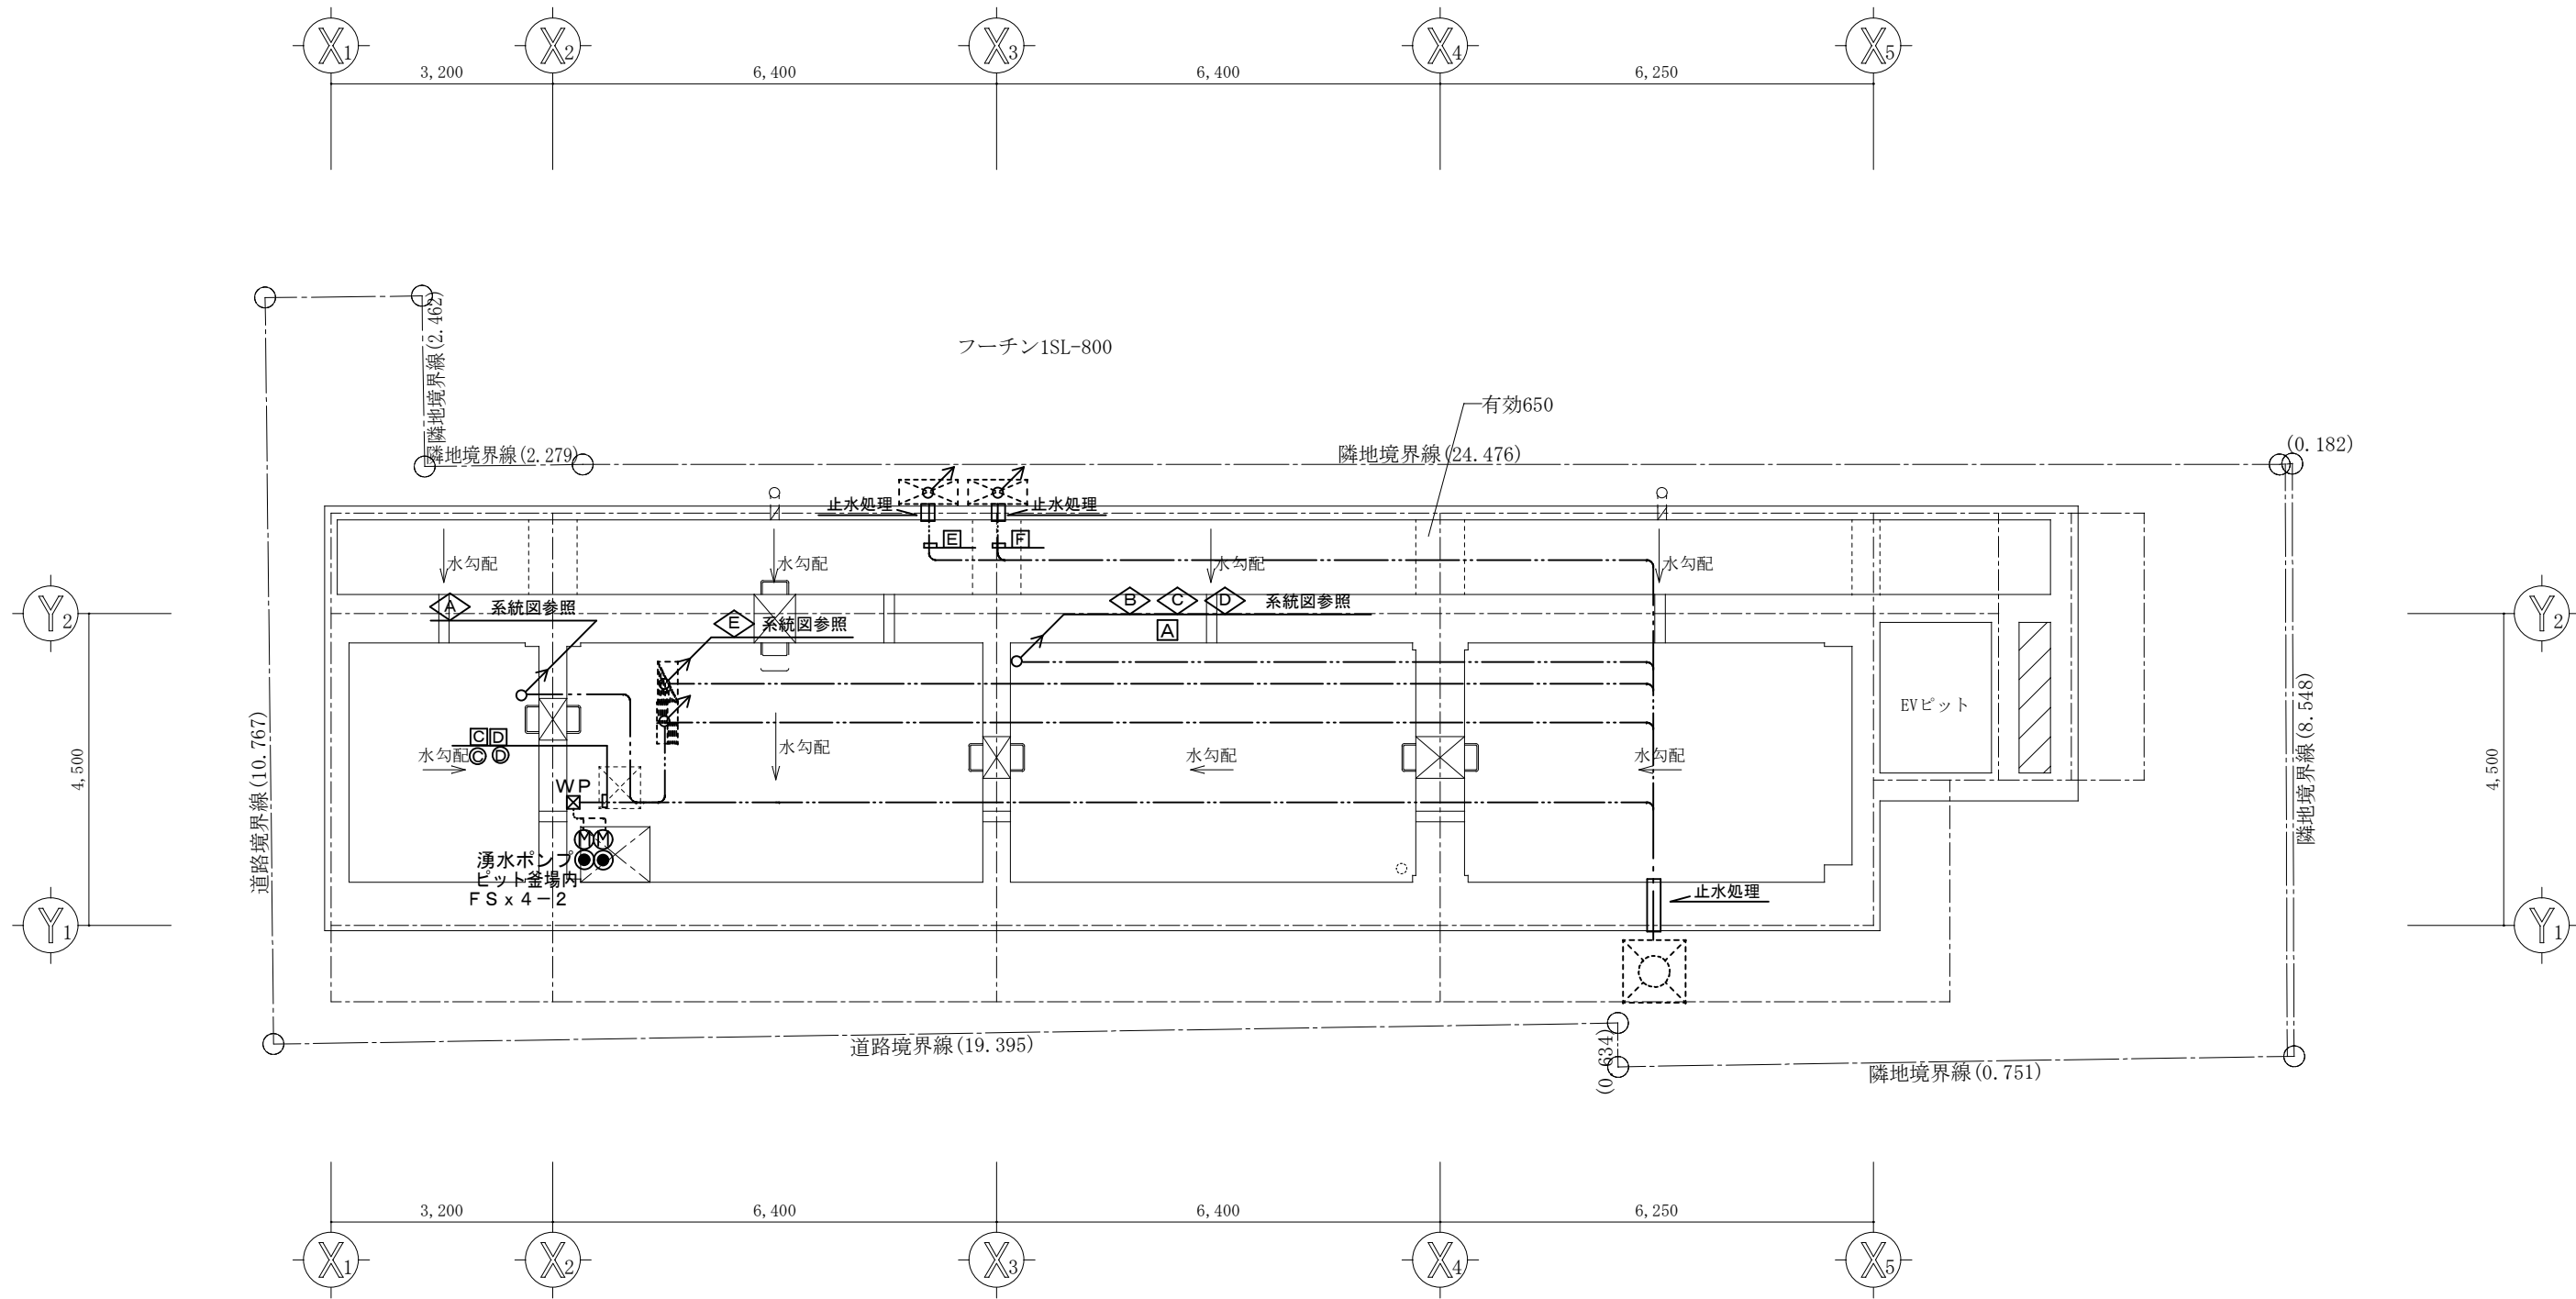


確認 E-03

Date			Revision			Checked	Date	Drawn	Date	Project title		Scale		Unit	
Date	Revision	Ck.	Date	Revision	Ck.					Sheet content		Sheet No.		E-09	
										株式会社 小野田建築設計事務所		(仮称) 墨田区石原2丁目計画 新築工事		1/100	
										ARCHITECTURE & ENGINEERING Dept.					
										一級建築士登録第255585号 小野田 貴夫					
										幹線動力設備 地下ピット図					


準工業地域
容積率300%・建ぺい率60%
日影規制：なし
準防火地域・22m高度地区

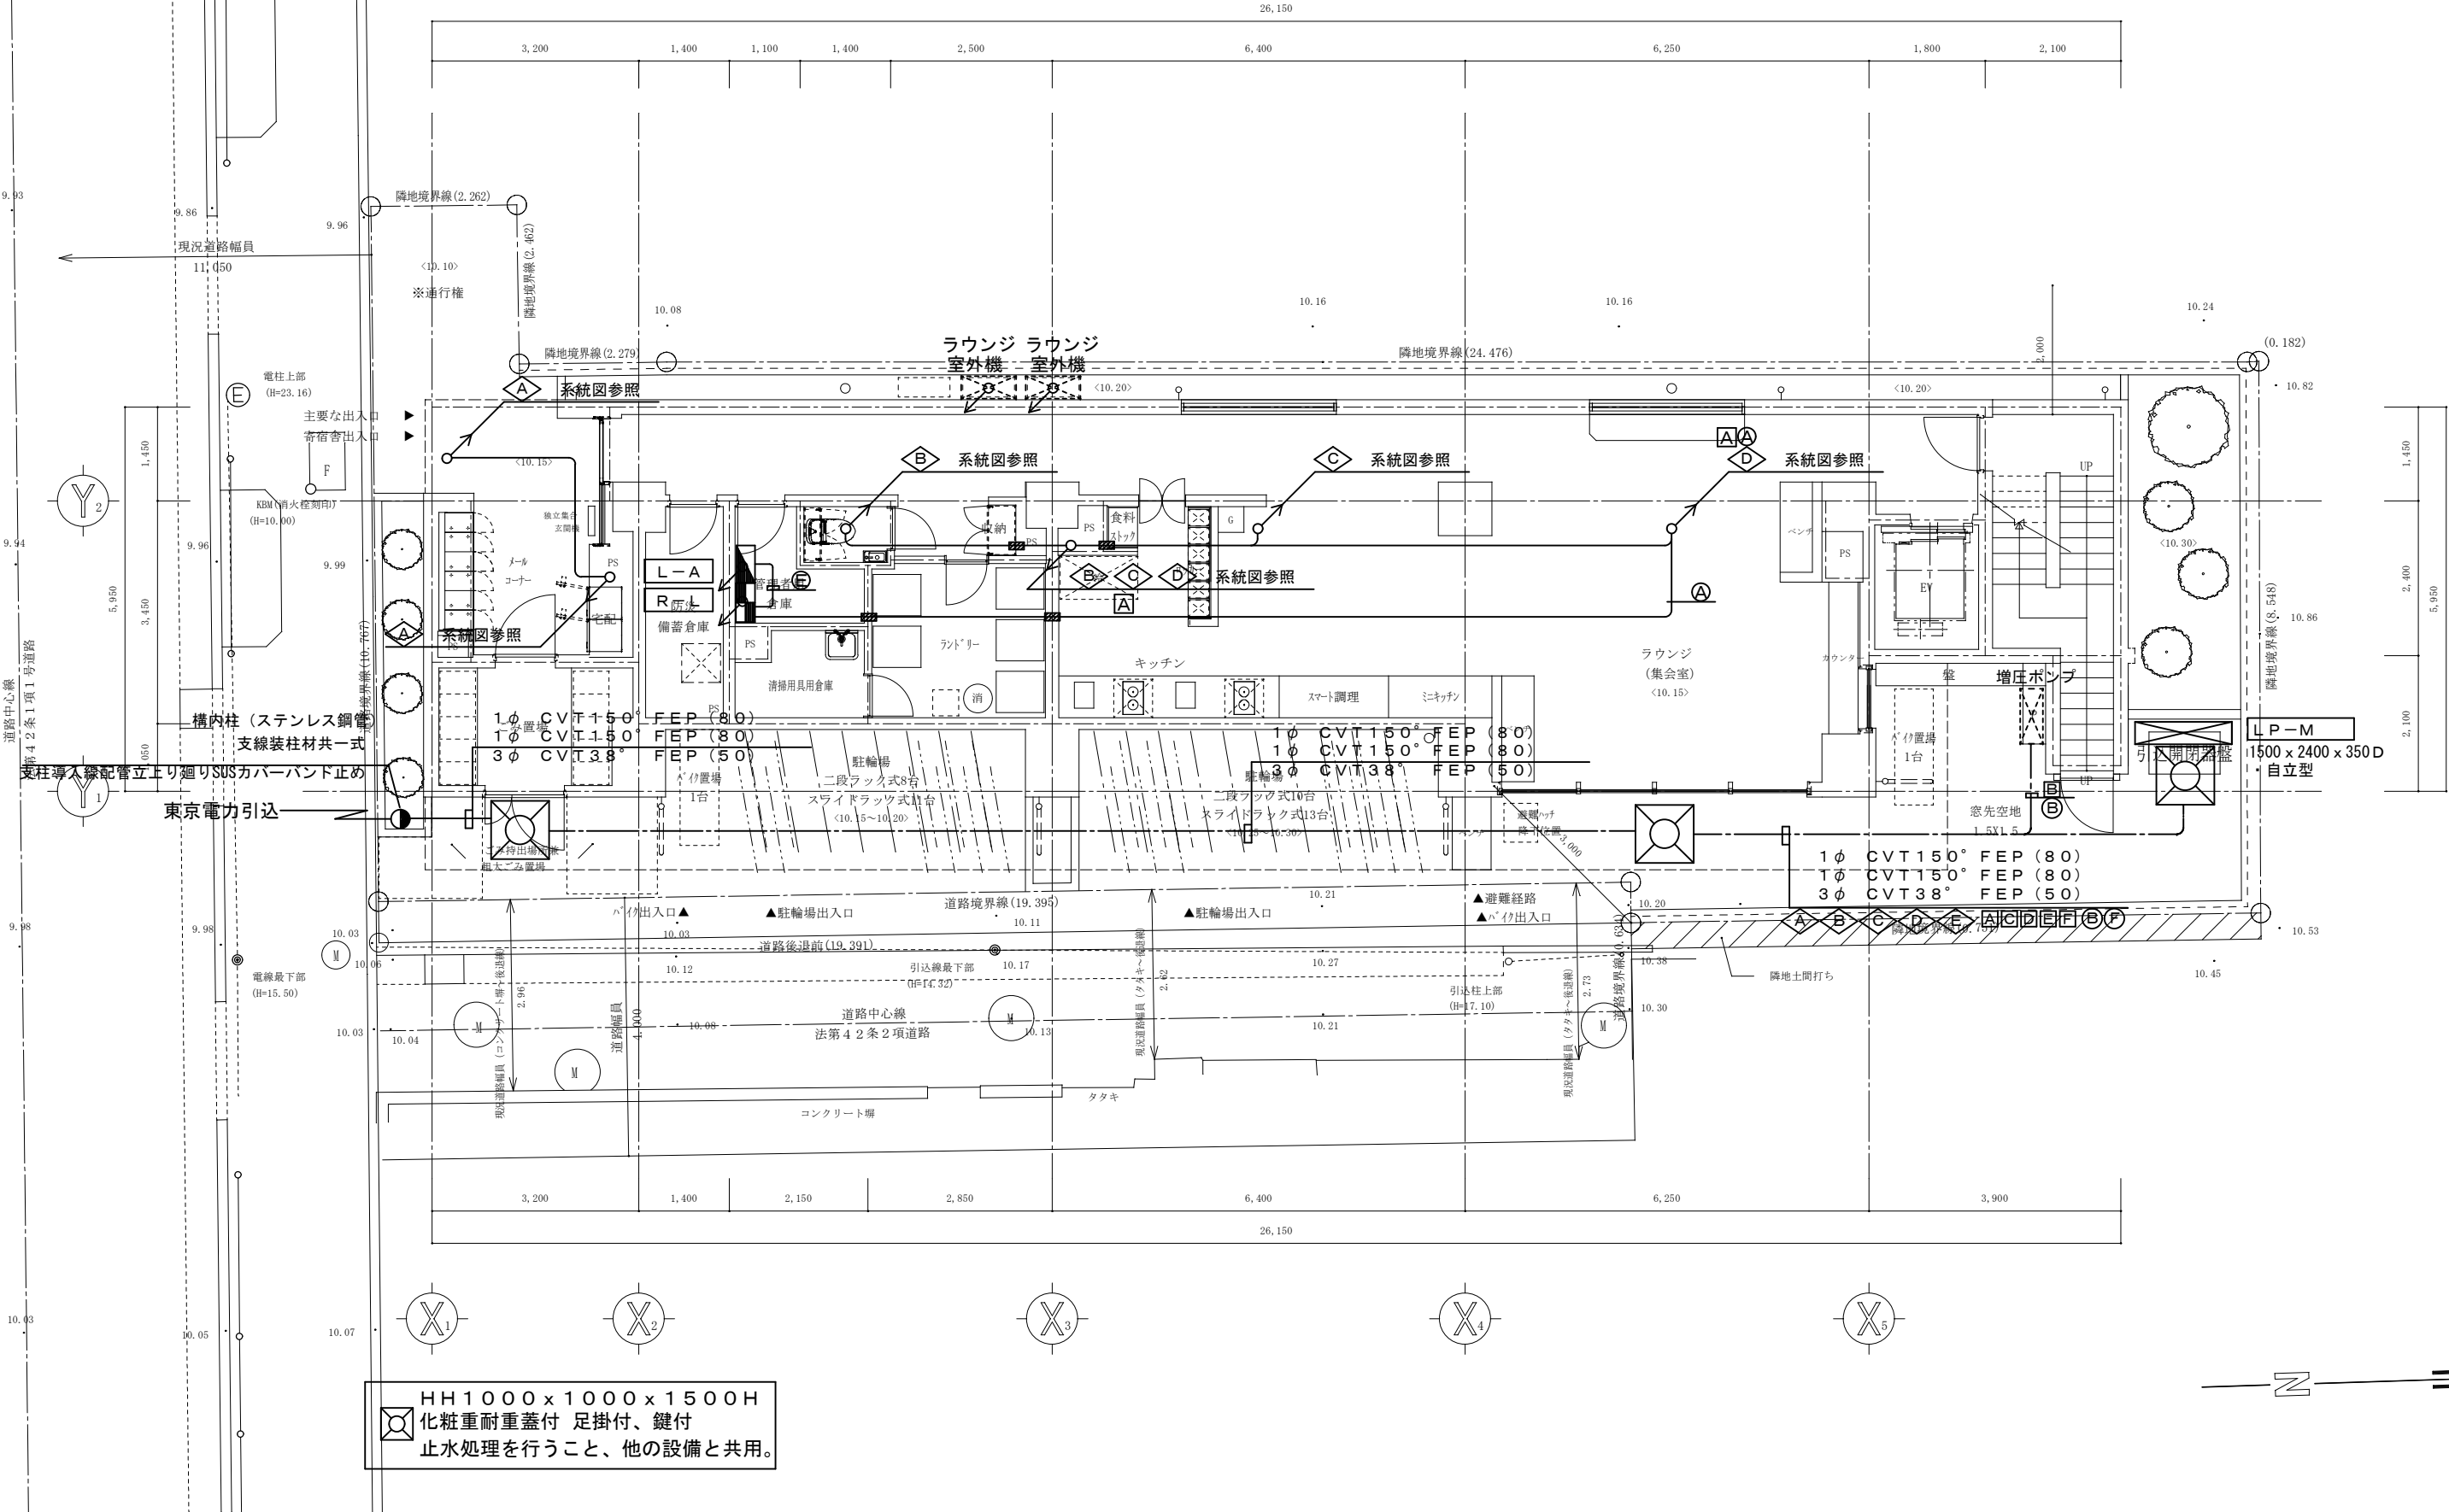

Date			Revision			Ck.	Date			Revision			Ck.	Checked	Date	Drawn	Date	株式会社 小野田 建築設計事務所 ARCHITECTURE & ENGINEERING Dept. 一級建築士登録第755585号 小野田 貴夫			Project title			Scale			Unit		
																					(仮称) 墨田区石原2丁目計画 新築工事			1/100			MM		
																					Sheet content			Sheet No.					
																					幹線動力設備 平面図 (1)			E - 10					

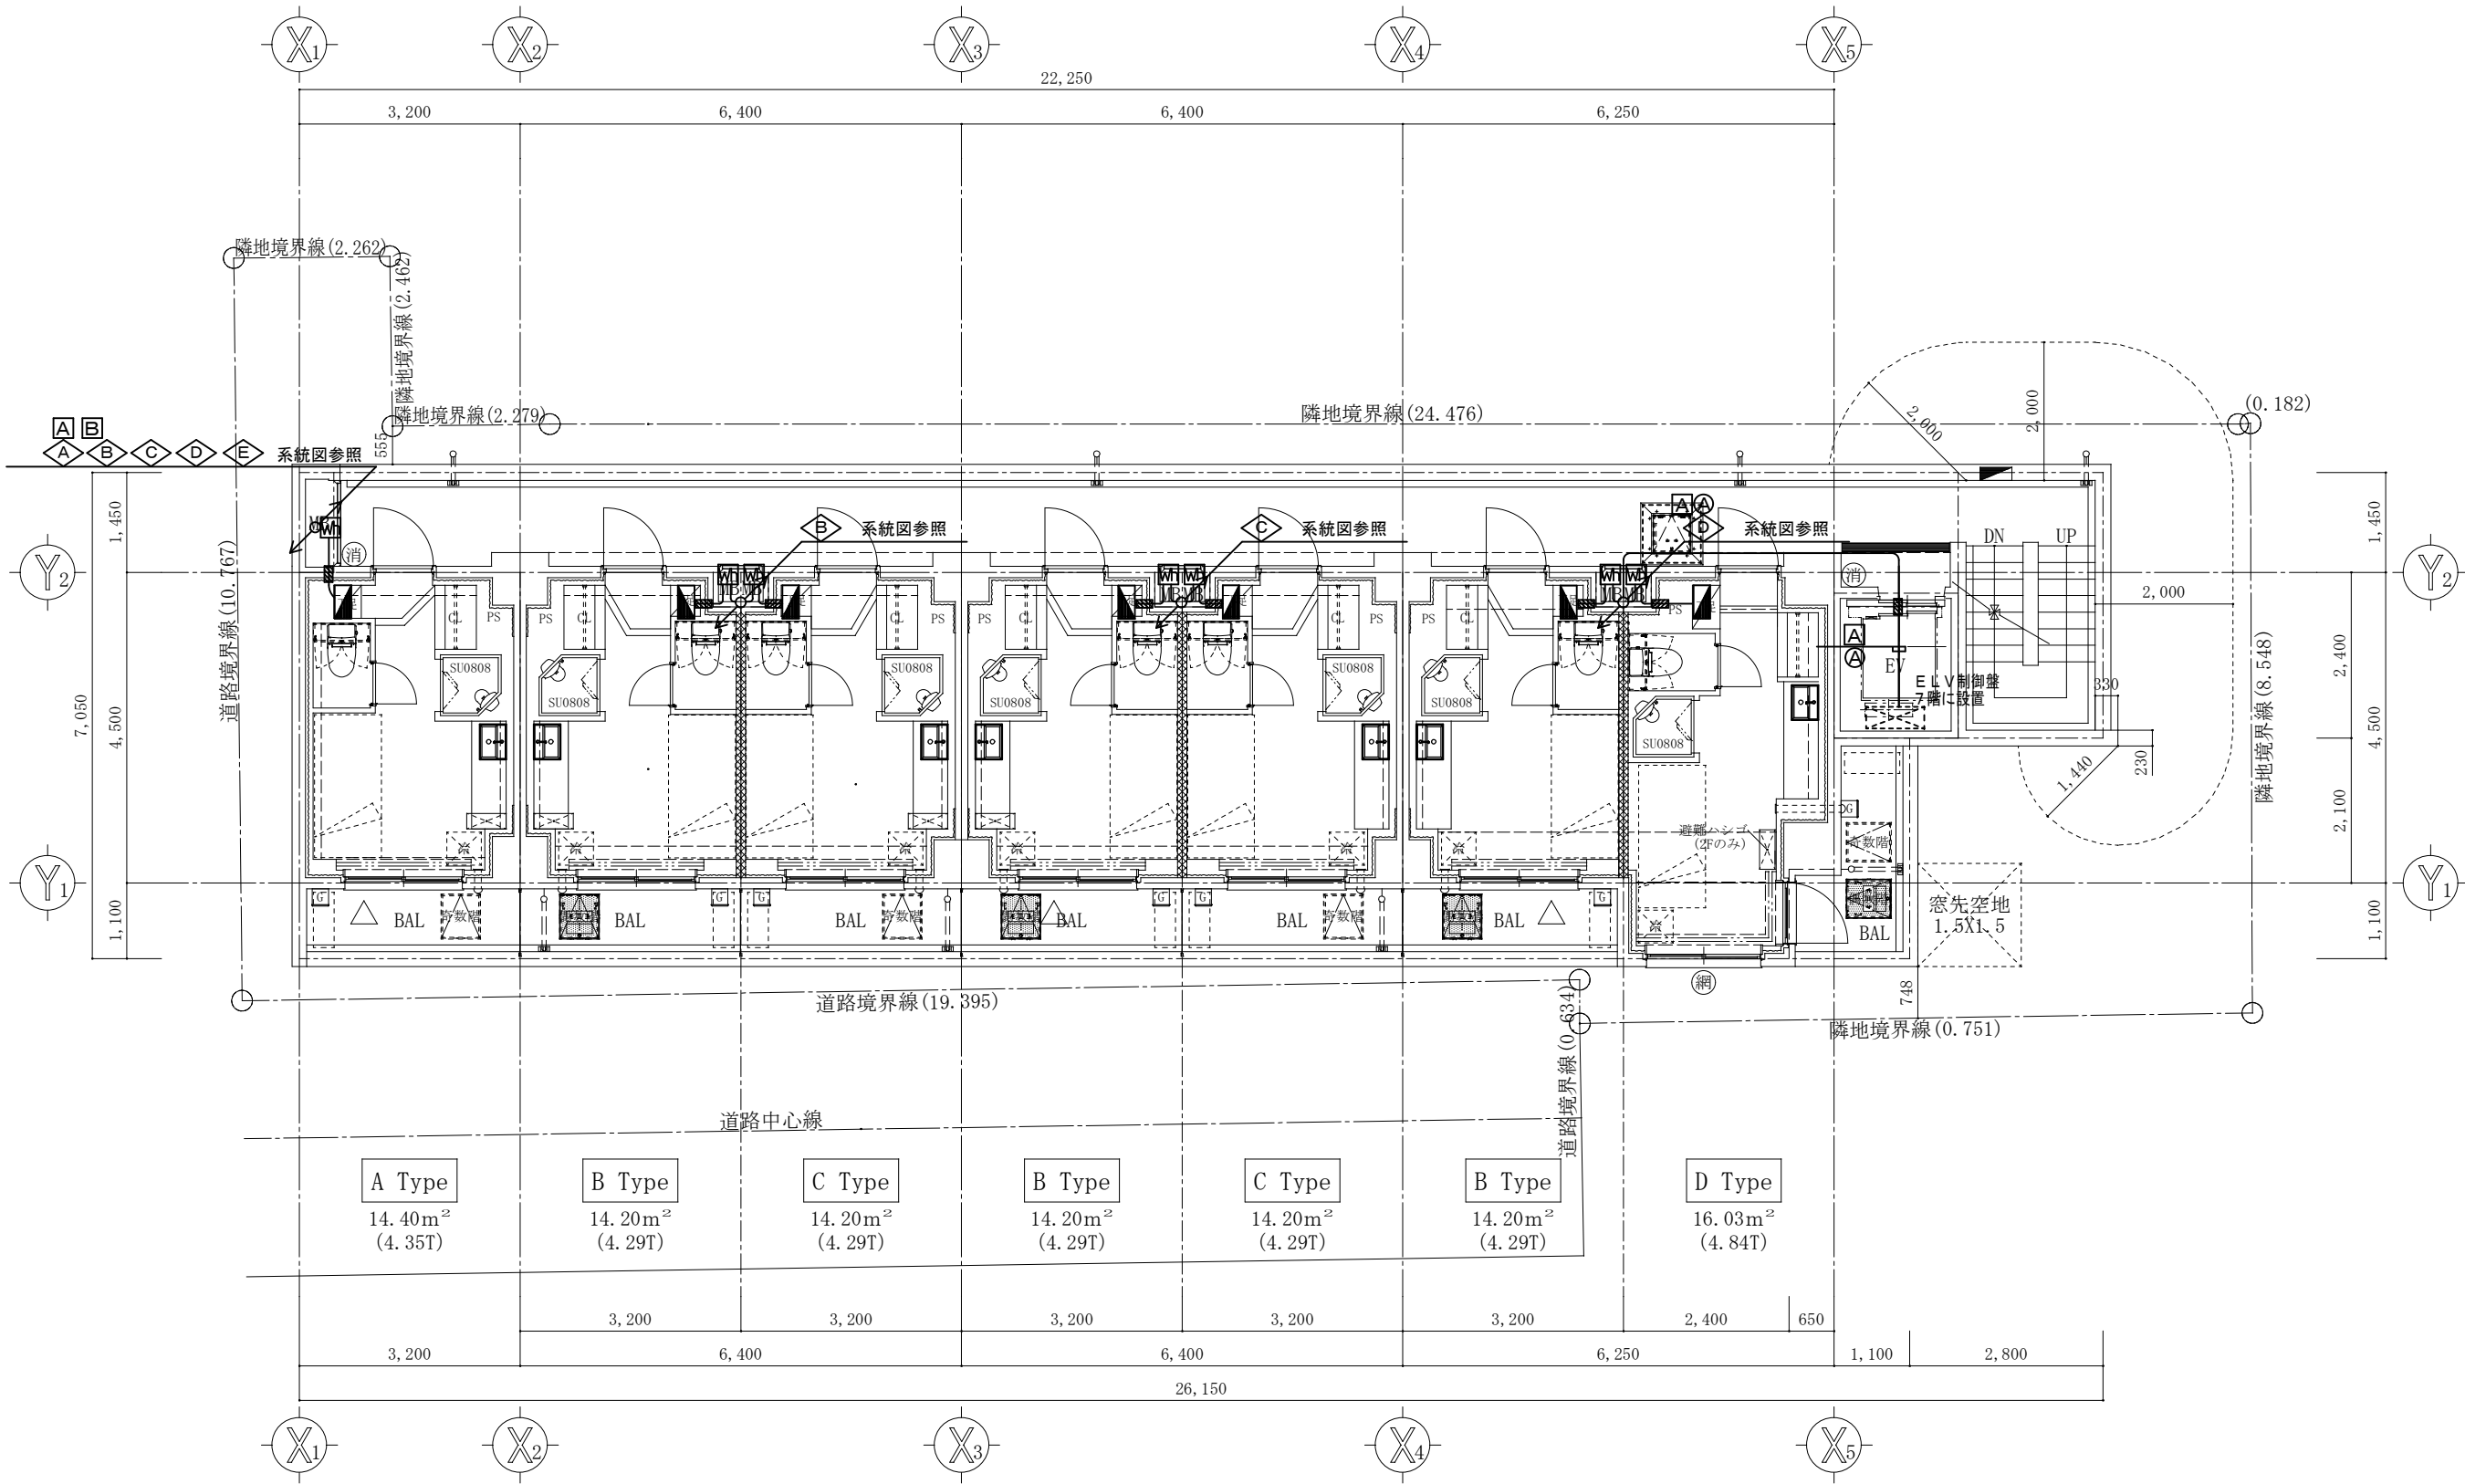


2 ～ 7 階平面図

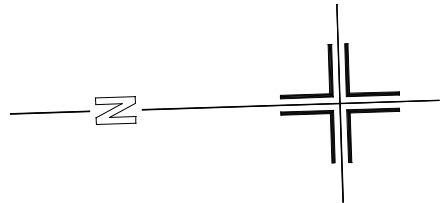


確認 E-05

DateRevisionCk.			DateRevisionCk.			CheckedDate	DrawnDate	株式会社 小野田 建築設計事務所 ARCHITECTURE & ENGINEERING Dept. 一級建築士登録第255585号 小野田 貴夫	Project title		ScaleUnit
									(仮称) 墨田区石原2丁目計画 新築工事		1/100MM
									Sheet content		Sheet No.
									幹線動力設備 平面図 (2)		E - 1 1

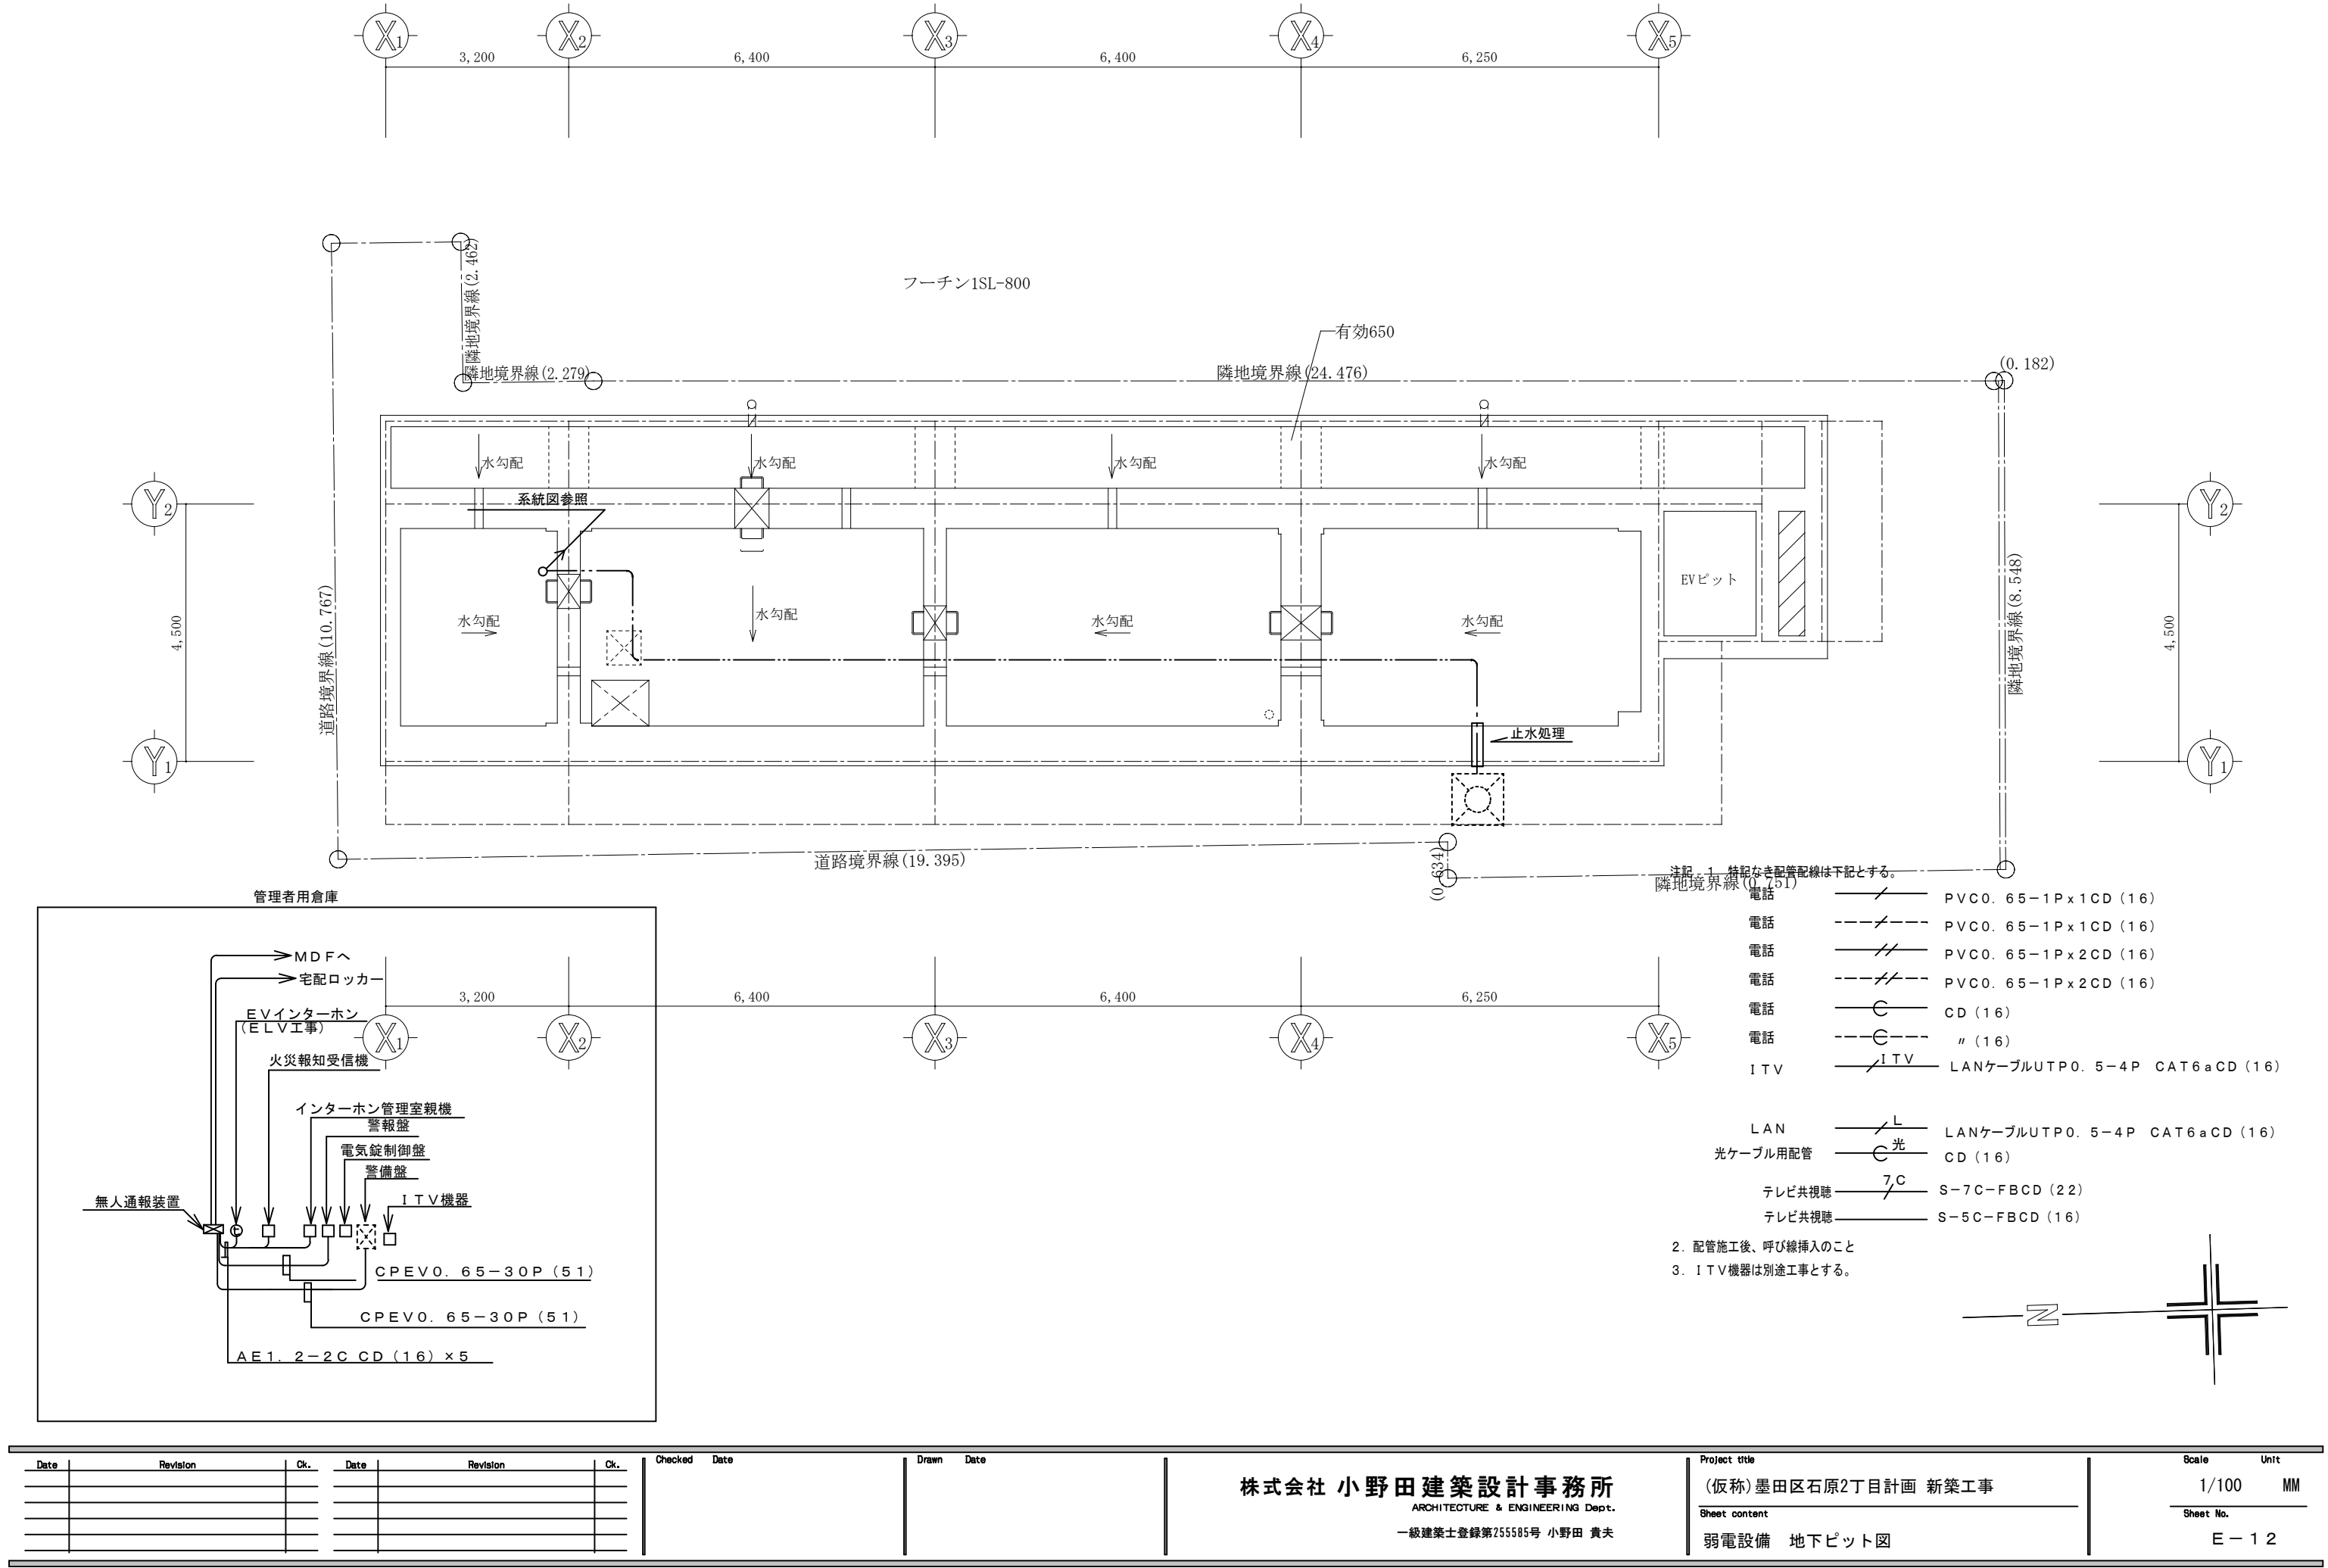


準防火地域・22m高度地区



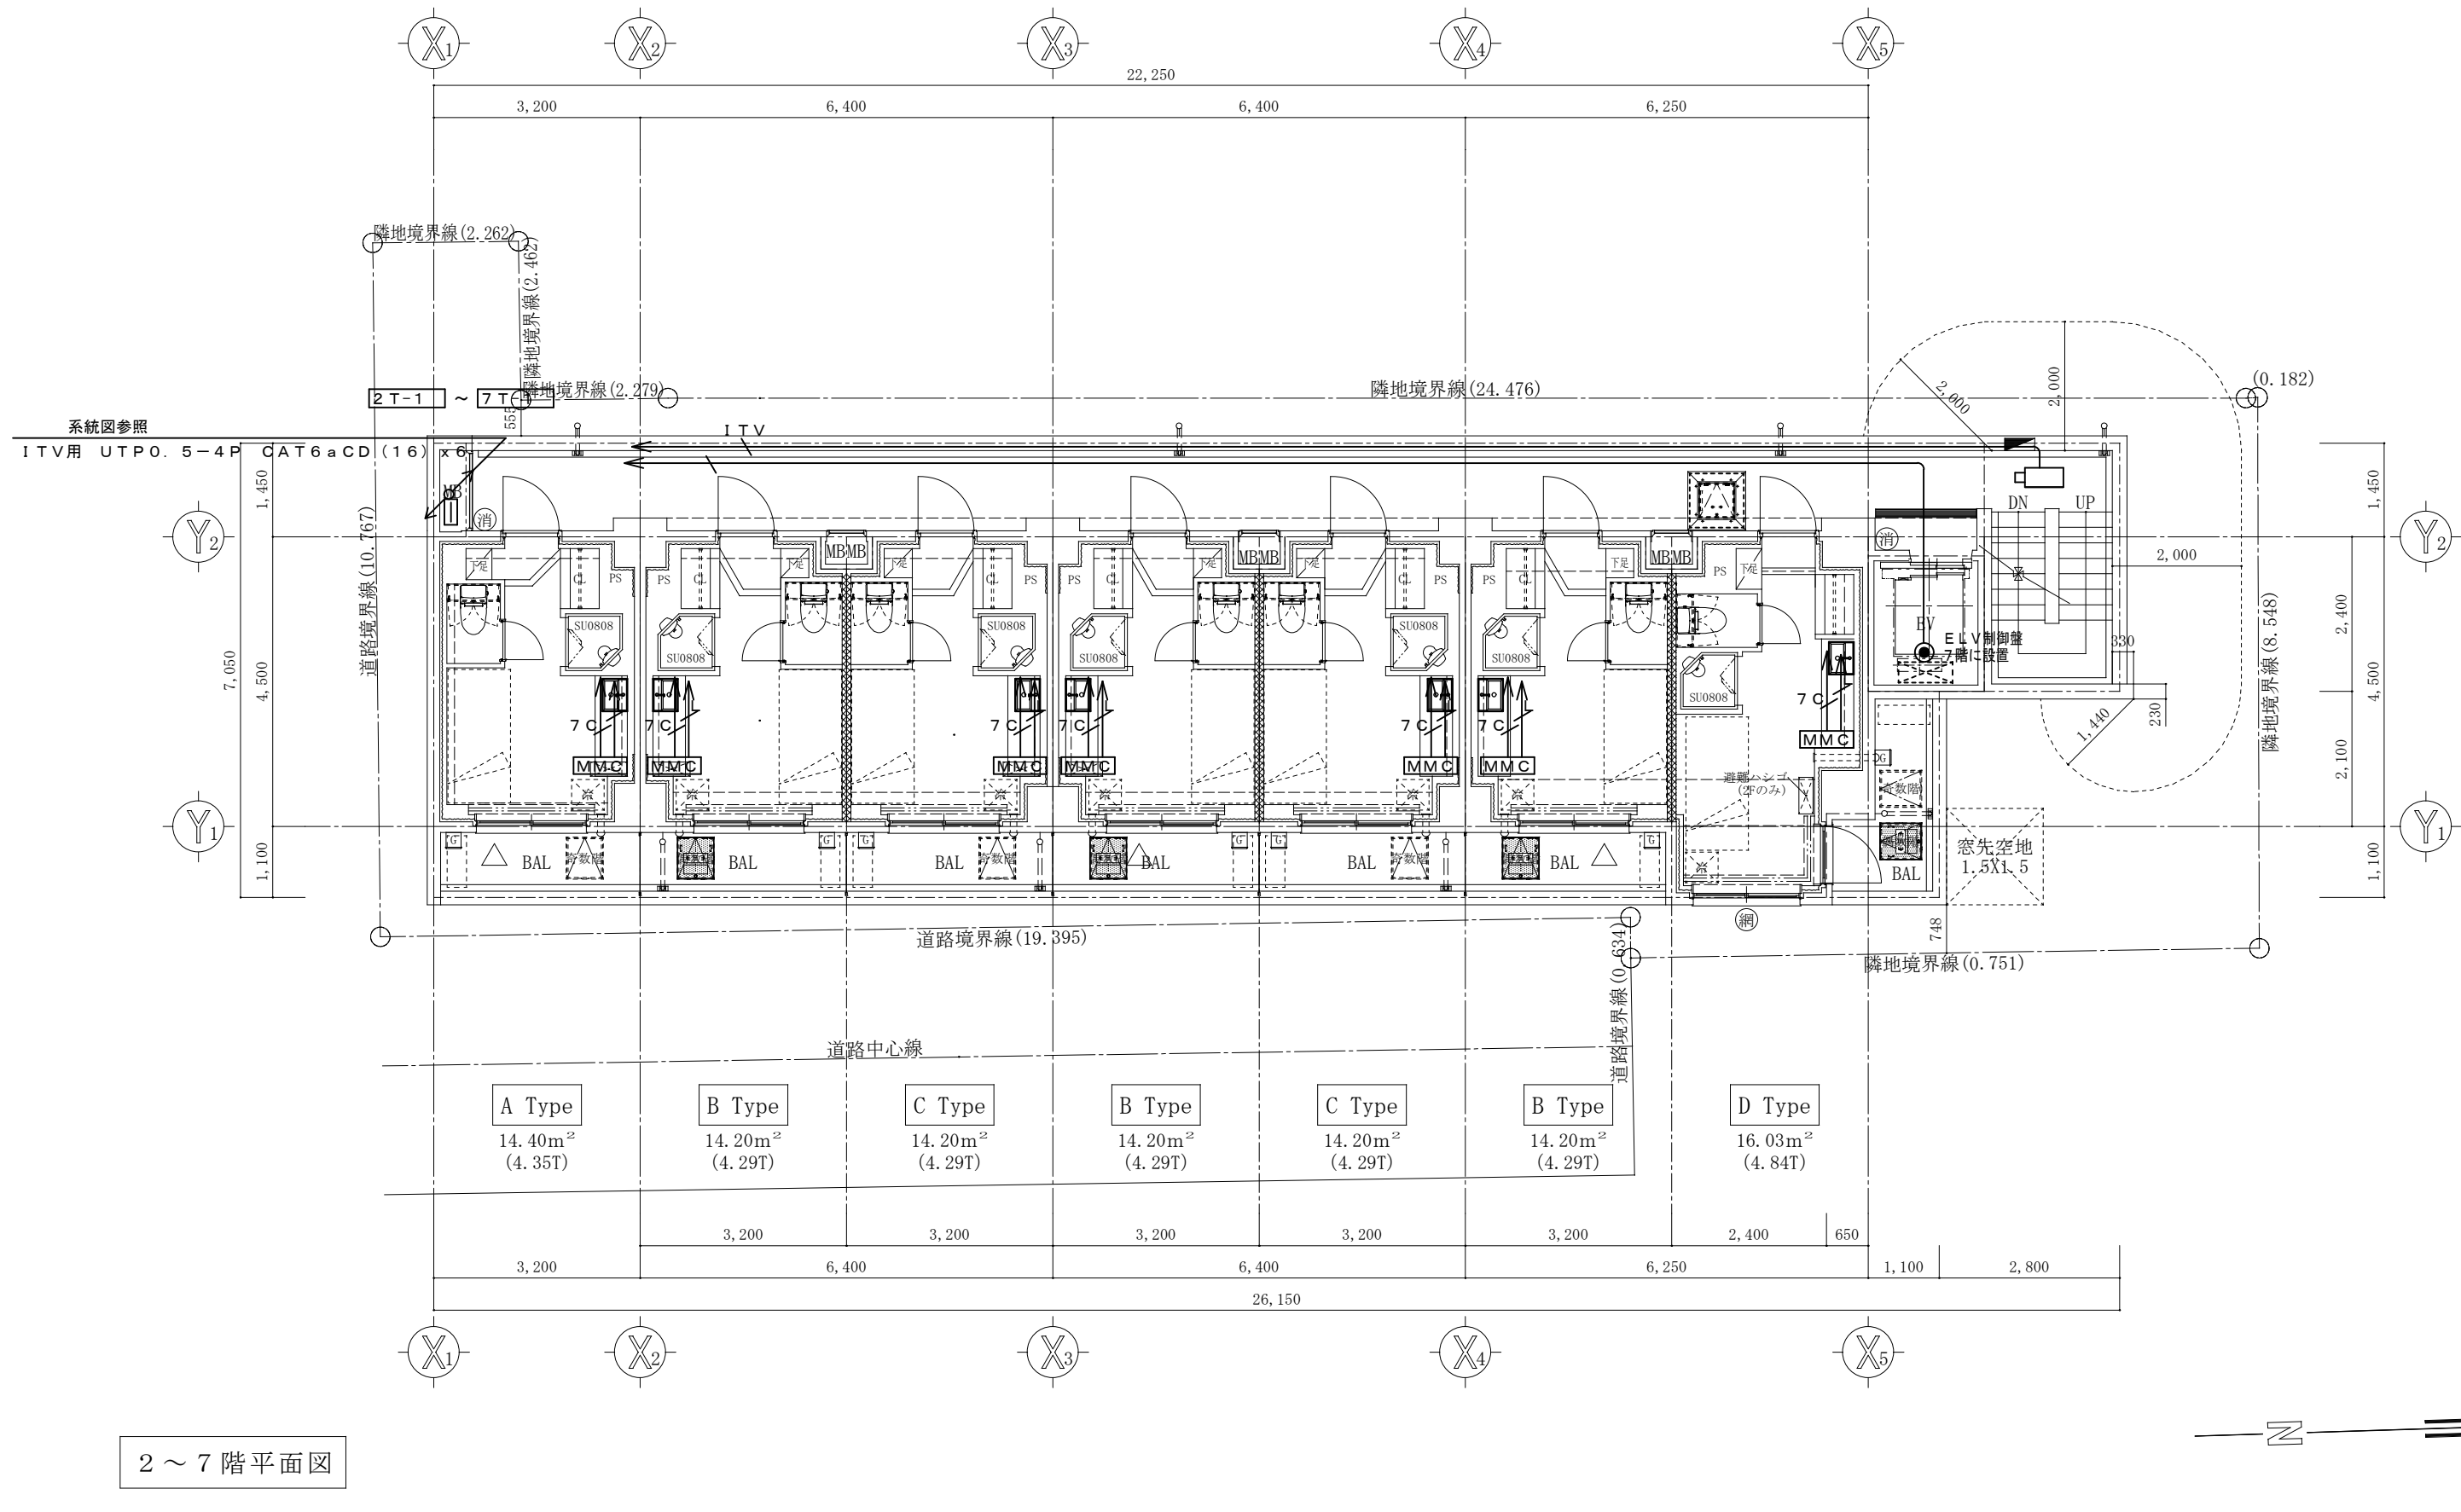

2 ～ 7 階平面図


Date	Revision	Ck.	Date	Revision	Ck.	Checked	Date	Drawn	Date	Project title	Scale	Unit
										(仮称) 墨田区石原2丁目計画 新築工事	1/100	MM
										Sheet content		
										弱电設備 平面図 (2)		
											E - 1 4	

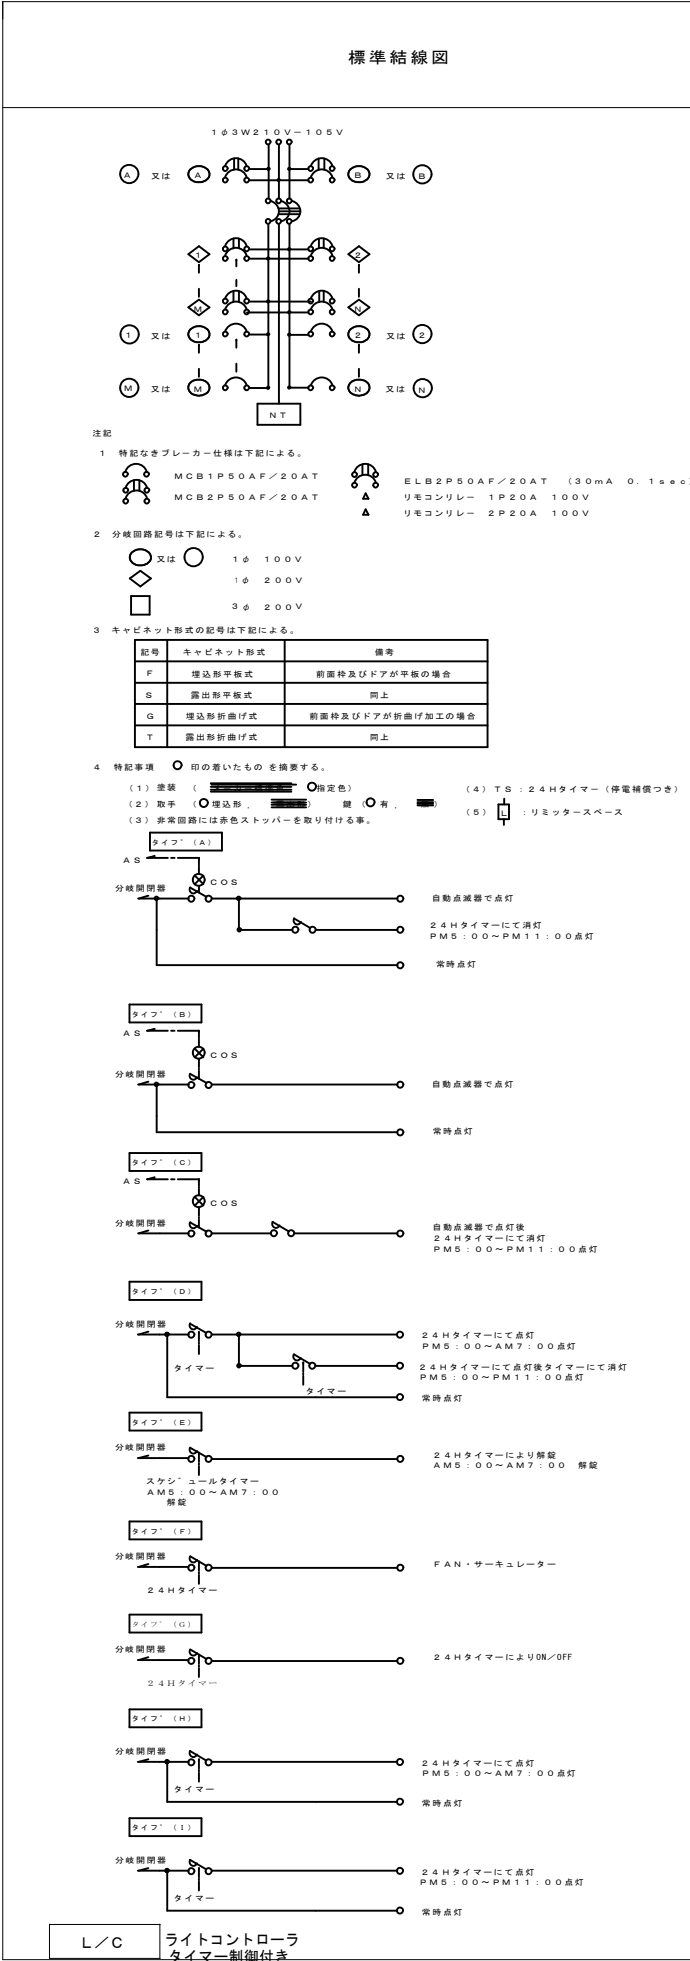

盤名称	電気方式 主開閉器容量 総容量	回路 番号	電圧 V	分岐 開閉器容量	負荷名称	負荷容量 (VA)		付属回路	備考	
						電灯	コンセント			
電灯分電盤 L-A (S)		A	100	MCB2P 50/20A	予備					
		A	100	MCB2P 50/20A	設備警報盤		150			
		B	#	MCB2P 50/20A	火災報知受信機		150			
		C	#	MCB2P 50/20A	インターホン制御盤		150			
		D	#	MCB2P 50/20A	ITV機器		150			
		E	#	MCB2P 50/20A	自動通報		150			
		F	#	MCB2P 50/20A	電気錠制御盤		150			
		G	#	MCB2P 50/20A	ノンタッチキー制御盤		150			
		H	#	MCB2P 50/20A	警備		150			
					</					

照明器具姿図								
A	スポットライト	B	ベースダウンライト	C	防湿 ダウンライト	D	ダウンライト	E
備考：スパイクを含む事		備考：専用電源別置き（見積りに含む事）		備考：専用電源別置き（見積りに含む事）		●NNU140113KLE9使用		LED 7.2W
2400TYPE LEDモジュール 電球色(3000K) 消費電力 20.0W ■非調光タイプ アルミダイキャスト レーザー仕上（ダークグレー） 透明強化ガラス 任意方向取付可能 電源内蔵フレレンジ 防湿防雨形（IP67） 調光不可 重：2.1kg		900TYPE LEDモジュール 調色12000K-1800K相当（12000-1800K） 消費電力 10.1W ■無線調光タイプ 枠：アルミダイキャスト（白艶消） コーン：アルミダイキャスト（鏡面マット仕上） 電源ユニット別売（別置形） 断熱施工不可 LED交換不可 無線モジュール付 重：0.7kg <無線調光タイプ>調光率：1-100% 径：φ85（mm） 埋込穴：φ75 埋込深さ：99（mm）		600TYPE LEDモジュール 電球色(3000K) 消費電力 10.4W ■無線調光タイプ 枠：アルミダイキャスト（黒艶消） コーン：アルミ（黒） 電源ユニット別売（別置形） 防湿形 LED交換不可 断熱施工不可 無線モジュール付 重：0.5kg <無線調光タイプ>調光率：5-100%		YAMADA AD-2614-L		LDL40Wx1 WP ガード付とする
造 蔭 ER56090H+B-520HA		造 蔭 SXD1020WA_SX101N		造 蔭 ERD8543BA_FX392NA		造 蔭 SX99002S パナソニック NNN71500		パナソニック NNF41051LE9
I	座 園 灯							あ
LED 2800K 6.3W 防雨型								非常照明器具
ボールを含む事								1 LED 1W バッテリー内蔵型 非常灯評定番号：LAL E-004
								2 LED 1.3W バッテリー内蔵型 非常灯評定番号：LAL E-006
								3 LED 1W バッテリー内蔵型 防湿型・防雨型 非常灯評定番号：LAL E-007
パナソニック XY2094LE1								あ1：パナソニック NNF891605C あ2：パナソニック NNF893605C あ2：パナソニック NNF891715C
ア	ダウンライト	イ	スポットライト					あ1
LED13.9Wx1 （電球色）		LEDユニット 4000K 14.7W						器具（あ1）で床面において2ルクス以上の照度を確保できる範囲
パナソニック LGB74103LE1		パナソニック NNN03732WLE1						器具取り付高さ2.1m2.4m2.6m 床面配置 A14.2m4.64.7
								あ2
								器具（あ2）で床面において2ルクス以上の照度を確保できる範囲
								器具取り付高さ2.1m2.4m2.6m3.0m4.0m5.0m6.0m 床面配置 A15.4m5.95.95.96.97.98.76.4
								あ3
								器具（あ3）で床面において2ルクス以上の照度を確保できる範囲
								器具取り付高さ2.1m2.4m2.6m3.0m 床面配置 A14.3m4.64.7
								い
								B級・B.L形 避難口誘導灯片面型

準工業地域
容積率300%・建ぺい率60%
日影規制：なし
準防火地域・22m高度地区

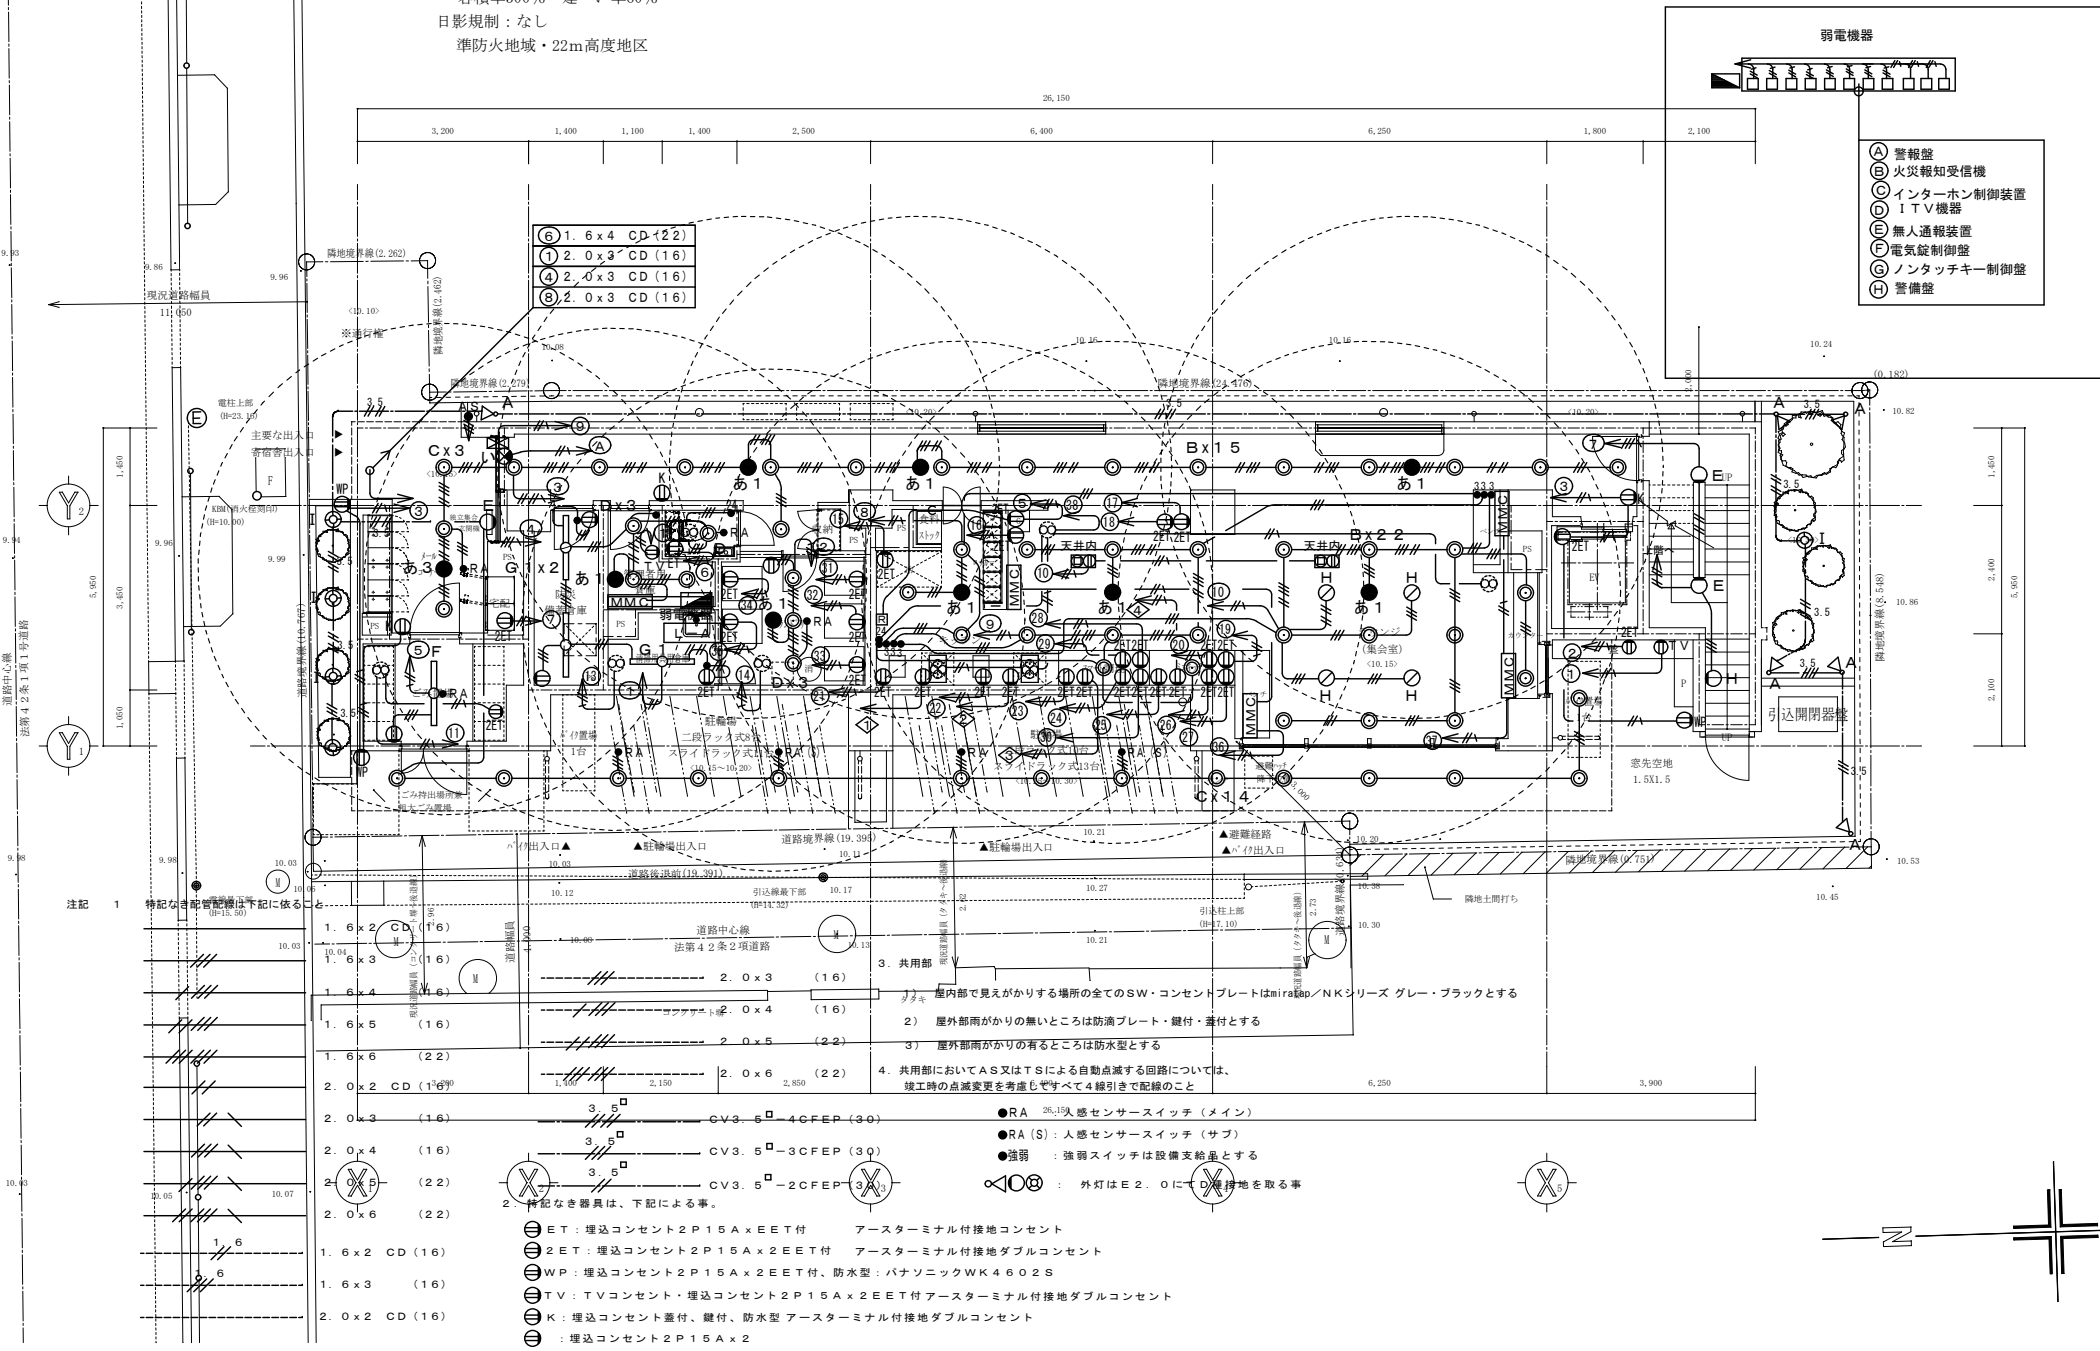

注記 1 特記なき配管配線は下記に依ること

- 1. 6 x 2 CD (16)
- 1. 6 x 3 CD (16)
- 1. 6 x 4 CD (16)
- 1. 6 x 5 CD (16)
- 1. 6 x 6 CD (22)
- 2. 0 x 2 CD (16)
- 2. 0 x 3 CD (16)
- 2. 0 x 4 CD (16)
- 2. 0 x 5 CD (22)
- 2. 0 x 6 CD (22)
- 2. 0 x 3 (16)
- 2. 0 x 4 (16)
- 2. 0 x 5 (22)
- 2. 0 x 6 (22)
- 2. 0 x 3 (16)
- 2. 0 x 4 (16)
- 2. 0 x 5 (22)
- 2. 0 x 6 (22)

- 3. 共用部
- 1) 屋内部で見えがかりする場所の全てのSW・コンセントプレートはmiraep/NKシリーズ グレー・ブラックとする
- 2) 屋外部雨がかりの無いところは防滴プレート・鍵付・蓋付とする
- 3) 屋外部雨がかりの有るところは防水型とする
- 4. 共用部においてAS又はTSによる自動点滅する回路については、竣工時の点滅変更を考慮し必ず4線引きで配線のこと

- RA 25,15A 人感センサースイッチ (メイン)
- RA (S) : 人感センサースイッチ (サブ)
- 遮断 : 強弱スイッチは設備支給品とする
- △108 : 外灯はE2.0にD接地地を取る事

2. 特記なき器具は、下記による事。

- ET : 埋込コンセント2P15A x EET付 アースターミナル付接地コンセント
- EET : 埋込コンセント2P15A x 2EET付 アースターミナル付接地ダブルコンセント
- WP : 埋込コンセント2P15A x 2EET付、防水型 : パナソニックWK4602S
- TV : TVコンセント・埋込コンセント2P15A x 2EET付 アースターミナル付接地ダブルコンセント
- K : 埋込コンセント蓋付、鍵付、防水型 アースターミナル付接地ダブルコンセント
- : 埋込コンセント2P15A x 2

確認E-07


Date	Revision	Ok.	Date	Revision	Ok.	Checked	Date	Drawn	Date	Project title	Scale	Unit
										(仮称) 墨田区石原2丁目計画 新築工事	1/100	MM
										電灯コンセント設備 平面図 (1)		

Sheet No. E-18

1. セキュリティ (非常)	■	有り	
2. セキュリティ (火災)	■	有り	☐ 無し
省令 40 号対応	☐	共用	☐ 住戸用 ■ 対応無し
3. セキュリティ (ガス)	☐	有り	■ 無し
4. セキュリティ (防犯)	☐	有り	■ 無し
5. セキュリティ移報	■	有り	☐ 無し
6. 集合玄関機組込キー	☐	逆マスター	■ 非接触キー
7. 宅配着荷表示	■	有り	☐ 無し
表示箇所	■	集合玄関機	■ 住宅情報盤
8. 管理室親機	■	有り	☐ 無し
9. お取次ぎ機能	■	有り	
10. 来客録画・留守録音	■	有り	
11. 住戸玄関カラーカメラ	☐	有り	■ 無し
12. 住宅情報盤モニターサイズ		7型ワイドモニター	
13. 住宅情報盤操作方式		タッチパネル方式	
14. エレベーター連動	☐	有り	■ 無し
信号形態	☐	接点	☐ シリアル
15. 宅外スマホ連携 (無線 LAN)	☐	有り	■ 無し
(スマホ連動機能: 呼出・通話・解錠・警報受信・宅配着荷・応答メッセージ・スマホ居室間通話)			
16. 置き配対応 (P a b b i t)	■	対応可	

The diagram illustrates the Pabbit Cloud system architecture, showing the following components and their interconnections:



- 住宅情報庫 (Residential Information Database):** The central hub for residential data.
- 玄関子機 (Entrance Sub-unit):** Connected to the Residential Information Database via "警報" (Alarm) and "呼出・通話" (Call/Communication) lines.
- 各階警報機 (各階通話表示部) (Each Floor Alarm/Call Display Unit):** Connected to the Residential Information Database via "警報" (Alarm) and "呼出・通話" (Call/Communication) lines.
- 着信表示 (Incoming Call Display):** Receives signals from the Entrance Sub-unit and Each Floor Alarm/Call Display Unit.
- 映像 (Video):** Transmits video data from the Entrance Sub-unit and Each Floor Alarm/Call Display Unit to the Management Room Terminal and the Common Entrance.
- 呼出・通話 (Call/Communication):** Transmits call/communication signals from the Entrance Sub-unit and Each Floor Alarm/Call Display Unit to the Management Room Terminal and the Common Entrance.
- 非常用押ボタン (Emergency Push Button):** Connected to the Management Room Terminal.
- 病錠 (Lock):** Connected to the Management Room Terminal.
- オートロック (Auto Lock):** Connected to the Management Room Terminal.
- 管理室観視機 (Management Room Observation Terminal):** Receives video and call/communication signals from the Entrance Sub-unit and Each Floor Alarm/Call Display Unit.
- 制御装置 (Control Device):** Connected to the Management Room Observation Terminal.
- インターネット (Internet):** Connects the Management Room Observation Terminal and Control Device to the Pabbit Cloud.
- Pabbit Cloud:** The central cloud service, connected to the Management Room Observation Terminal and Control Device.
- 共同玄関 (Common Entrance):** Receives video and call/communication signals from the Entrance Sub-unit and Each Floor Alarm/Call Display Unit.
- 照合 (Verification):** Transmits verification signals from the Common Entrance to the Management Room Observation Terminal and Control Device.









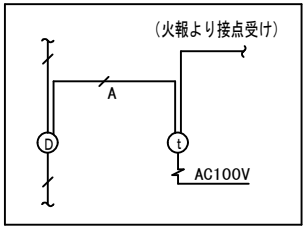


	AE0. 9-2C	(PF16)
	FCPEVO. 9-1P	(PF16)
	FCPEVO. 9-1P	(PF16) xn
	FCPEVO. 9-3P	(PF22)
	FCPEVO. 9-5P	(PF22)
	FCPEV-S0. 9-5P	(PF22)
	FCPEVO. 9-1P	(PF16)
	AE0. 9-3C	(PF16)
	UTPO. 5-4P (CAT5e)	(PF16)

AD	オートドア制御部	(建築工事)
TB	宅配ボックス 非接触キーリーダー	(建築工事) 組込み (建築工事)
R	警報発信装置	(別途設備工事)
NK	非接触キー制御部	(建築工事)
RT	ルーター	(別途設備工事)
ELV	ELV制御盤	(ELV工事)
① _{EV}	ELVインターホン	(ELV工事)
D	集合玄関機 非接触キーリーダー	(建築工事) 組込み


インターホン設備 系統図

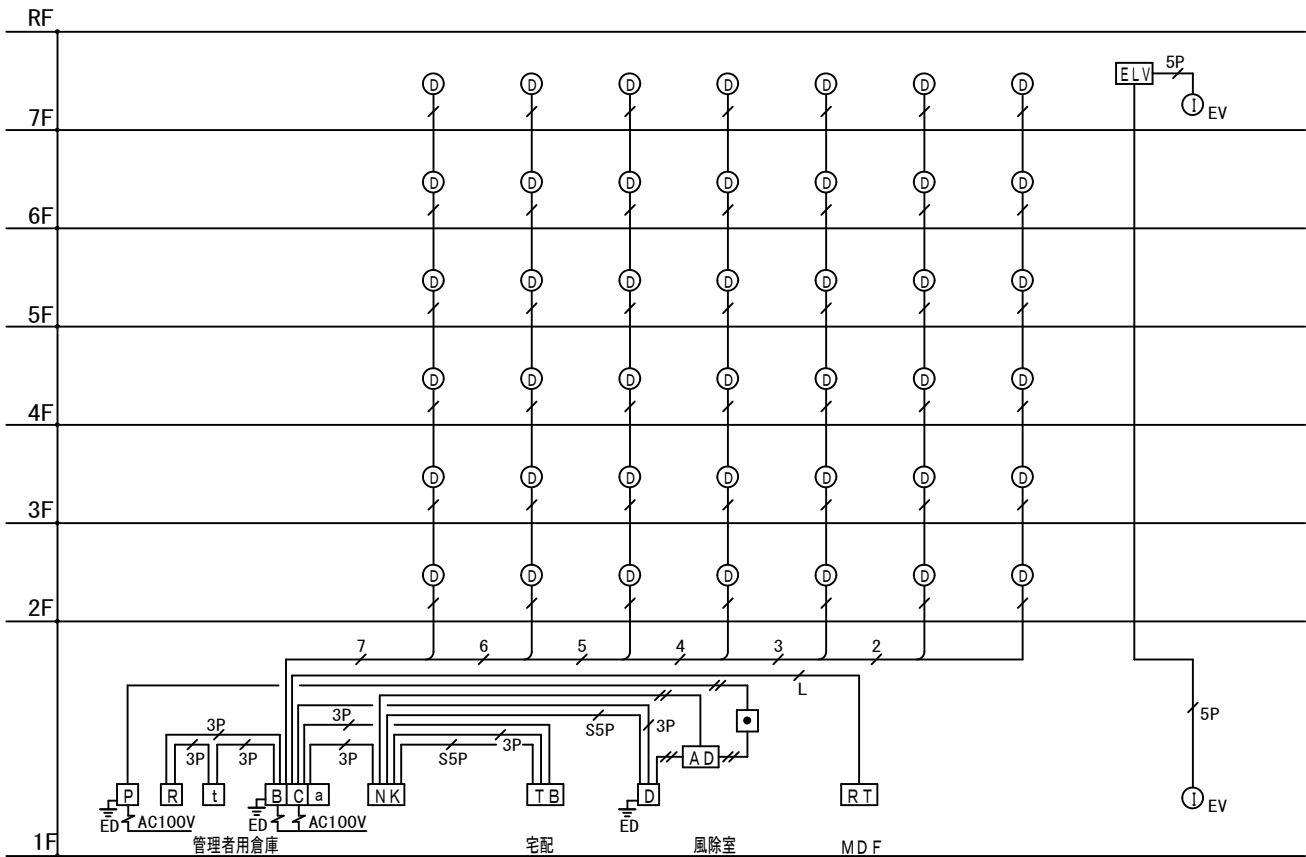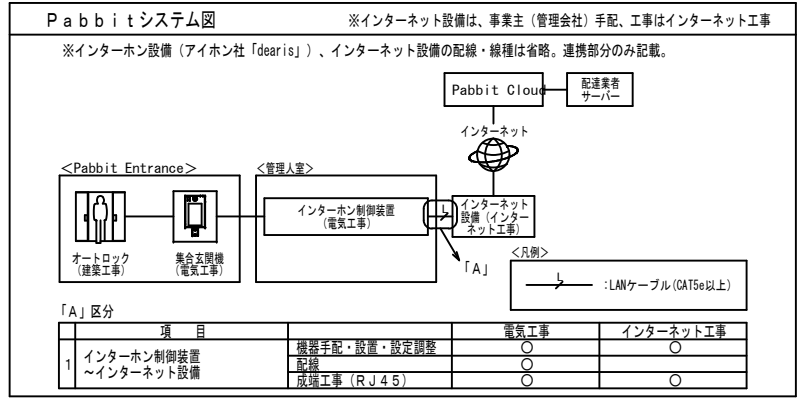

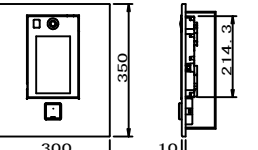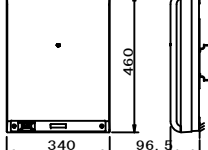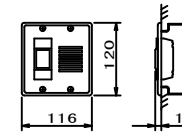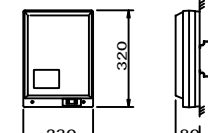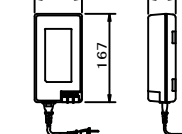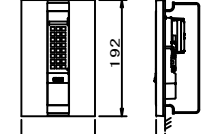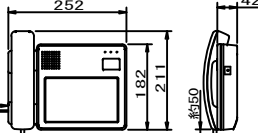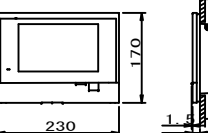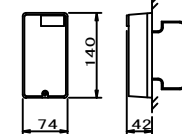D	カメラ付集合玄関機	C	制御装置
	VMX-DLMUB VMW-3035P-K  電源電圧 DC24V (制御装置または電源アダプタから供給) 通信方式 遠隔先の機器に依存する 形 状 壁掛け型 (専用スイッチボックス) 材質/色調 樹脂製樹脂 (パネル: アルミ) / ブラック カメラ 1/2.7型カラーCMOS 監視 直射日光や強い室外線の当たる場所への設置は避けること 備考 非接触キー受信部 (建築工事) D 接地地必要		VMX-4XB  電源電圧 AC100V 50/60Hz 形 状 壁掛け型 (JIS3用スイッチボックス+セパレーター) 材質 樹脂製樹脂 住戸数 最大500住戸 (1系統最大125住戸) 集合玄関機 最大32台 管理室機能 最大4台 (カメラ付は最大2台) 運動出力 全館ボックス、エレベーター、非接触キー、警報装置、EV充電システム 備 考
E	非常時解錠押ボタン	B	増幅器 (4系統)
	VX-KB24  電源電圧 DC12V (電源アダプターから供給) 形 状 埋込型 (JIS2用スイッチボックス) 材質 ステンレスパネル 接点定格 AC250V 6A 備 考 プラゲ内蔵、ロック式、引き戻し機構		VJW-4VG  電源電圧 AC100V 50/60Hz 形 状 壁掛け型 (JIS3用スイッチボックス+セパレーター) 材質 自己消火性樹脂 備 考 4系統出力 (1系統あたり1の最大住戸数は25住戸) VJシステム専用
F	電源アダプタ	D	玄関機
	PS-1225A  電源電圧 AC100V 出力電圧 DC12V 出力電流 2.5A 形 状 箱型・壁取付 (専用金具) 両用 材質 樹脂		VJ-DP VJW-3P-S VJW-2AVS  電源電圧 住宅情報機より供給 形 状 壁埋込型 (JIS3用スイッチボックスカバー付) 材質 難燃性樹脂/自己消火性樹脂 備考 防塵・防湿形 (JIS C 0920 IP54 相当) 絶縁アダプター接続 戸外表示器型式確認品 (VJW-3P-S装着時)
I	管理室親機	I	住宅情報盤
	VMX-MKRA  電源電圧 DC24V (制御装置または電源アダプターPS-2410Aから供給) 形 状 箱型・壁取付用型 (JIS3用スイッチボックス) 材質 難燃性樹脂 モニター 7型タッチパネルカラー液晶モニター 備 考 警報表示、メモリーメッセージ機能付		VM-RMY-NS  電源電圧 AC100V 50/60Hz 警報機能 非常・火災 通信方式 同通信装置方式 ディスプレー 7型 TFT 液晶ディスプレイ (タッチパネル) 形状/材質 壁埋込型 (専用ボックス: A-V (D) VJ) / 難燃性樹脂 備 考 録画機能付
A	映像アダプター		
	VHW-1AVA  形 状 壁掛け型 (JIS3用スイッチボックス) 材質 自己消火性樹脂 備 考 1住戸に1台設置 1通話路・1映像路用		

Date Revision Ck.			Date Revision Ck.			Checked Date		Drawn Date		Project title		Scale Unit	
										(仮称) 墨田区石原2丁目計画 新築工事		MM	
										Sheet content		Sheet No.	
										株式会社 小野田建築設計事務所 ARCHITECTURE & ENGINEERING Dept. 一級建築士登録第255585号 小野田 貴夫		インターホン設備 系統図・凡例・注記・姿図 E - 2 2	

準工業地域
容積率300%・建ぺい率60%
日影規制：なし
準防火地域・22m高度地区

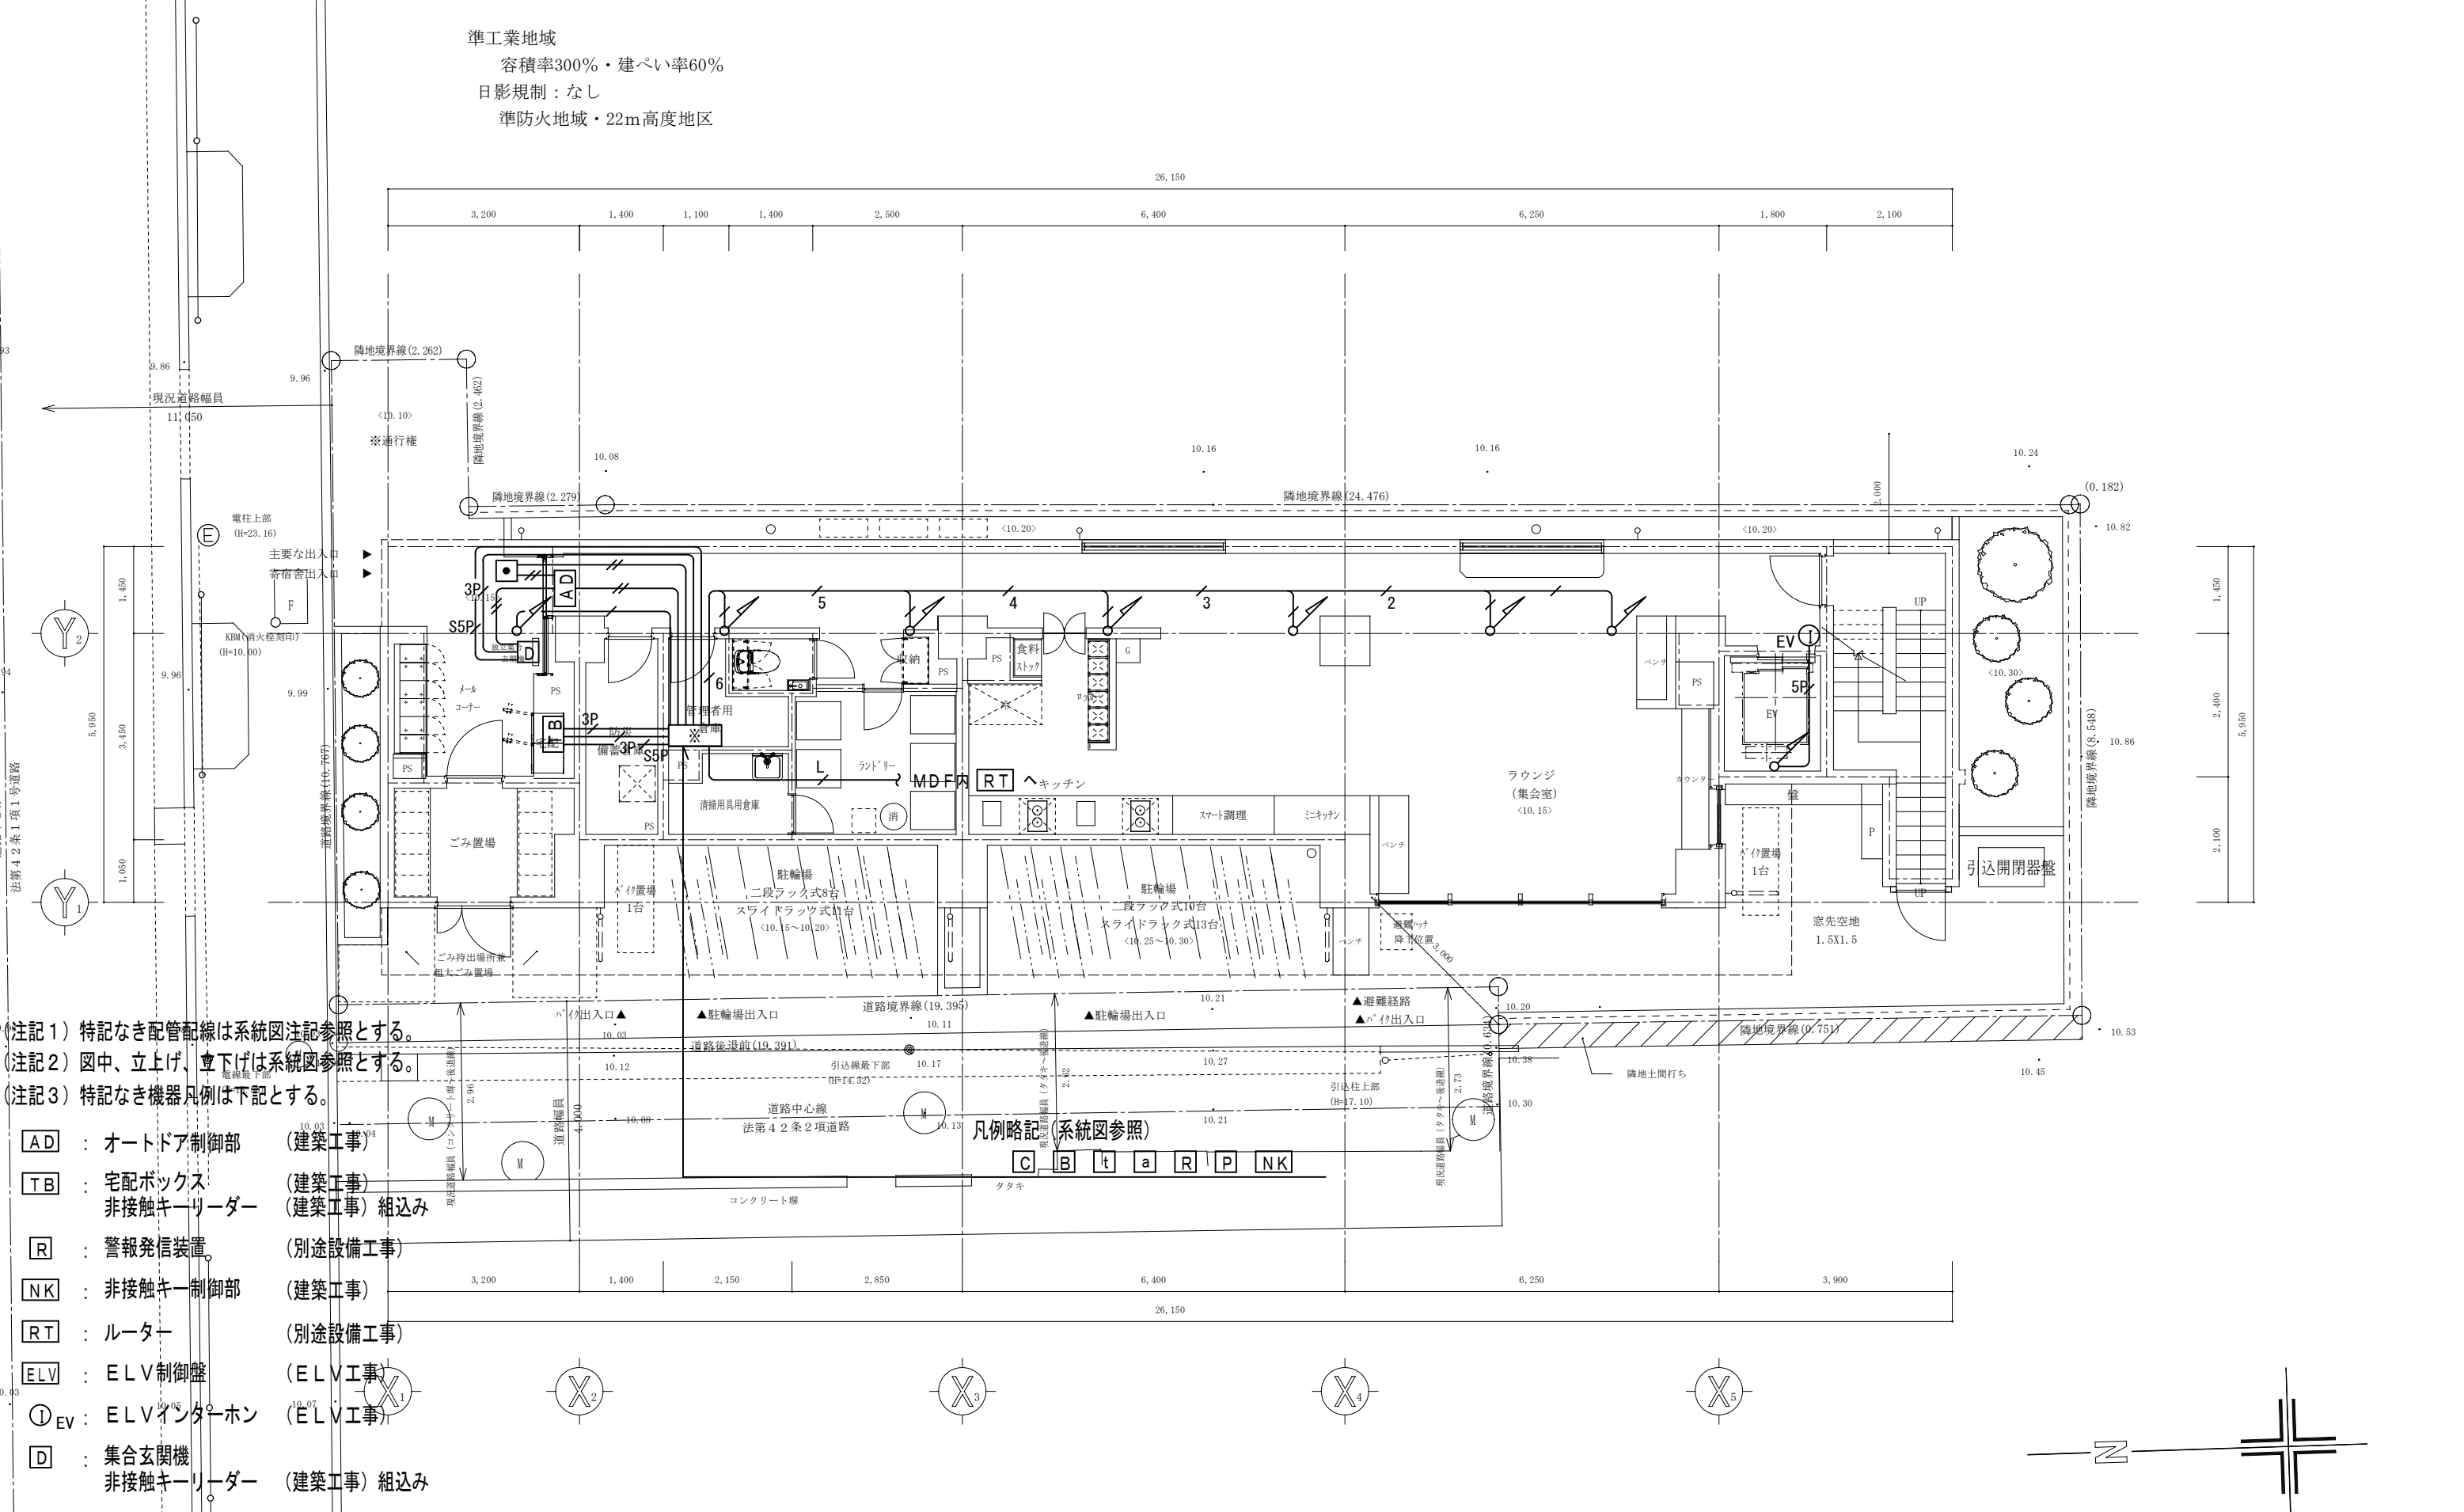


(注記1) 特記なき配管配線は系統図注記参照とする。
(注記2) 図中、立上げ、垂下げは系統図参照とする。
(注記3) 特記なき機器凡例は下記とする。

- [AD] : オートドア制御部 (建築工事)
- [TB] : 宅配ボックス (建築工事)
非接触キーリーダー (建築工事) 組込み
- [R] : 警報発信装置 (別途設備工事)
- [NK] : 非接触キー制御部 (建築工事)
- [RT] : ルーター (別途設備工事)
- [ELV] : ELV制御盤 (ELV工事)
- ①EV : ELVインターホン (ELV工事)
- [D] : 集合玄関機 (建築工事)
非接触キーリーダー (建築工事) 組込み

(注記4) MDF室～管理室間の有線LAN配線が不可の場合、管理室内のインターネット環境の利用でも可とする。

Date			Revision			Checked	Date	Drawn	Date	Project title	Scale	Unit
Date	Revision	Ck.	Date	Revision	Ck.							
										(仮称) 墨田区石原2丁目計画 新築工事	1/100	MM
										Sheet content		
										インターホン設備平面図 (1)		E - 2 3

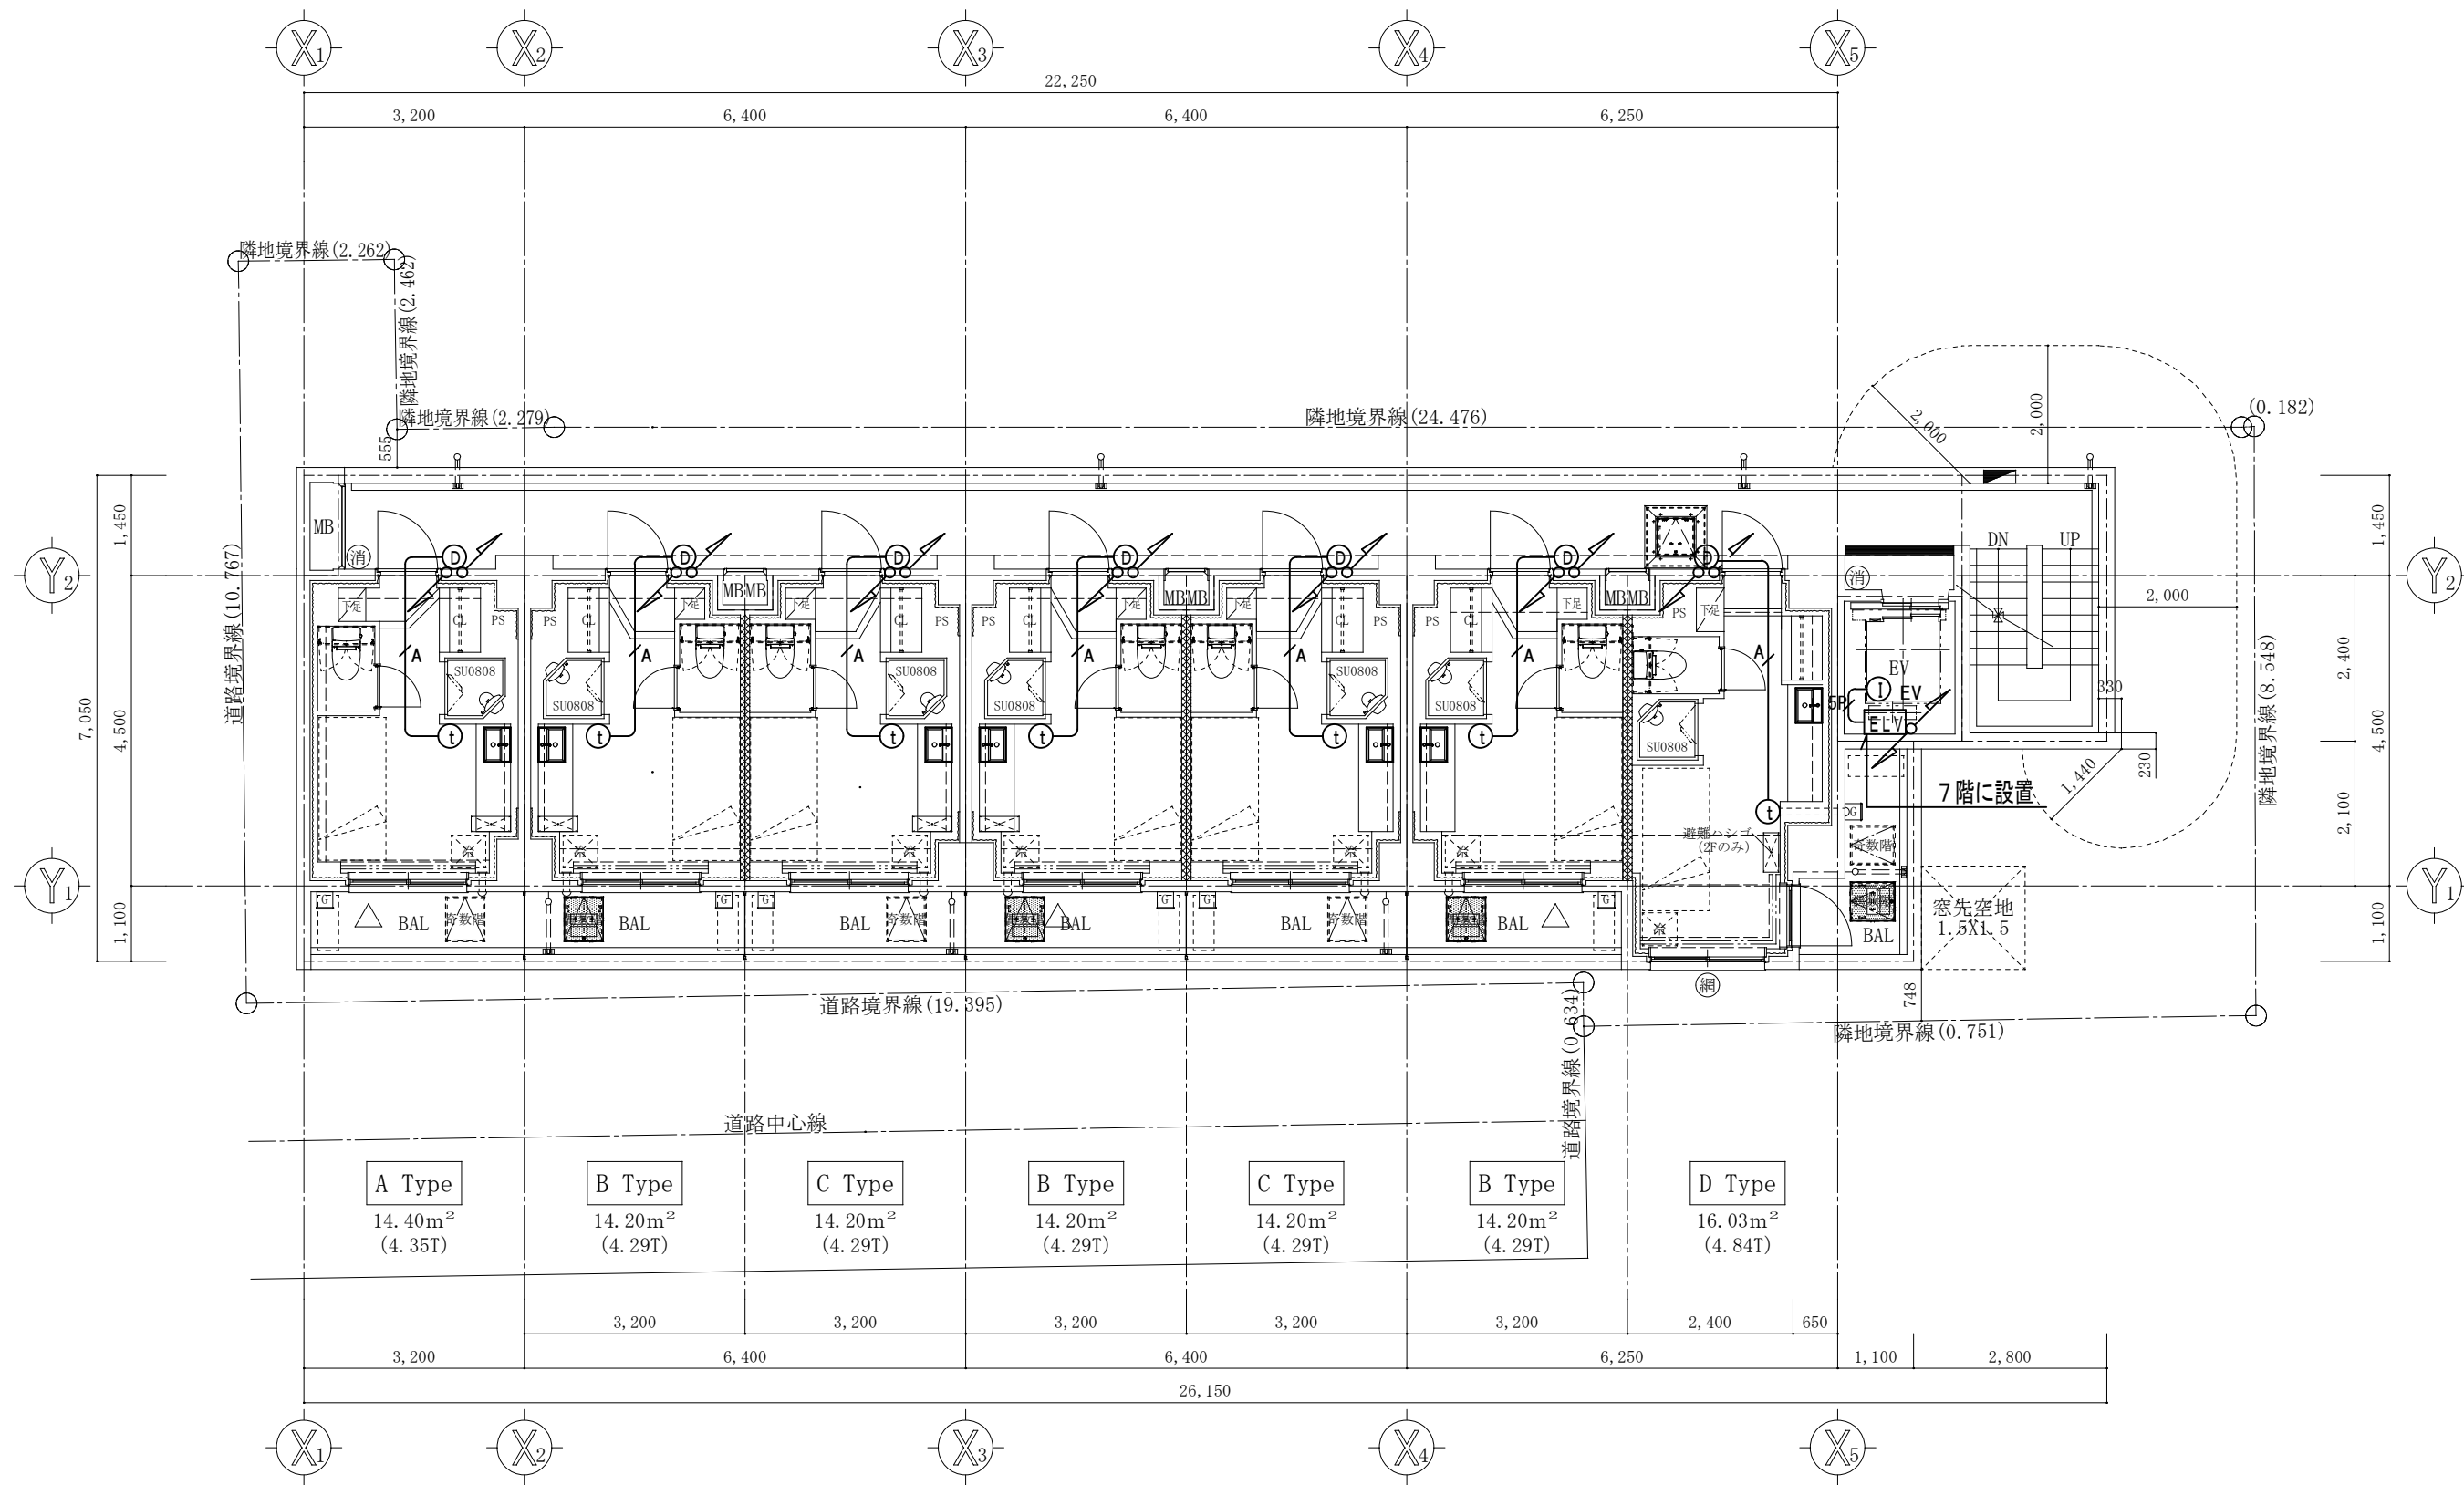

2 ～ 7 階平面図

Date			Revision			Ck.	Date	Checked	Date	Drawn	Date	Project title		Scale	Unit
Date	Revision	Ck.	Date	Revision	Ck.							Sheet content			
												株式会社 小野田 建築設計事務所		1/100	MM
												ARCHITECTURE & ENGINEERING Dept.			
												一級建築士登録第255585号 小野田 貴夫			
												（仮称）墨田区石原2丁目計画 新築工事		Sheet No.	E - 2 4
												インターホン設備平面図（2）			


凡 例

記 号	名 称	備 考
	受 信 機	注記参照
	機 器 収 容 箱	埋込型 縦型 ㊸㊹ 収容
	機 器 収 容 箱	埋込屋外型 縦型 ㊸㊹ 収容
	機 器 収 容 箱	放水口組込屋外型 ㊸㊹ 収容
㊸	電 鈴	DC24V 露出型 防雨型
㊹	電 鈴	DC24V 露出型
㊺	フ ラ ッ ト 発 信 機	P型1級 専用表示灯 (24V LED) 付 屋内・屋外用
	光電式スポット型感知器	2種 露出型
	光電式スポット型感知器	2種 壁付用点検口
	差動式スポット型感知器	2種
	差動式スポット型感知器	2種 防水型
	定温式スポット型感知器	特種 防水型 60℃
	定温式スポット型感知器	1種 防水型 70℃
	終 端 器	
	中 継 器	感知器信号移報用
①	住 宅 情 報 盤	(インターホン工事)
■	非常時解錠押ボタン	ブザー付
	エレベーター制御盤	(ELV工事)
	電 気 錠 制 御 盤	(建築工事)
㊻	電 気 錠	(建築工事)
	オートドア制御部	(建築工事)
	配 管 配 線	天井いんぺい
	配 管 配 線	床いんぺい
	配 管 配 線	立上げ・立下げ
	ブ ル ボ ッ ク ス	
	警戒区域境界線	
	警 戒 区 域 番 号	自火報用


注 記

1。受信機
1) 種別 P型1級受信機 蓄積式 埋込型
2) 表示方式
a) 地区表示部 火災表示 10回線 窓式
3) 移信出力
・エレベーター制御盤 火災代表 1点
・電気錠制御盤 火災代表 1点
・オートドア制御部 火災代表 1点
・予備 2点
4) 回線内訳
・火災表示 8 L
・予備 2 L
・合計 10 L
2。電鈴は、一斉鳴動方式とする。
3。感知器に、Pを付記したものは、外部制御用P端子付とする。


4。住戸内感知器は、外部制御用P端子付きとし、住戸内の火災信号を住宅情報盤へ移信する。
5。エレベーター用煙感知器の点検ボックスの設置において、以下の工事区分はエレベーター工事とする。 ・エレベーター連動停止用スイッチ (スイッチ・取り付け・結線・試験) ・注意喚起シール (シール・貼り付け)
6。本物件は、日本住宅性能表示制度基準「火災時の安全に関すること」において、以下の各等級を取得するものとする。 感知警報装置設置等級：自住戸火災時 等級4 ・ 他住戸等火災時 等級4
7。オートドアに非常時解錠押ボタンを設置する。(インターホン工事)
8。特記なき配管配線は下記とする。
AE0. 9- 2C (PF16) AE0. 9- 4C (PF16)
AE0. 9- 3P (PF16)
HP0. 9- 2C (PF16)
9。区画貫通部は打ち込み配管とする。

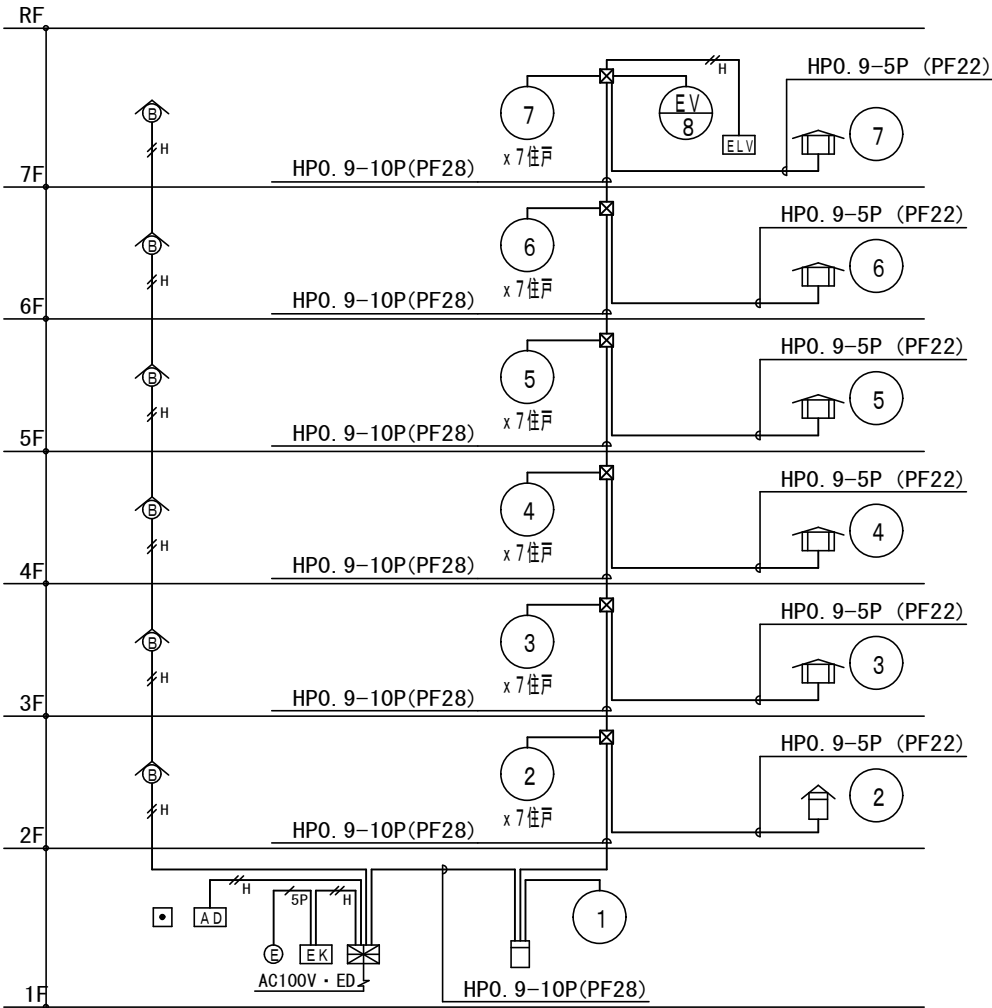

参考姿図

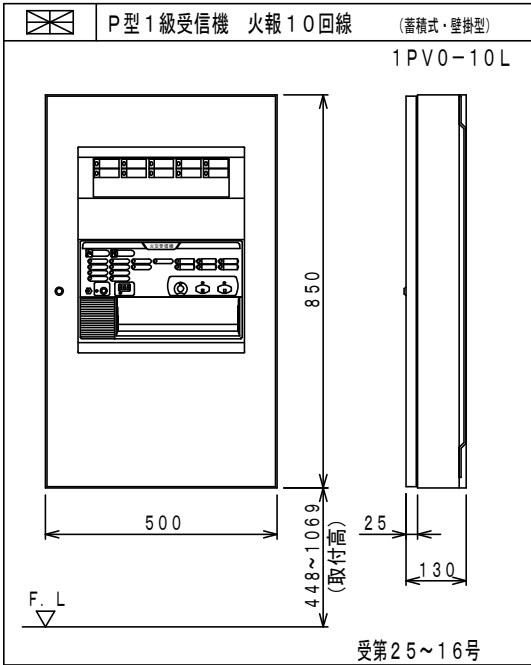

(注記) 住戸内詳細図

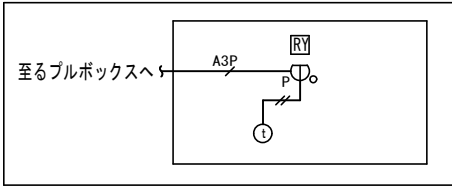


自動火災報知設備 系統図

確認 E-08


Date	Revision	Ck.	Date	Revision	Ck.	Checked	Date	Drawn	Date	Project title	Scale	Unit
										(仮称) 墨田区石原2丁目計画 新築工事		MM
										Sheet content		
										自動火災報知設備 系統図・凡例・機器図		

準工業地域
容積率300%・建ぺい率60%
日影規制：なし
準防火地域・22m高度地区

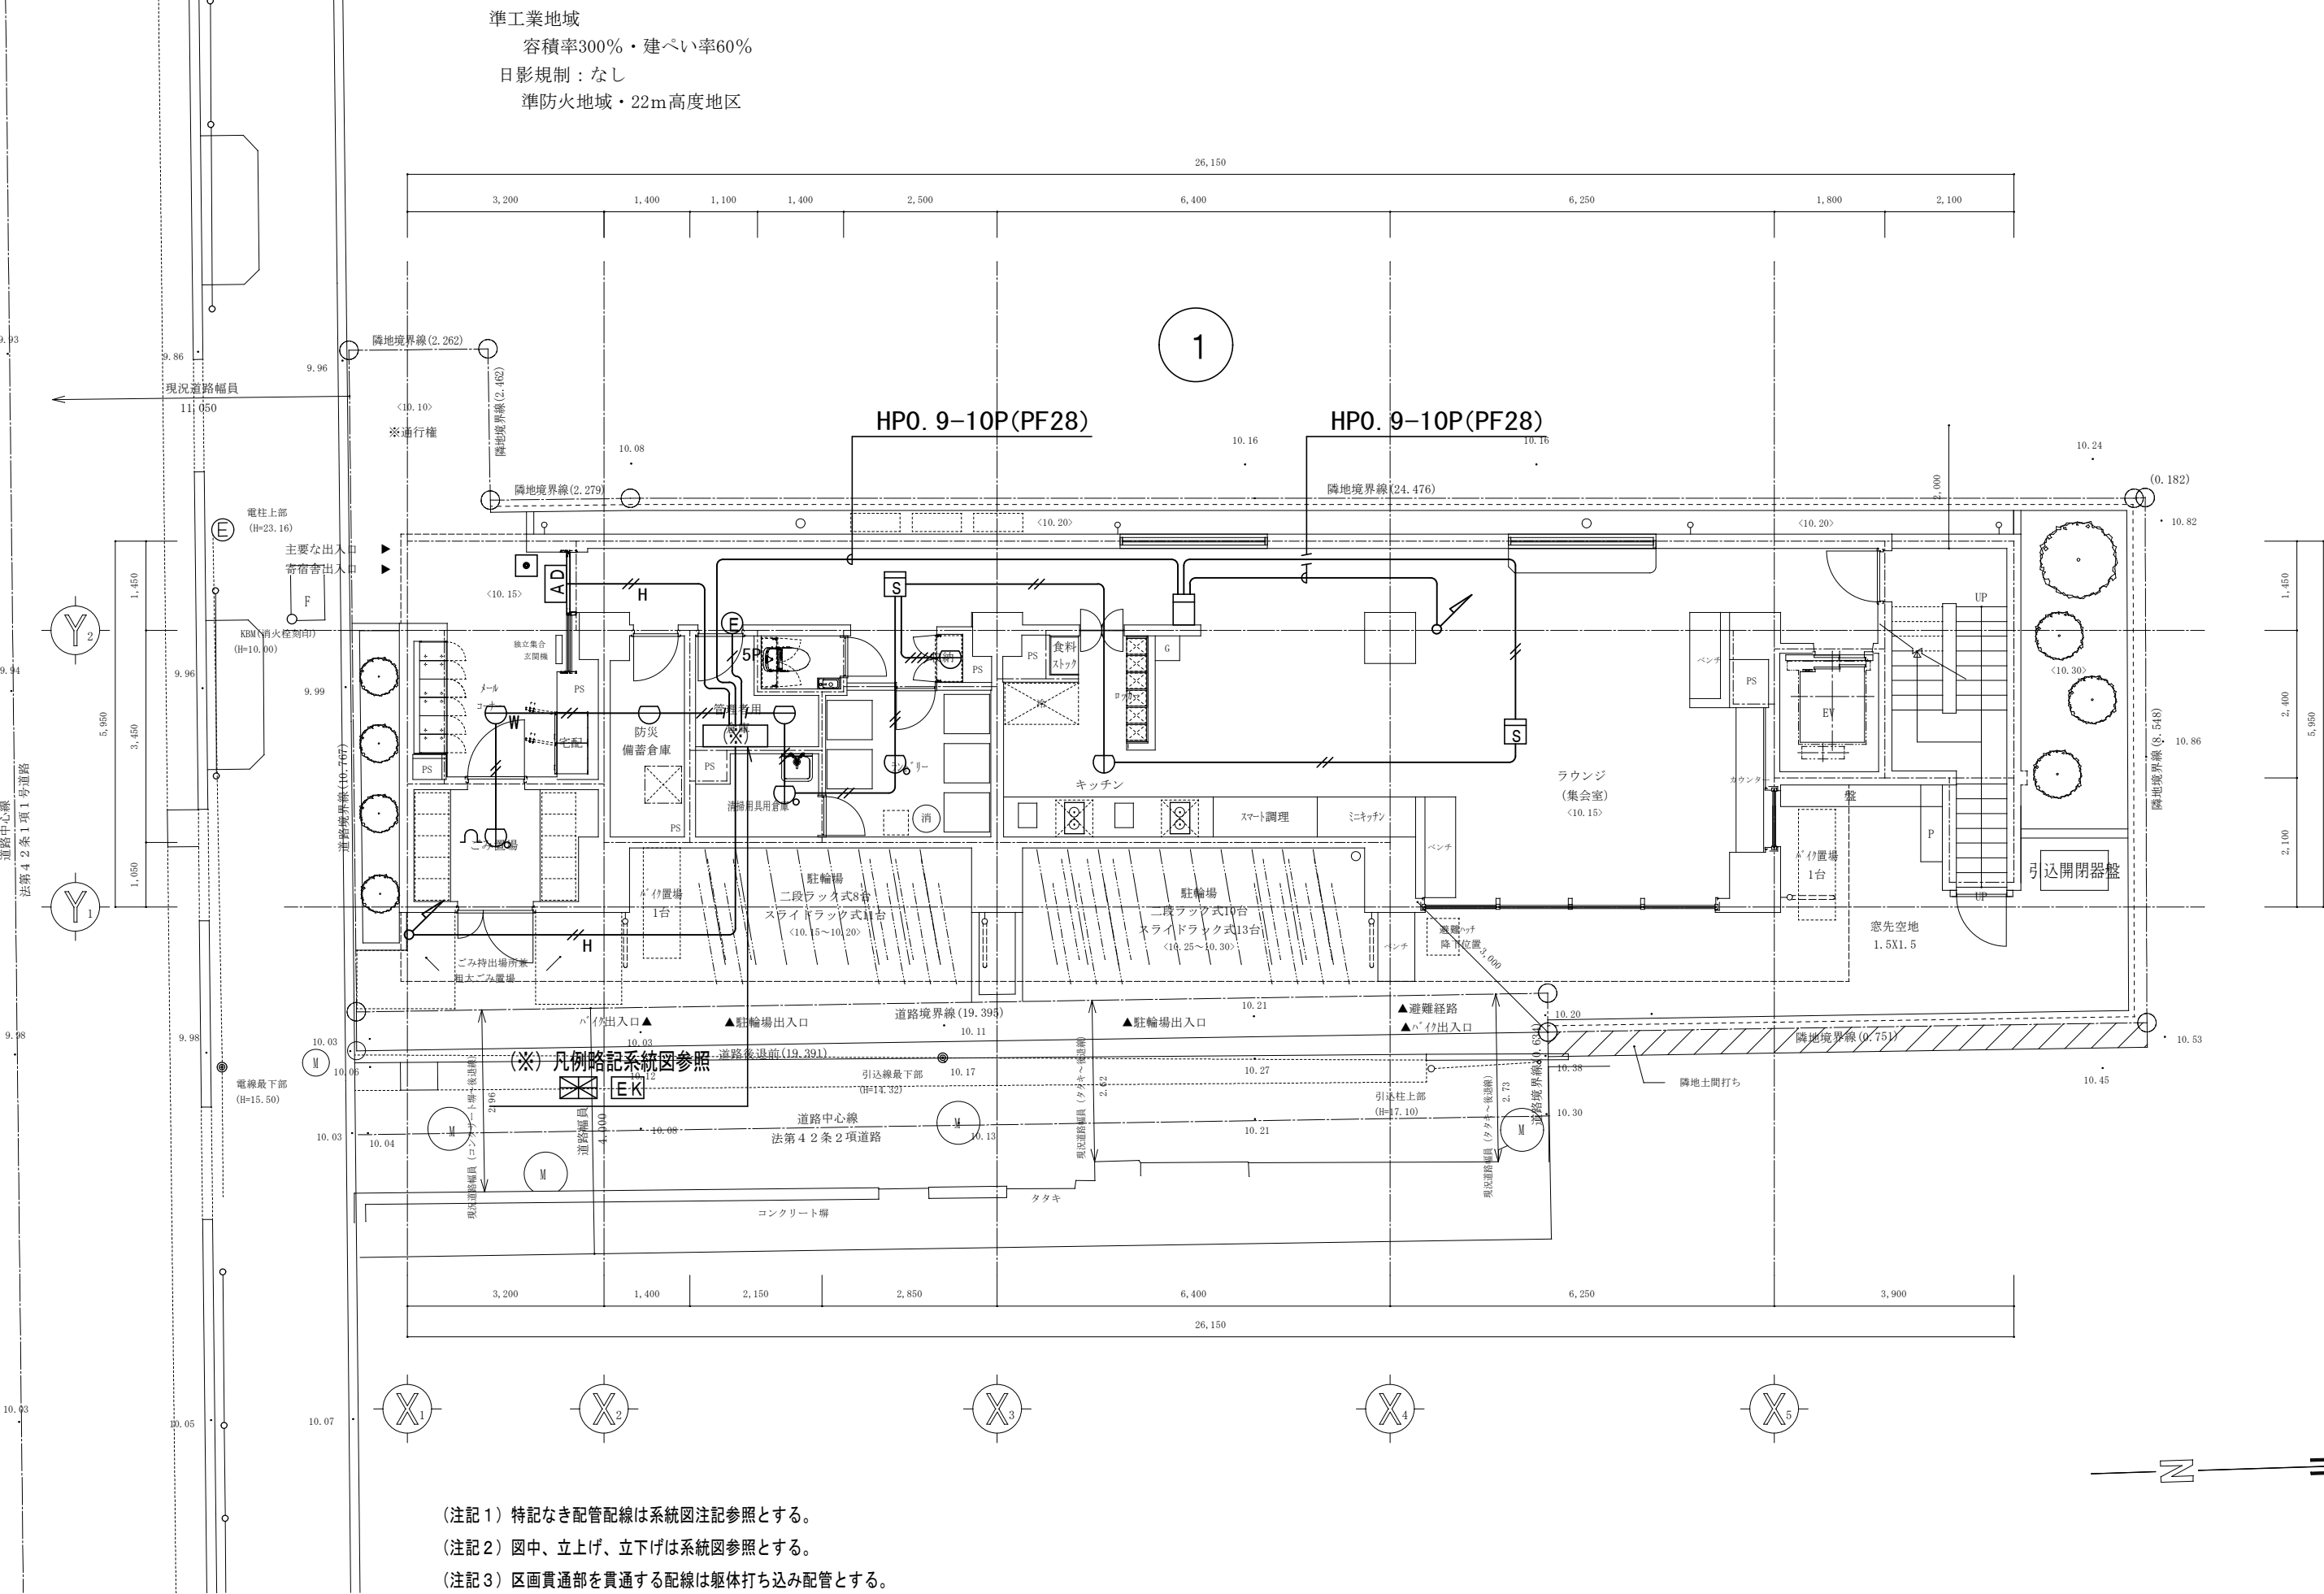

(注記1) 特記なき配管配線は系統図注記参照とする。
(注記2) 図中、立上げ、立下げは系統図参照とする。
(注記3) 区画貫通部を貫通する配線は躯体打ち込み配管とする。

Date			Revision			Ck.	Date			Revision			Ck.	Checked	Date	Drawn	Date	株式会社 小野田建築設計事務所 ARCHITECTURE & ENGINEERING Dept. 一級建築士登録第255585号 小野田 貴夫			Project title			Scale			Unit				
																					(仮称) 墨田区石原2丁目計画 新築工事			1/100			MM				
																					Sheet content			Sheet No.							
																					自動火災報知設備平面図 (1)			E - 2 6							

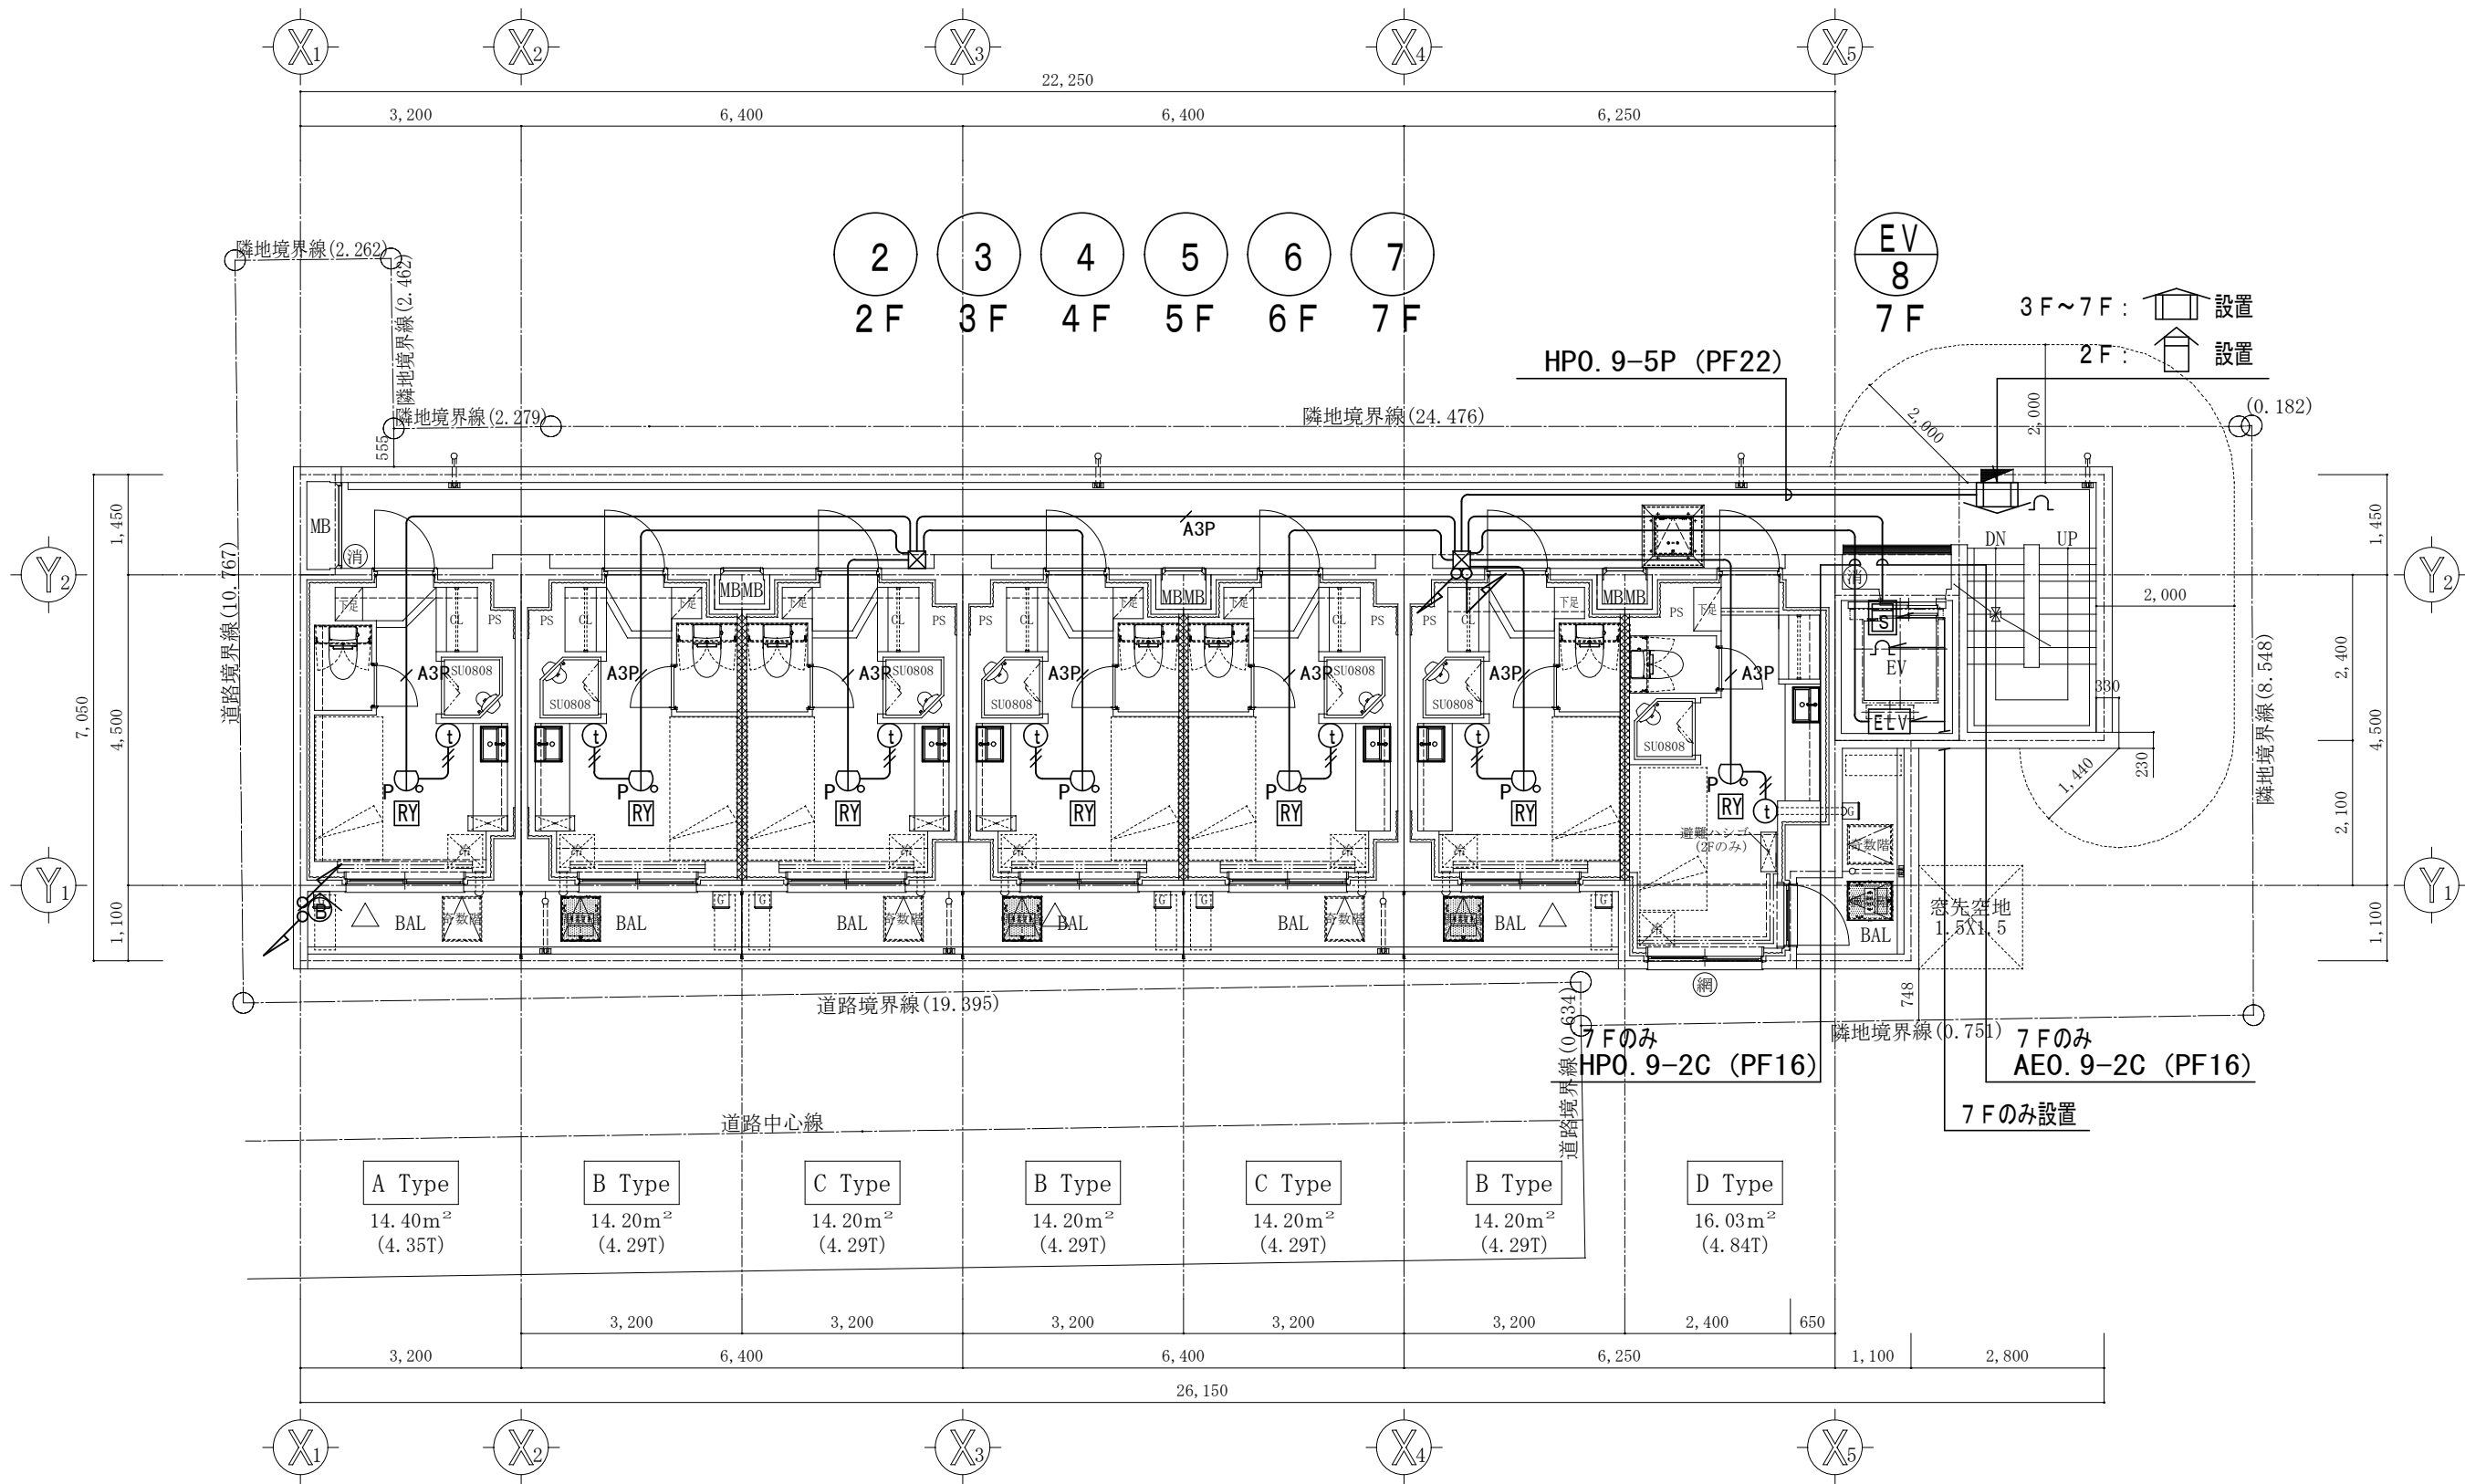


2 ～ 7 階平面図

- (注記 1) 特記なき配管配線は系統図注記参照とする。
- (注記 2) 図中、立上げ、立下げは系統図参照とする。
- (注記 3) 区画貫通部を貫通する配線は躯体打ち込み配管とする。

Date			Revision			Checked	Date	Drawn	Date	Project title	Scale	Unit
Date	Revision	Ck.	Date	Revision	Ck.							
										(仮称) 墨田区石原2丁目計画 新築工事	1/100	MM
										Sheet content		
										自動火災報知設備平面図 (2)		
											E - 27	

準工業地域
容積率300%・建ぺい率60%
日影規制：なし
準防火地域・22m高度地区

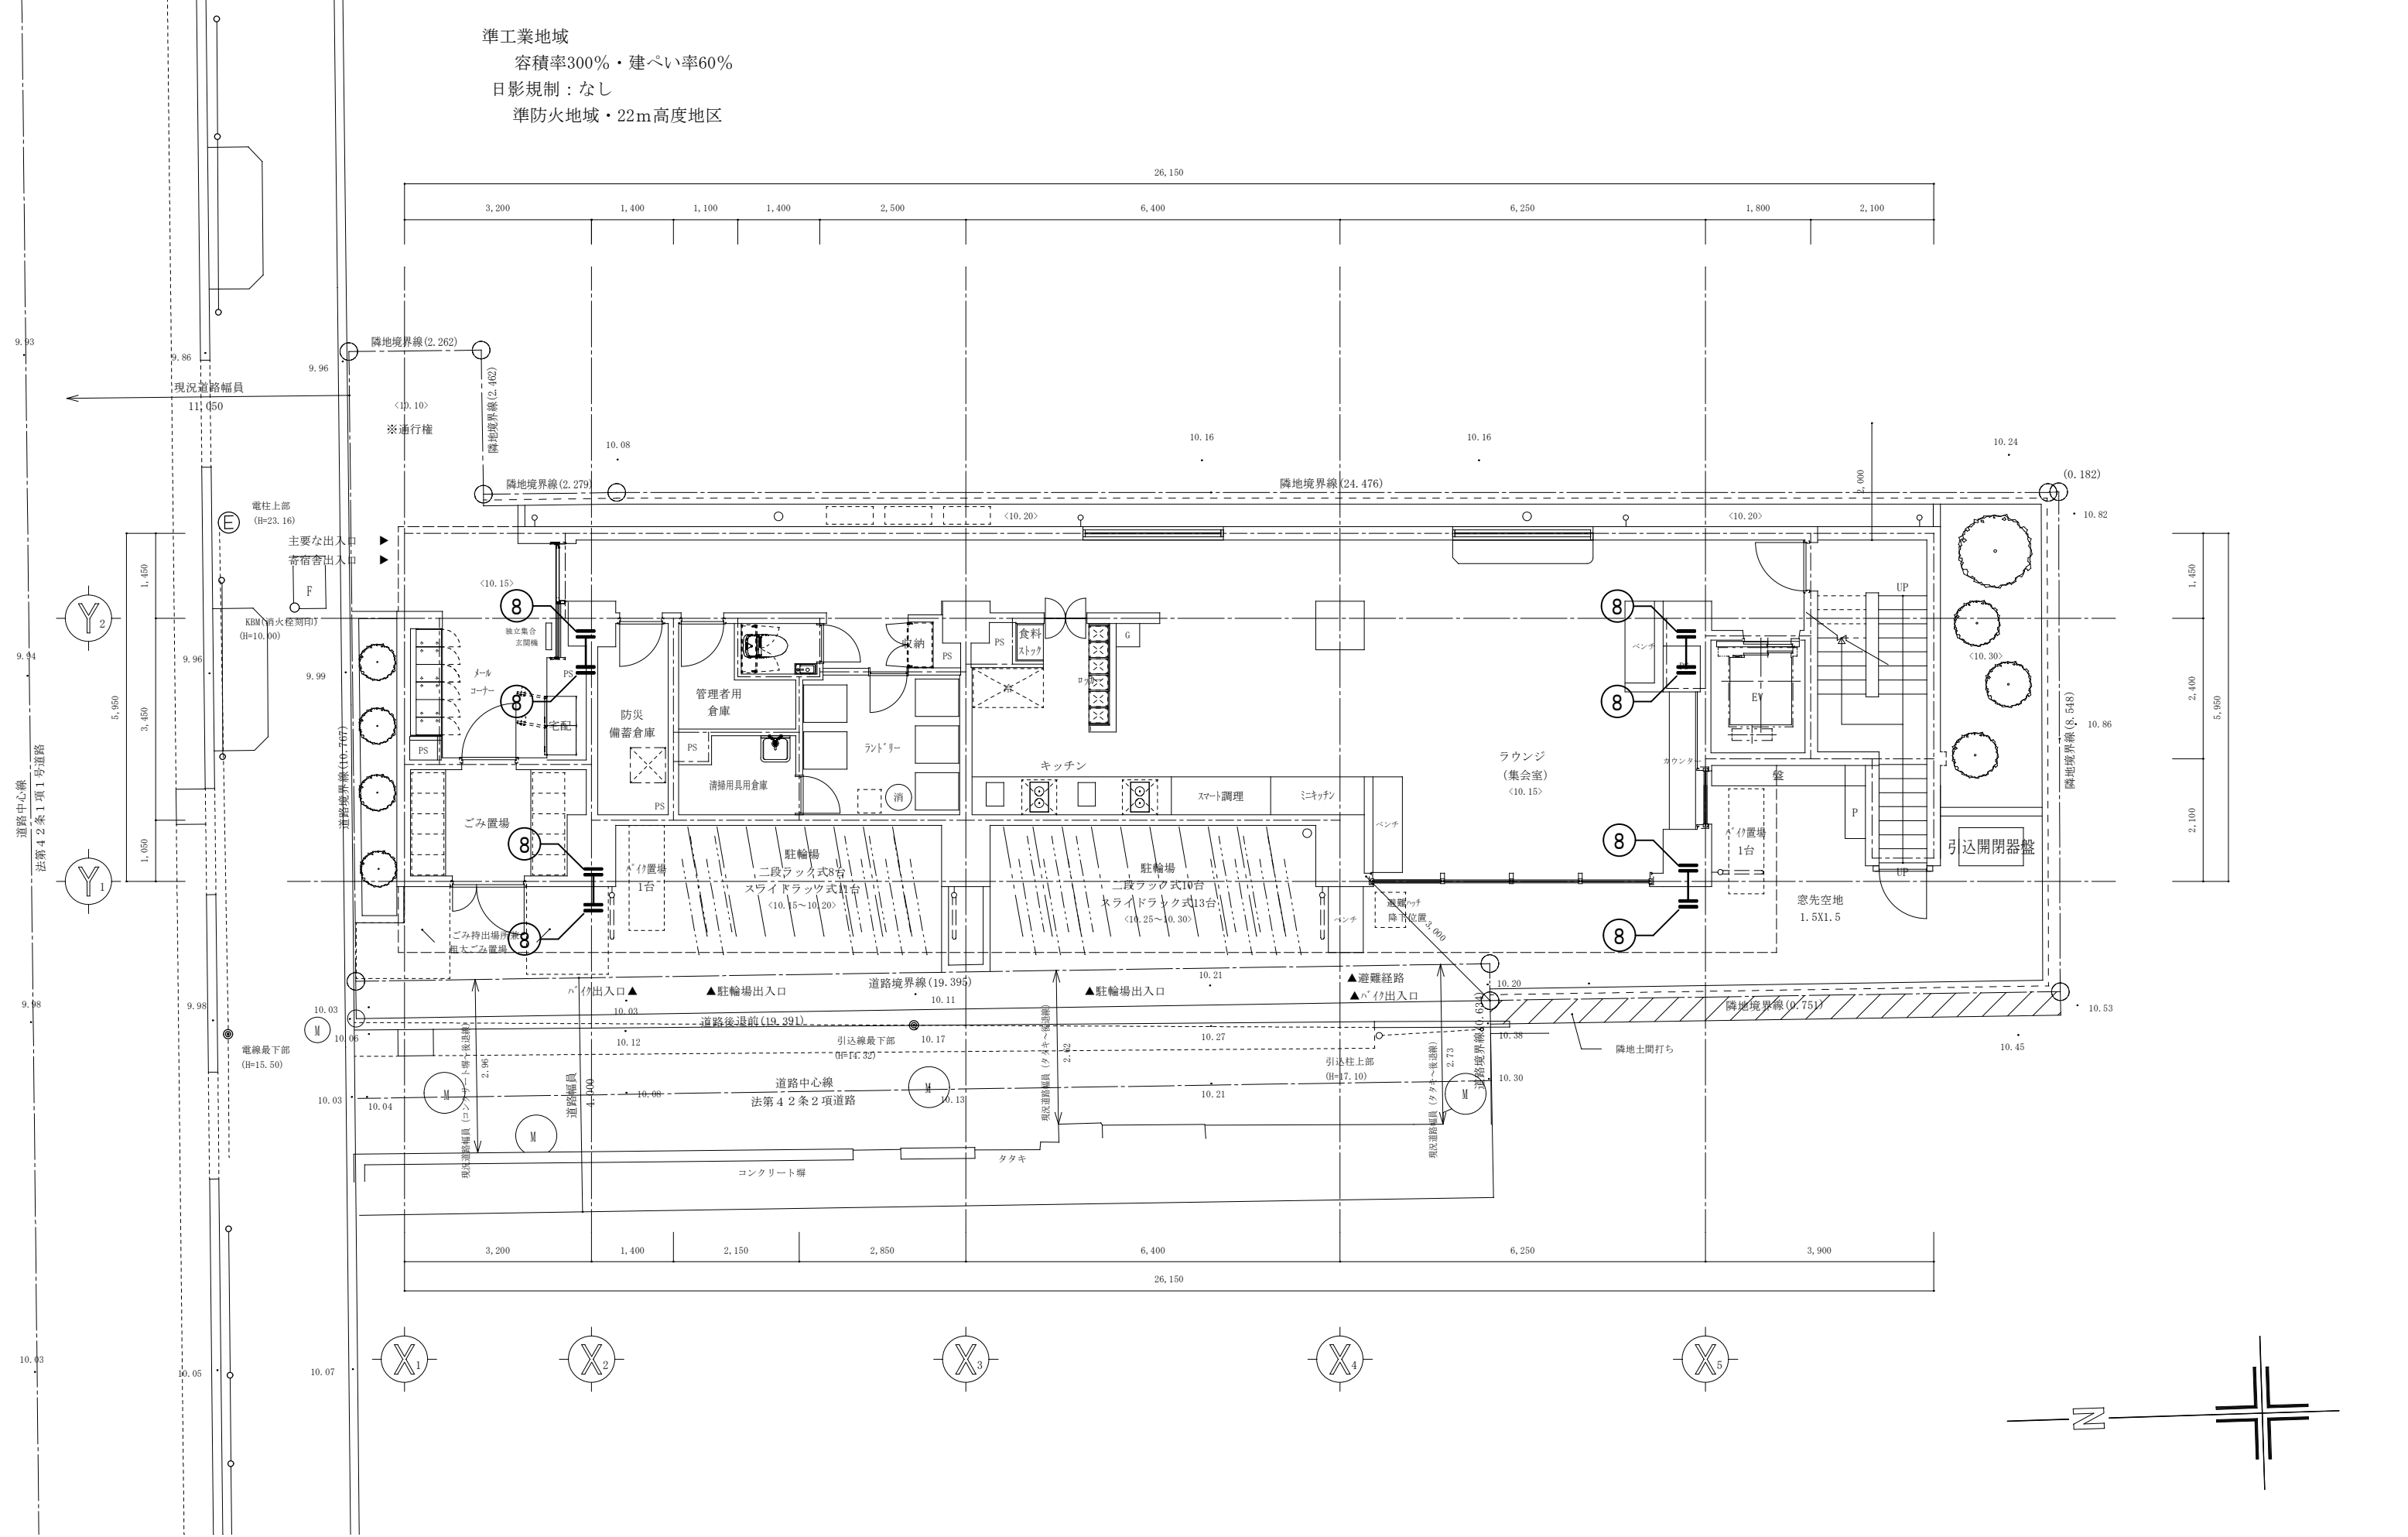

確認 E - 1 1

Date	Revision	Ck.	Date	Revision	Ck.

Checked	Date

Drawn	Date

株式会社 小野田建築設計事務所
ARCHITECTURE & ENGINEERING Dept.
一級建築士登録第255585号 小野田 貴夫

Project title
(仮称) 墨田区石原2丁目計画 新築工事
Sheet content
避雷針設備 平面図 (1)

Scale	Unit
1/100	MM
Sheet No.	
E - 2 8	

避雷設備凡例

番号	記号	名 称
1		突針 JIS中型
2		支持管 鋼管 (STK400) 溶融亜鉛めっき 60.5φ (3. 2 t) 3m~89.1φ (4. 2 t) 5m 8m
3		支持管取付台 基礎：建築工事
4		アルミ線 2. 0 × 19本 アルミ線取付金物 水平φ800 接着用・床用
5		T型クランプ
6		水切端子
7		1V 22mm²
8		鉄筋接続クランプ (2条に接続)

※ JIS Z 9290-3：2019規定に基づく。

※ 接地極：構造体利用接地極

※ 受雷部導体の突角部は30mm以上突出させること。

保護クラスに応じた受雷部の配置

保 護 クラス	回転球体法 R (m)	メッシュ法幅 (m)
Ⅳ	60	20×20

※ 回転球体法・メッシュ法を適用する。

※ 備考1. Rは、回転球体法の球体半径。

保護クラスに応じた引下げ導線の必要箇所数

保護クラス	平均間隔 (m)
Ⅳ	20


構造体受雷部利用の材料及び使用条件

材料	厚さt (mm)	厚さt' (mm)	断面積 (mm²)
鉄 (ステンレス・亜鉛めっき鋼)	4	0. 5	50
銅	5	0. 5	50
アルミニウム合金	7	0. 65	50


被保護物等を覆う金属板として、1) 及び4) を満足し、かつ、2) 又は3) を満足しなければならない。
1) 種々の部品間の電気的連続性が、恒久的であるもの (例 貴顕ろう付、溶接、クランプ、圧着、縫い合せ、ねじ止め又はボルト締め)
2) 金属板が雷放電によって穴があいても差し支えない構造の場合、又は金属板の下部に着火する可燃物がない場合、金属板の厚さがt' の値以上のもの
3) 雷放電による開孔及び局所加熱 (ホットスポット) を懸念する場合、金属板の厚さがt の値以上のもの
4) 絶縁物で覆われていない

構造体利用接地極

JIS Z 9290-3：2019 5. 4. 4 引
用
コンクリート基礎内の相互接続した鉄筋、又は他の適切な埋設金属構造物は、接地極として利用することが望ましい。
JIS Z 9290-3：2019 解説4. 6. 3 引
用
構造体利用接地極では、建築物等の地下部分構造体の鉄筋又は鉄骨を接地極とし、地上部分の鉄筋又は鉄骨を引下げ導線に利用する方法が最も望ましい。
構造体利用接地極と構造体利用引下げ導線の接続部分で、金属製構成部材相互の電気的接続が不十分な場合があるので建築物の建設時に相互の電気的連続性を確認する必要がある。

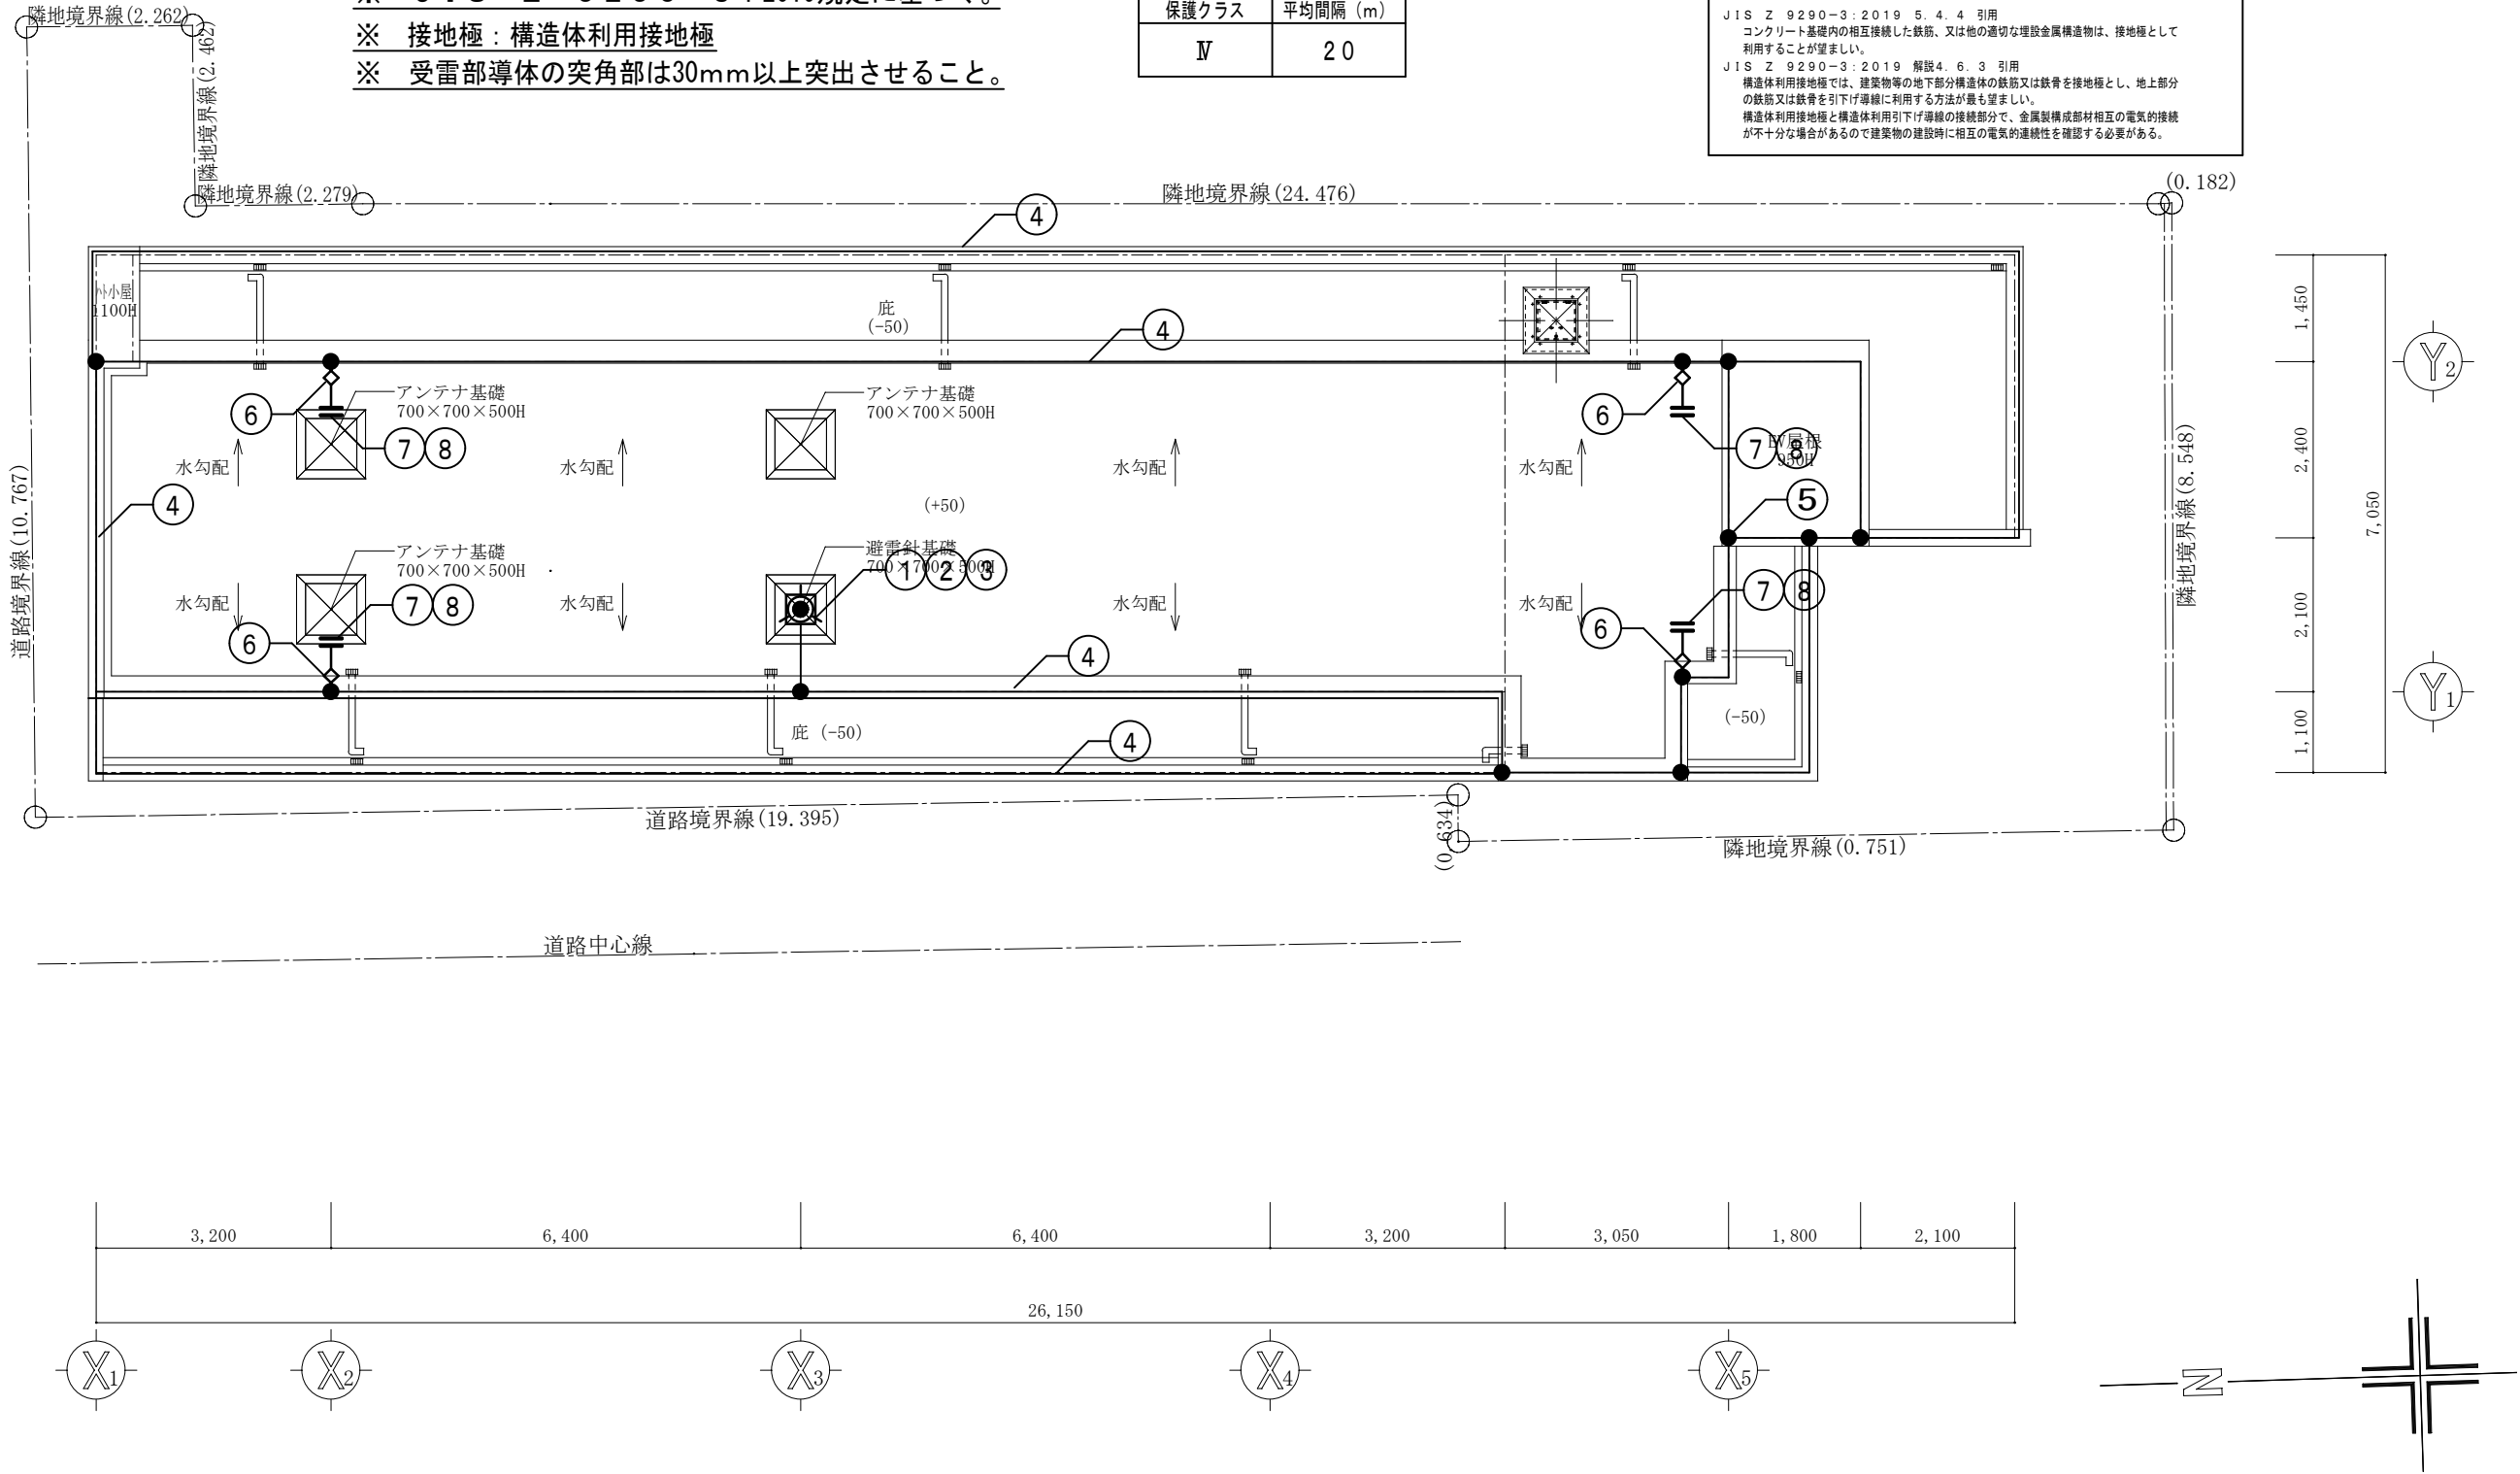

						確認 E-12	
Date	Revision	Ck.	Date	Revision	Ck.	Checked	Date
						Drawn	Date
						株式会社 小野田建築設計事務所 ARCHITECTURE & ENGINEERING Dept. 一級建築士登録第255585号 小野田 貴夫	
						Project title (仮称) 墨田区石原2丁目計画 新築工事 Sheet content 避雷針設備 平面図 (3)	
						Scale	Unit
						1/100	MM
						Sheet No.	E-29

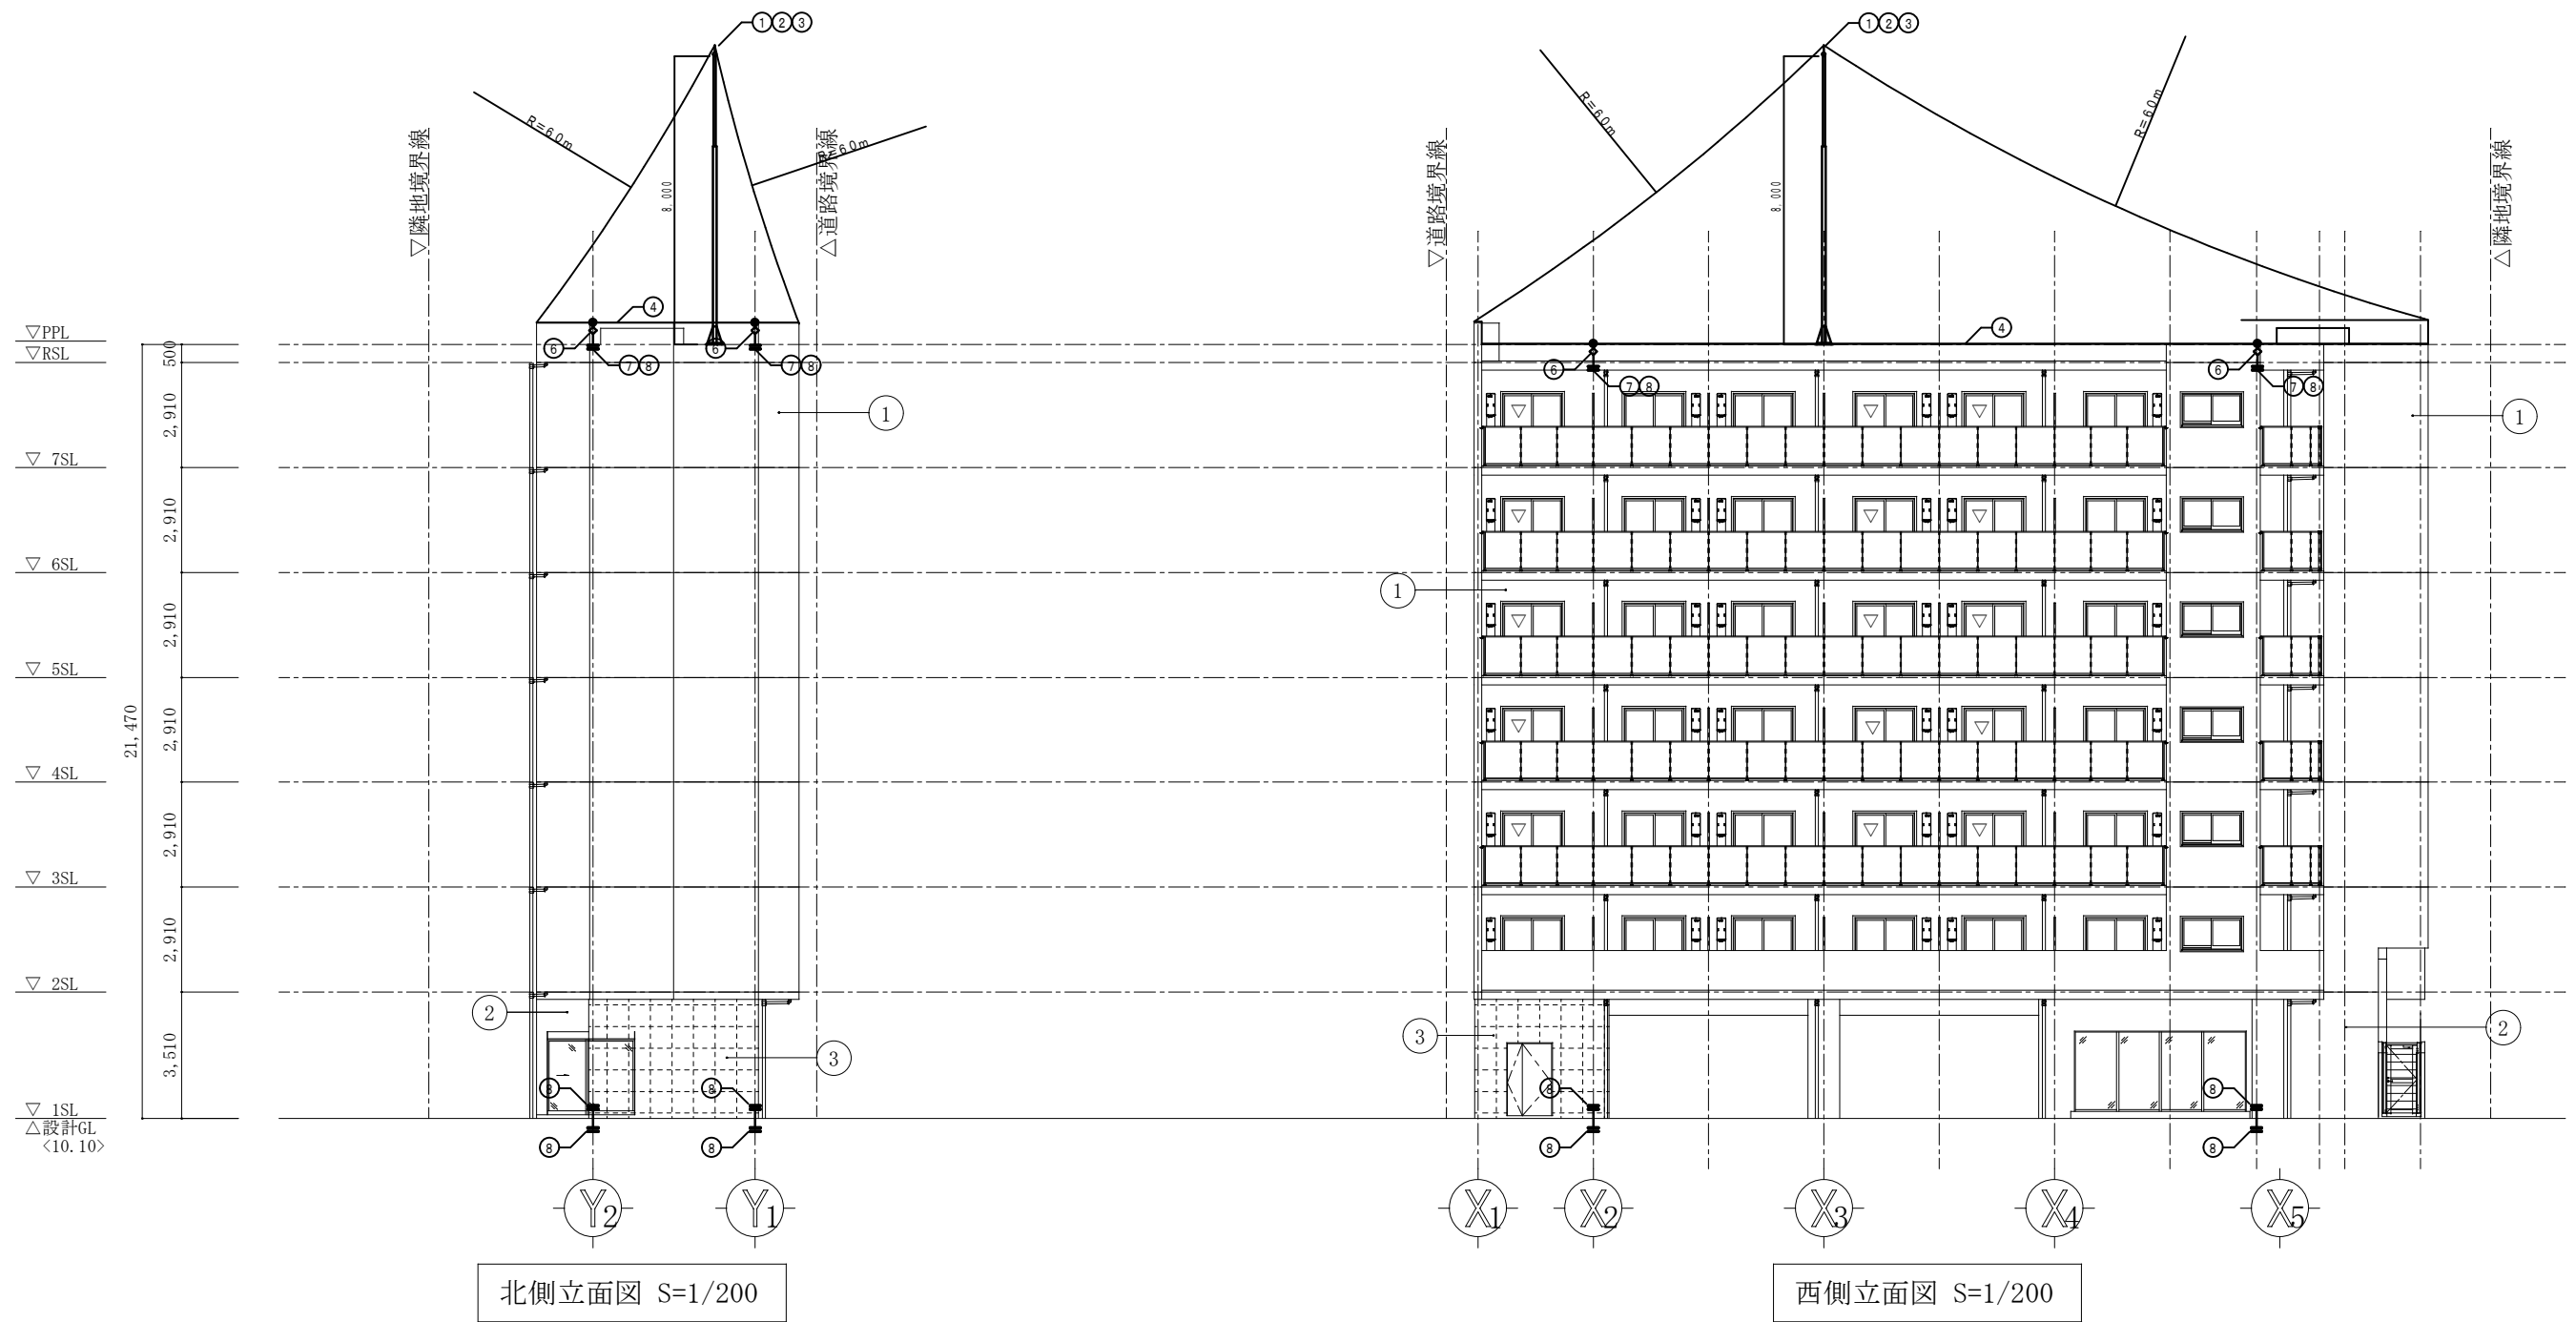

						確認 E - 1 3	
Date	Revision	Ck.	Date	Revision	Ck.	Scale	Unit
						1/200	MM
						Sheet No.	
						E - 3 0	
						Project title	
						(仮称) 墨田区石原2丁目計画 新築工事	
						Sheet content	
						避雷針設備 北・西側立面図	
						株式会社 小野田建築設計事務所	
						ARCHITECTURE & ENGINEERING Dept.	
						一級建築士登録第255585号 小野田 貴夫	

